
MASTER PLAN - PROPOSAL C - GREEN VALLEY

مجمعالشلالات السكني - المقترحج :الوادي الأخضر

المخطط العام - القطعة 157 مقاطعة 53بابيوخت - 199,175 م² -إحداثيات UTM 38S

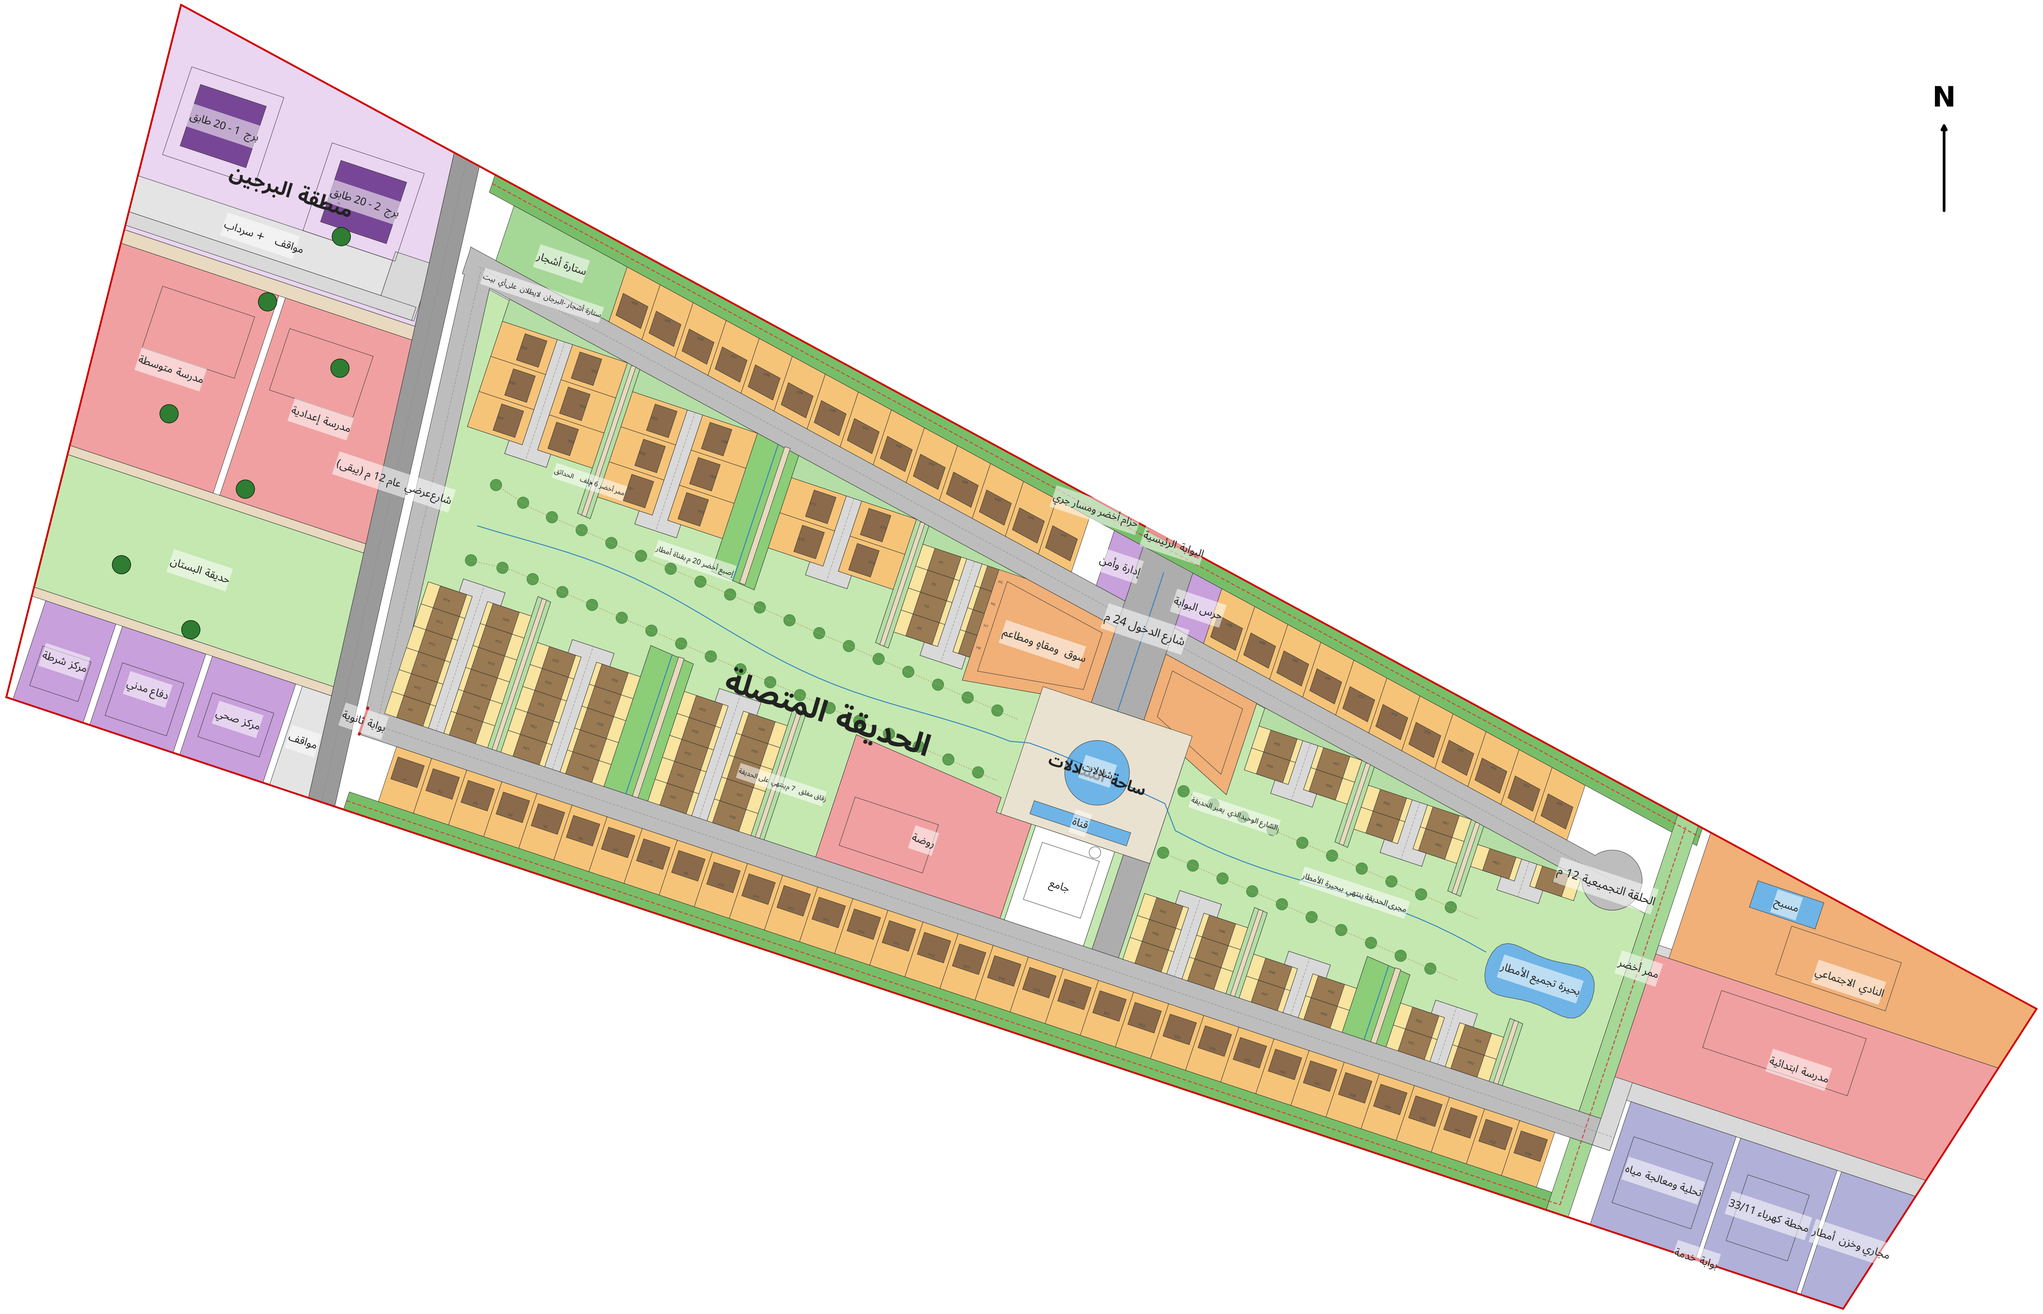

البرنامج

- فلل 400 م²: 74
- دور 200 م²: 64
- شقق البرجين : 152 (2برج × 19 طابقاً سكنياً × 4)
- المجموع: 290 وحدة
- السكان التقريبي : 1,588 نسمة
- الخضرة: 30%من القطعة
- كلبيت يطلمنالخلف على خضرة

استعمالات الأرض

- فلل 400 م²: 29,600 م² (14.9%)
- دور 200 م²: 12,800 م² (6.4%)
- منطقةالبرجين : 11,607 م² (5.8%)
- الخدمات العامة والتعليمية والتجارية والبنى التحتية: 48,401 م² (24.3%)
- الشوارعوالمواقف والساحة: 31,926 م² (16.0%)
- الحدائق والمساحات الخضراءوالممرات : 59,698 م² (30.0%)
- فضلاتوحواف : 5,146 م² (2.6%)
- المجموع: 199,177 م²

الخدمات - المرسوم /البرنامج (م²)

- الشارعالعرضي العام: 3,403
- مركز شرطة: 1,440 / 1,200
- دفاعمدني : 1,710 / 1,500
- مركز صحي : 1,710 / 1,500
- حديقةالبستان : 8,010
- مدرسة متوسطة: 6,179 / 4,800
- مدرسة إعدادية: 5,591 / 4,100
- منطقةالبرجين : 11,607 / 25,300
- إدارةوأمن البوابات : 700 / 1,500
- سوق ومقاهٍ ومطاعم: 4,011 / 3,500
- جامع: 1,548 / 1,500
- روضة: 4,276 / 3,600
- تحلية ومعالجة مياه: 2,688 / 2,500
- محطة كهرباء 33/11: 2,464 / 2,500
- مجاري وخزن أمطار: 1,489 / 1,500
- مدرسة ابتدائية: 8,345 / 7,700
- النادي الاجتماعي : 6,740 / 4,000

- فيلا 400 م²
- دار 200 م²
- برج 20 طابق
- تعليم
- خدمات عامة
- تجاري ونادي
- مسار جري
- بنى تحتية
- حديقة
- إصبع أخضر
- حزام أخضر
- ماء
- شوارع