


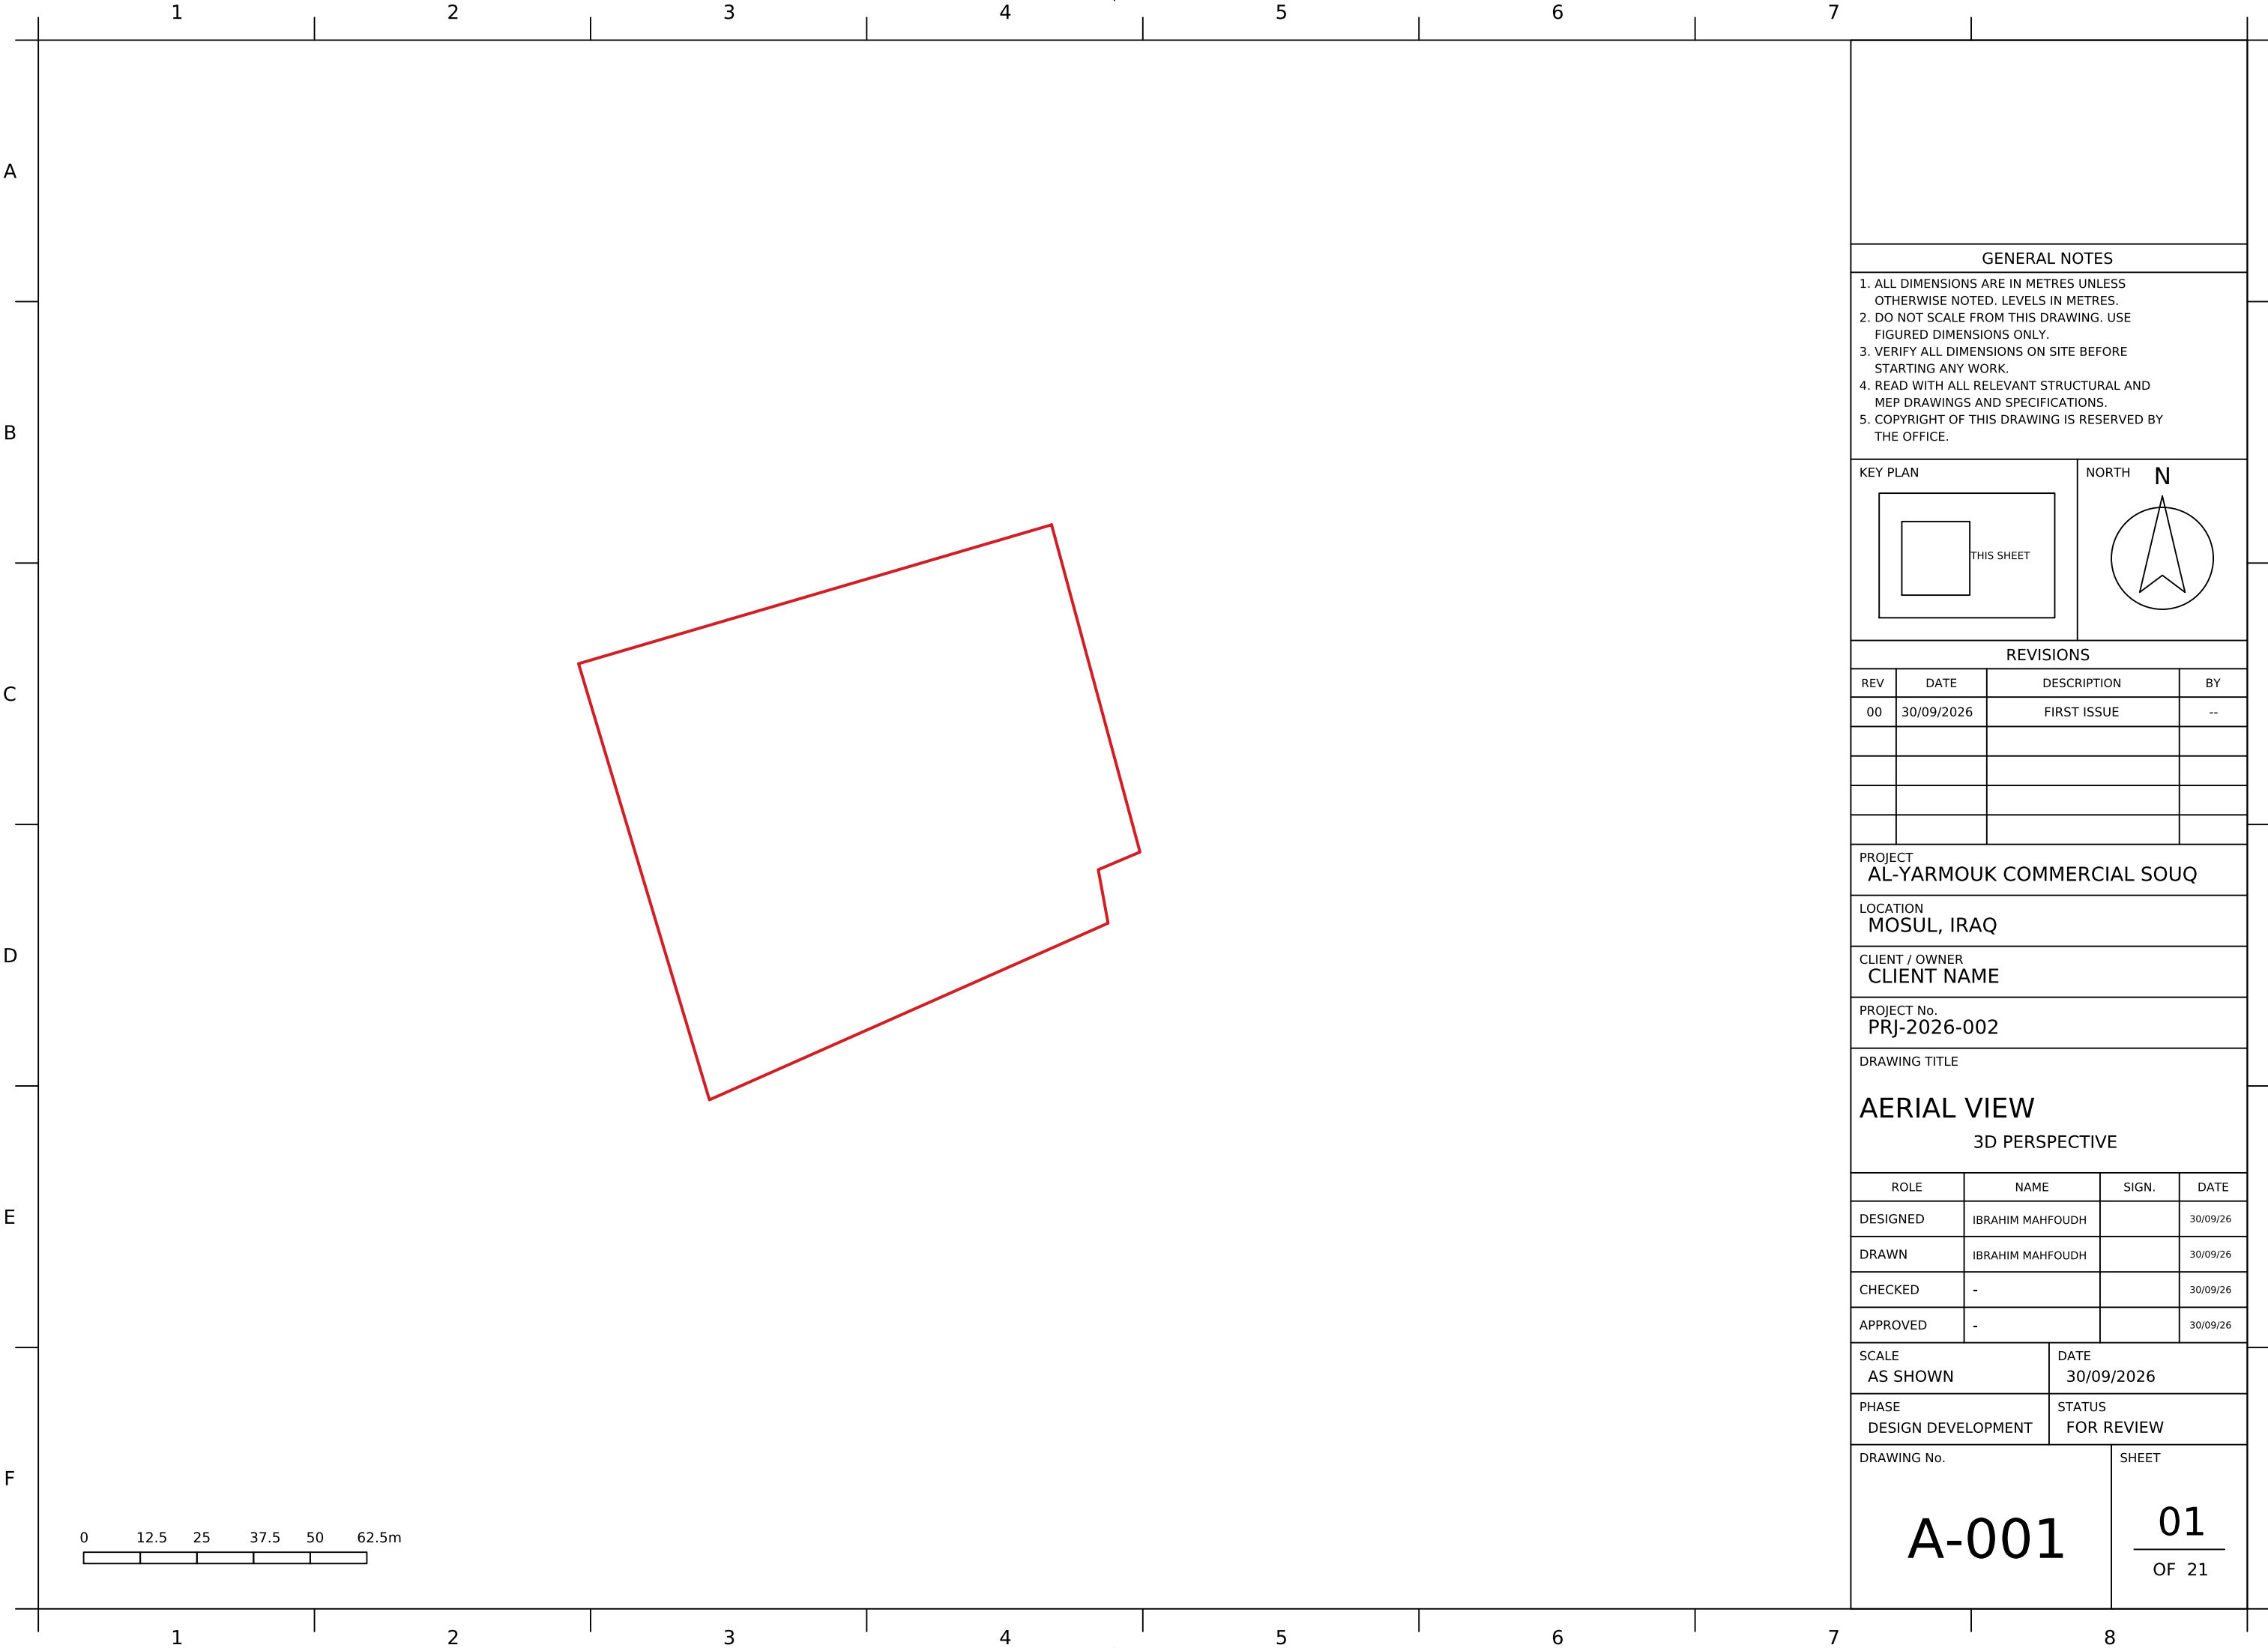

GENERAL NOTES

1. ALL DIMENSIONS ARE IN METRES UNLESS OTHERWISE NOTED. LEVELS IN METRES.
2. DO NOT SCALE FROM THIS DRAWING. USE FIGURED DIMENSIONS ONLY.
3. VERIFY ALL DIMENSIONS ON SITE BEFORE STARTING ANY WORK.
4. READ WITH ALL RELEVANT STRUCTURAL AND MEP DRAWINGS AND SPECIFICATIONS.
5. COPYRIGHT OF THIS DRAWING IS RESERVED BY THE OFFICE.

KEY PLAN

NORTH

N

REVISIONS			
REV	DATE	DESCRIPTION	BY
00	30/09/2026	FIRST ISSUE	--

PROJECT
AL-YARMOUK COMMERCIAL SOUQ

LOCATION
MOSUL, IRAQ

CLIENT / OWNER
CLIENT NAME

PROJECT No.
PRJ-2026-002

DRAWING TITLE

AERIAL VIEW

3D PERSPECTIVE

ROLE	NAME	SIGN.	DATE
DESIGNED	IBRAHIM MAHFOUDH		30/09/26
DRAWN	IBRAHIM MAHFOUDH		30/09/26
CHECKED	-		30/09/26
APPROVED	-		30/09/26

SCALE AS SHOWN	DATE 30/09/2026
-------------------	--------------------

PHASE DESIGN DEVELOPMENT	STATUS FOR REVIEW
-----------------------------	----------------------


DRAWING No.

A-001

SHEET

01


OF 21

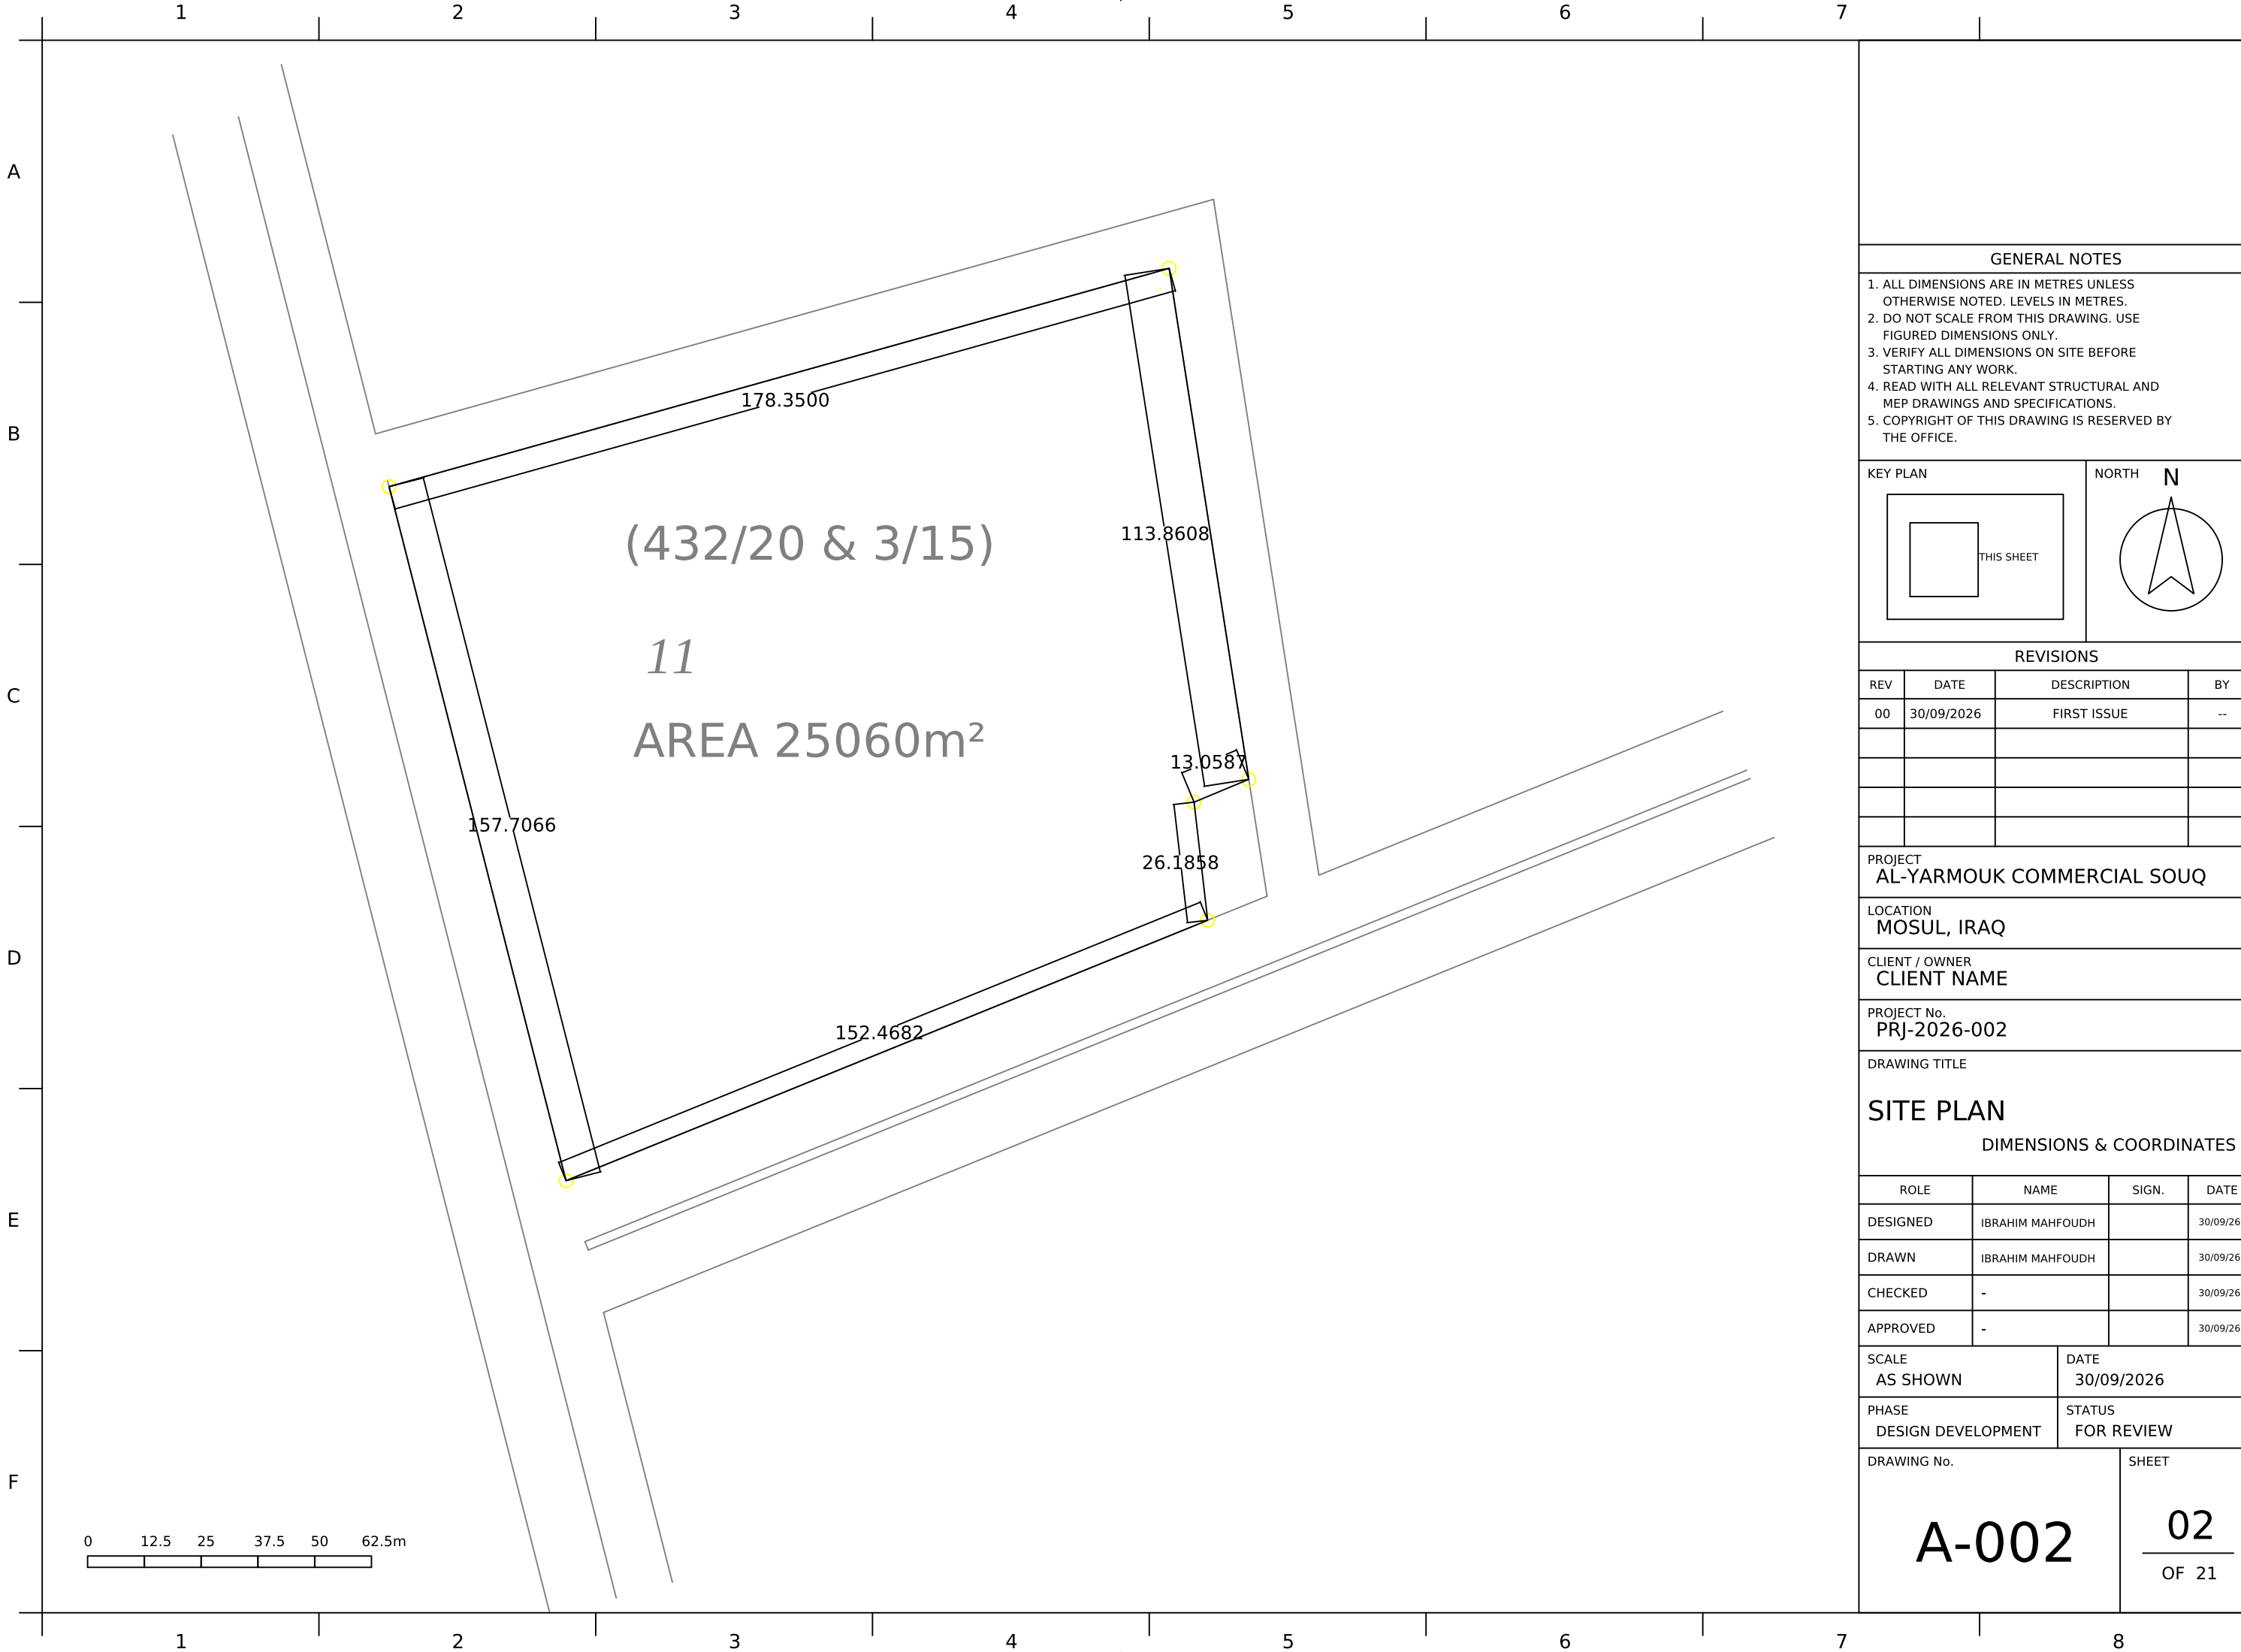

GENERAL NOTES

- 1. ALL DIMENSIONS ARE IN METRES UNLESS OTHERWISE NOTED. LEVELS IN METRES.
- 2. DO NOT SCALE FROM THIS DRAWING. USE FIGURED DIMENSIONS ONLY.
- 3. VERIFY ALL DIMENSIONS ON SITE BEFORE STARTING ANY WORK.
- 4. READ WITH ALL RELEVANT STRUCTURAL AND MEP DRAWINGS AND SPECIFICATIONS.
- 5. COPYRIGHT OF THIS DRAWING IS RESERVED BY THE OFFICE.


KEY PLAN

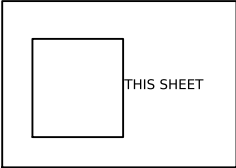

THIS SHEET

NORTH

N

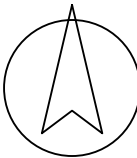

REVISIONS

REV	DATE	DESCRIPTION	BY
00	30/09/2026	FIRST ISSUE	--

PROJECT
AL-YARMOUK COMMERCIAL SOUQ

LOCATION
MOSUL, IRAQ

CLIENT / OWNER
CLIENT NAME

PROJECT No.
PRJ-2026-002

DRAWING TITLE

SITE PLAN
DIMENSIONS & COORDINATES

ROLE	NAME	SIGN.	DATE
DESIGNED	IBRAHIM MAHFOUDH		30/09/26
DRAWN	IBRAHIM MAHFOUDH		30/09/26
CHECKED	-		30/09/26
APPROVED	-		30/09/26

SCALE
AS SHOWN

DATE
30/09/2026

PHASE
DESIGN DEVELOPMENT


STATUS
FOR REVIEW


DRAWING No.

A-002

SHEET

02
OF 21

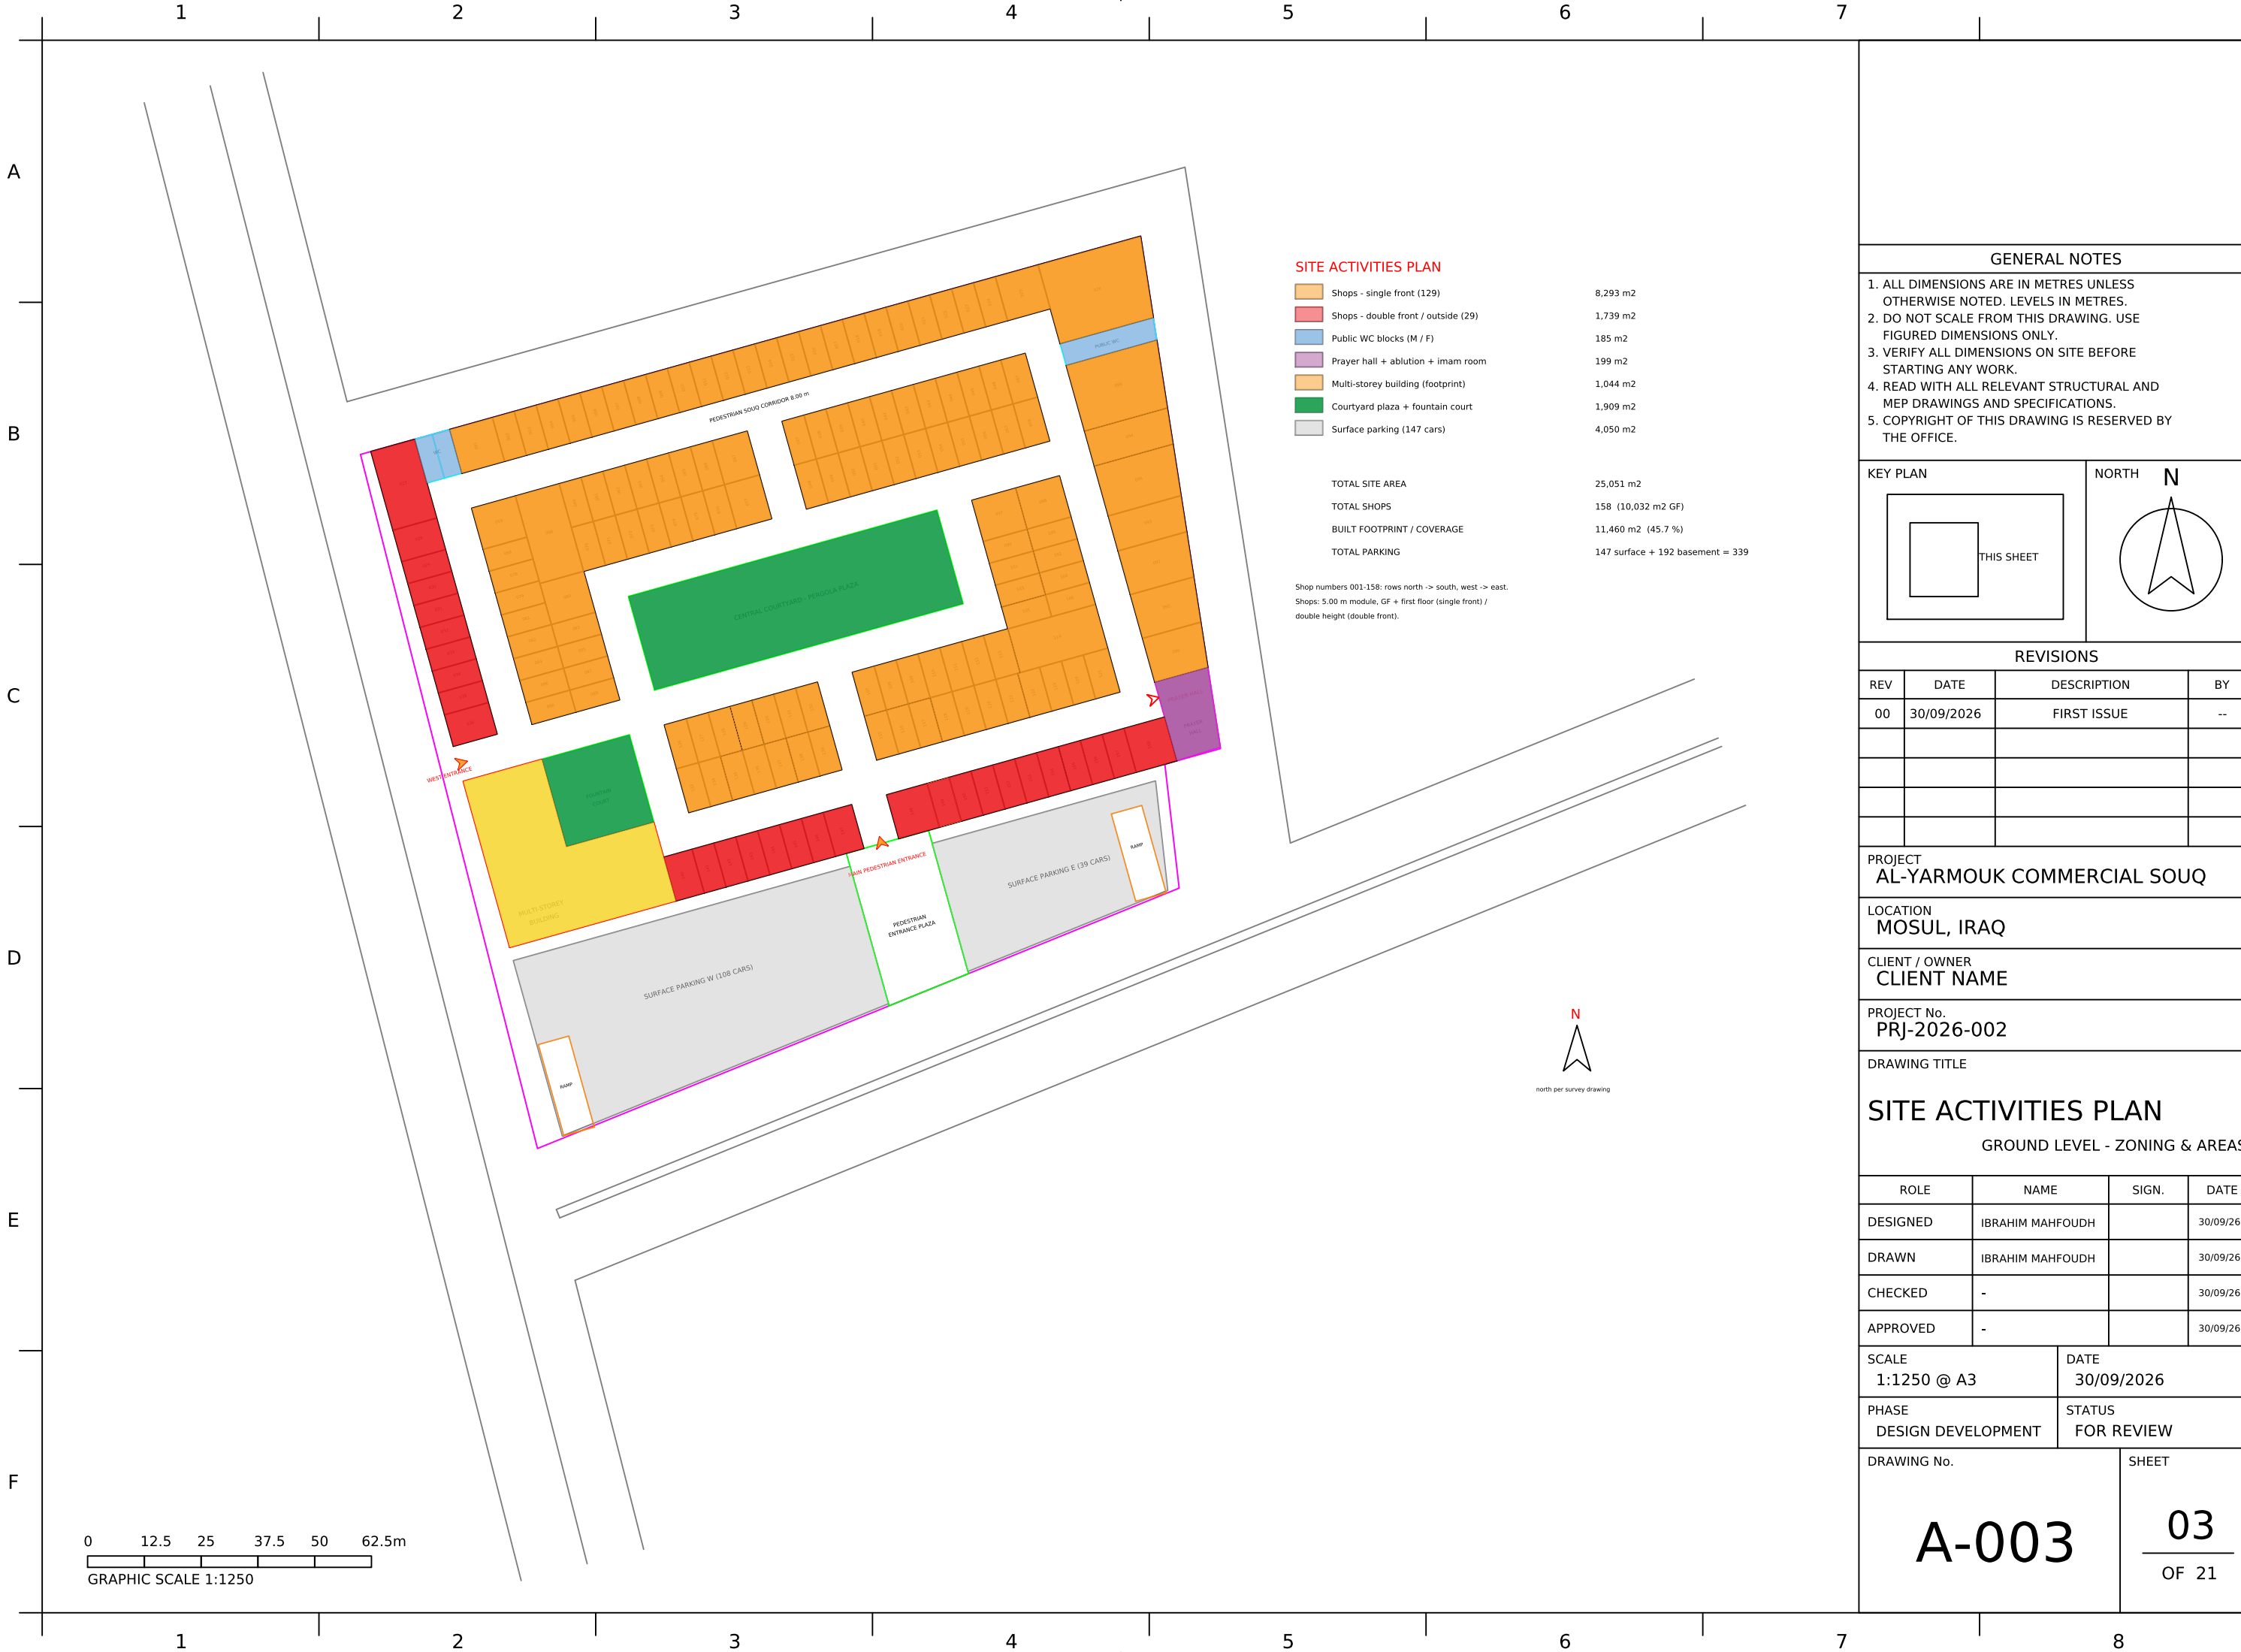

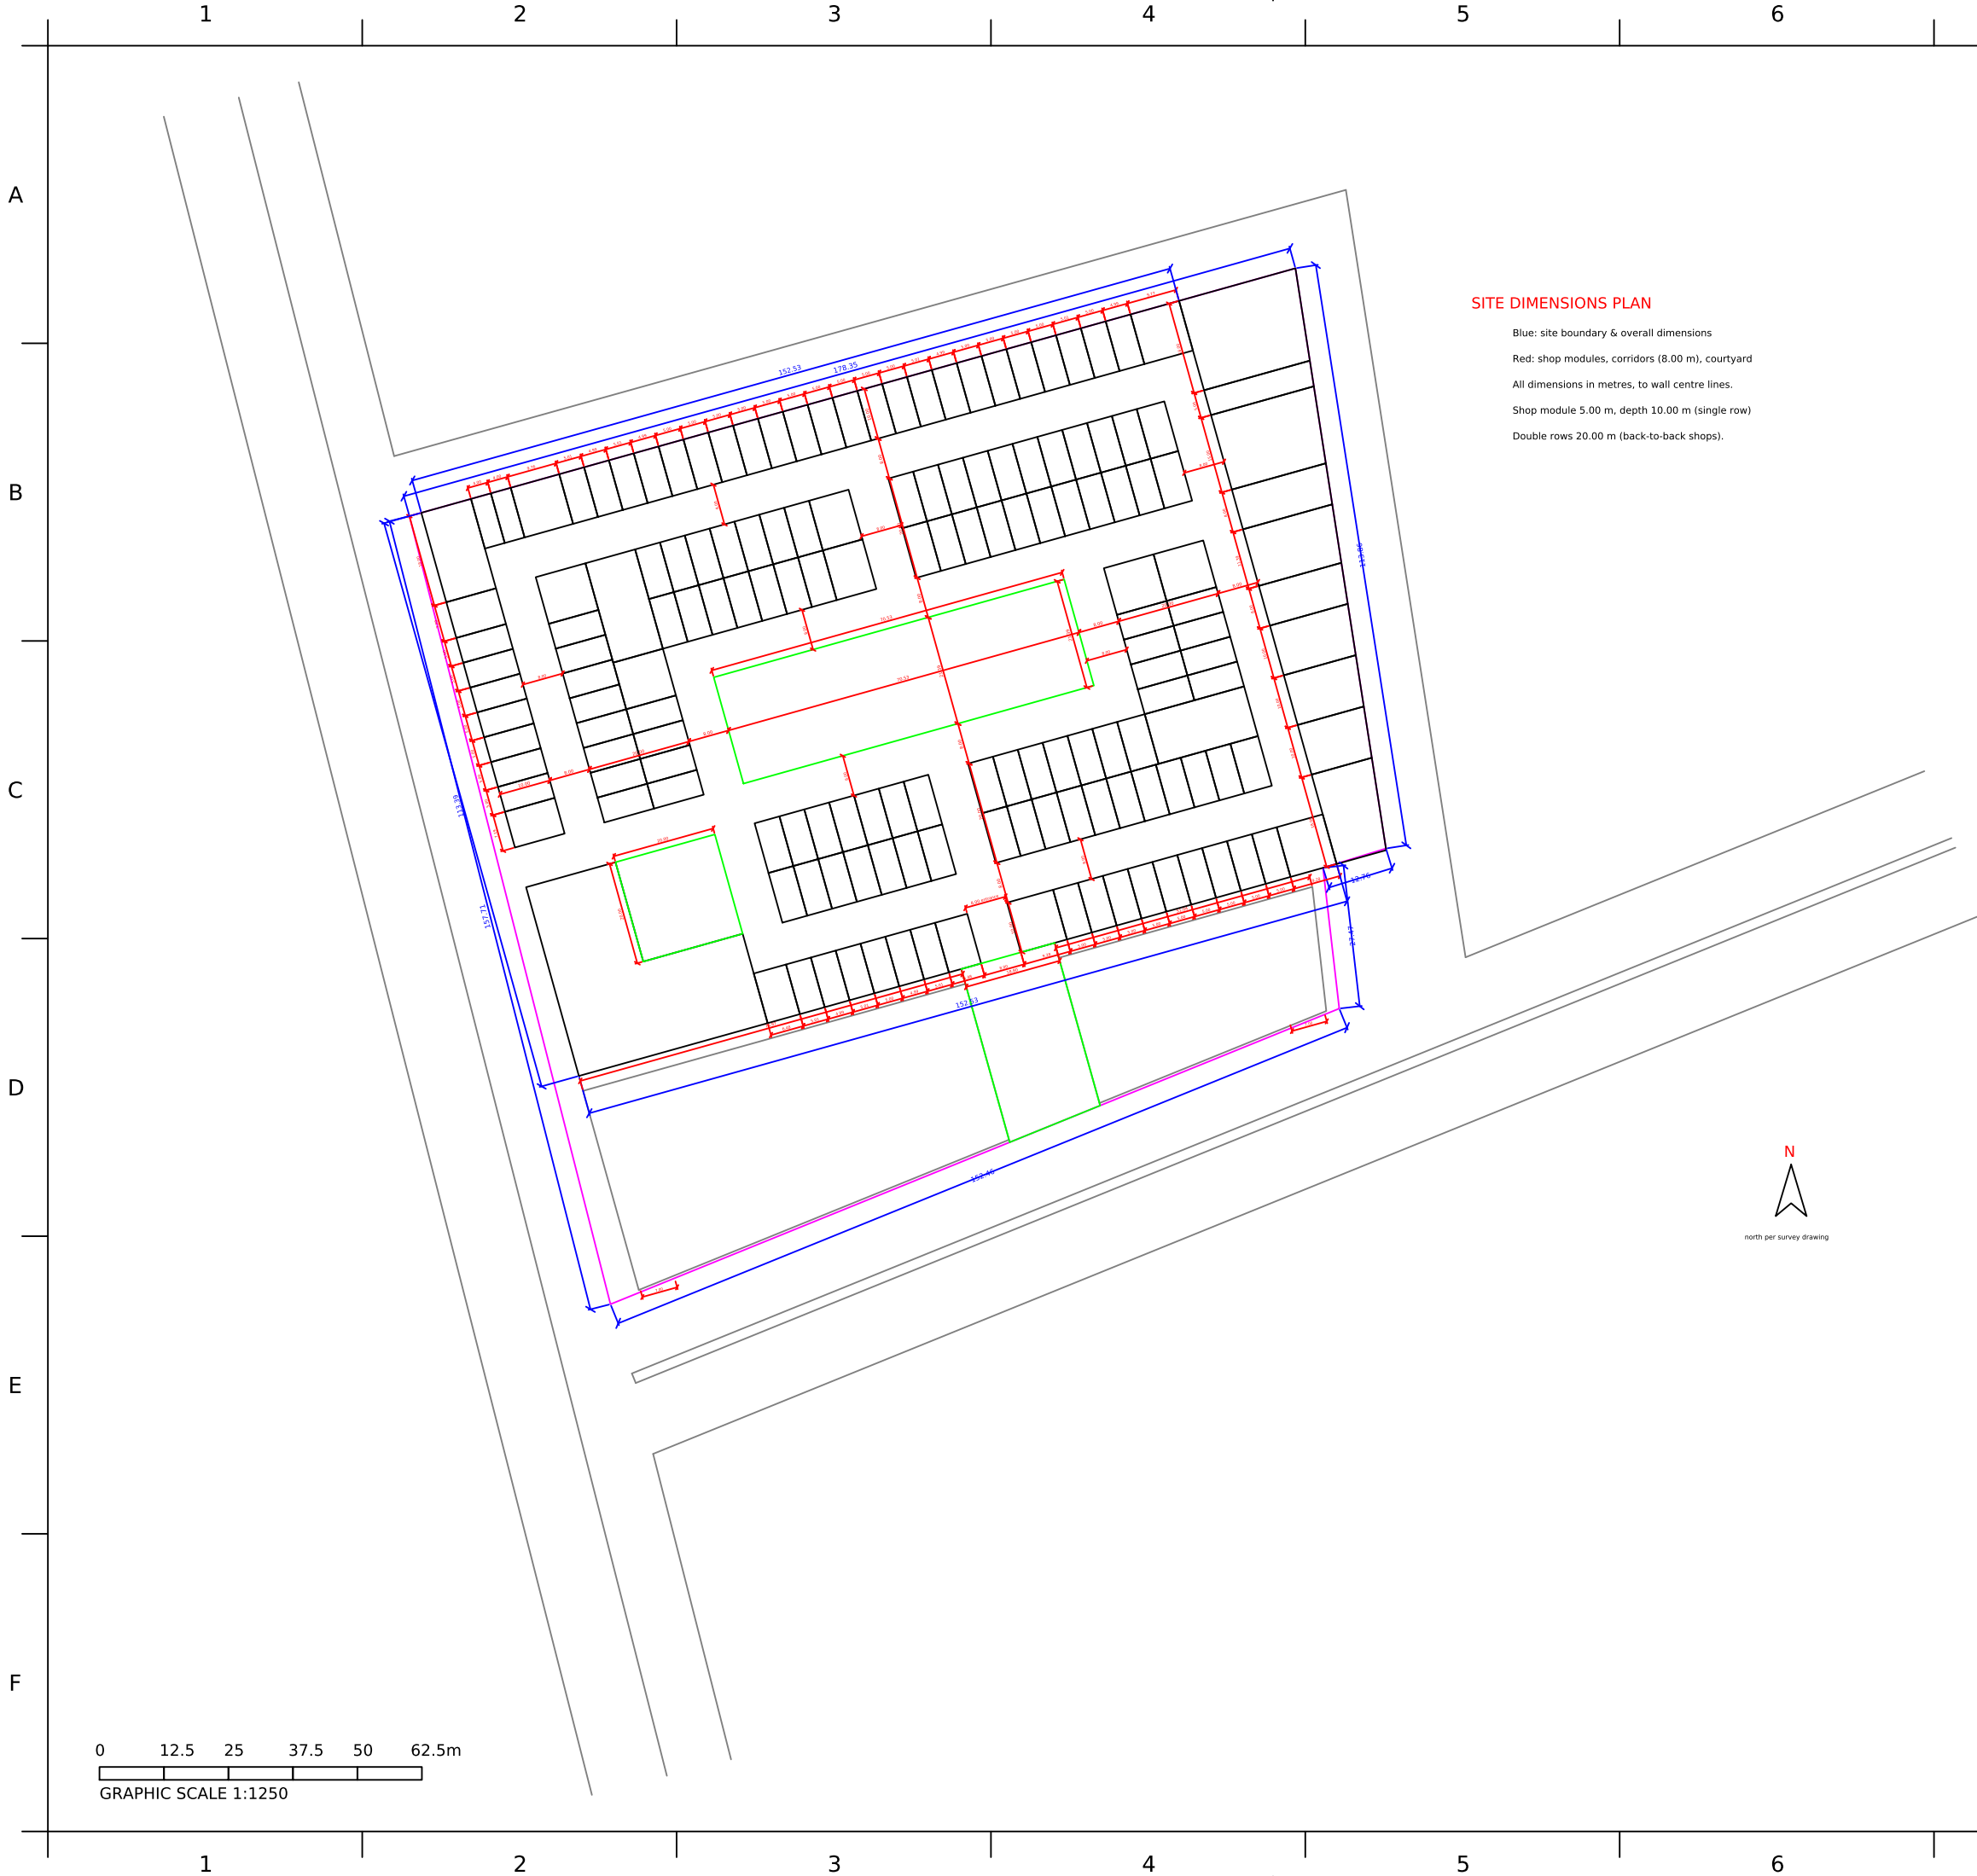


SITE DIMENSIONS PLAN

Blue: site boundary & overall dimensions
Red: shop modules, corridors (8.00 m), courtyard
All dimensions in metres, to wall centre lines.
Shop module 5.00 m, depth 10.00 m (single row)
Double rows 20.00 m (back-to-back shops).


GENERAL NOTES

- ALL DIMENSIONS ARE IN METRES UNLESS OTHERWISE NOTED. LEVELS IN METRES.
- DO NOT SCALE FROM THIS DRAWING. USE FIGURED DIMENSIONS ONLY.
- VERIFY ALL DIMENSIONS ON SITE BEFORE STARTING ANY WORK.
- READ WITH ALL RELEVANT STRUCTURAL AND MEP DRAWINGS AND SPECIFICATIONS.
- COPYRIGHT OF THIS DRAWING IS RESERVED BY THE OFFICE.

KEY PLAN

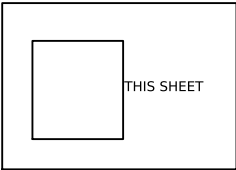

NORTH

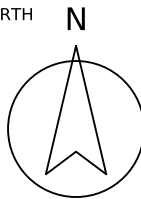

REVISIONS

REV	DATE	DESCRIPTION	BY
00	30/09/2026	FIRST ISSUE	--

PROJECT
AL-YARMOUK COMMERCIAL SOUQ

LOCATION
MOSUL, IRAQ

CLIENT / OWNER
CLIENT NAME

PROJECT No.
PRJ-2026-002

DRAWING TITLE

SITE DIMENSIONS PLAN
GROUND LEVEL

ROLE	NAME	SIGN.	DATE
DESIGNED	IBRAHIM MAHFOUDH		30/09/26
DRAWN	IBRAHIM MAHFOUDH		30/09/26
CHECKED	-		30/09/26
APPROVED	-		30/09/26



SCALE 1:1250 @ A3	DATE 30/09/2026
----------------------	--------------------

PHASE DESIGN DEVELOPMENT	STATUS FOR REVIEW
-----------------------------	----------------------

DRAWING No. A-005	SHEET 04 OF 21
--------------------------	--------------------------

BASEMENT (-1) CAR PARK PLAN | level -3.50


Parking stalls (2.50 x 5.00 m): 192
Gross basement area: 6,525 m2 (34.0 m2 / car)
Aisles 6.00 m two-way (green)
Two ramps 30 x 7 m, two-way, slope <= 15 %
Cores: stairs + lifts to the souq above (blue)
Services: shelter 60 m2, electrical room 20 m2, generator
Sprinklers & jet-fan ventilation to civil-defence requirements

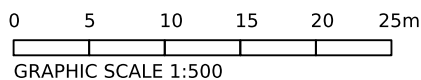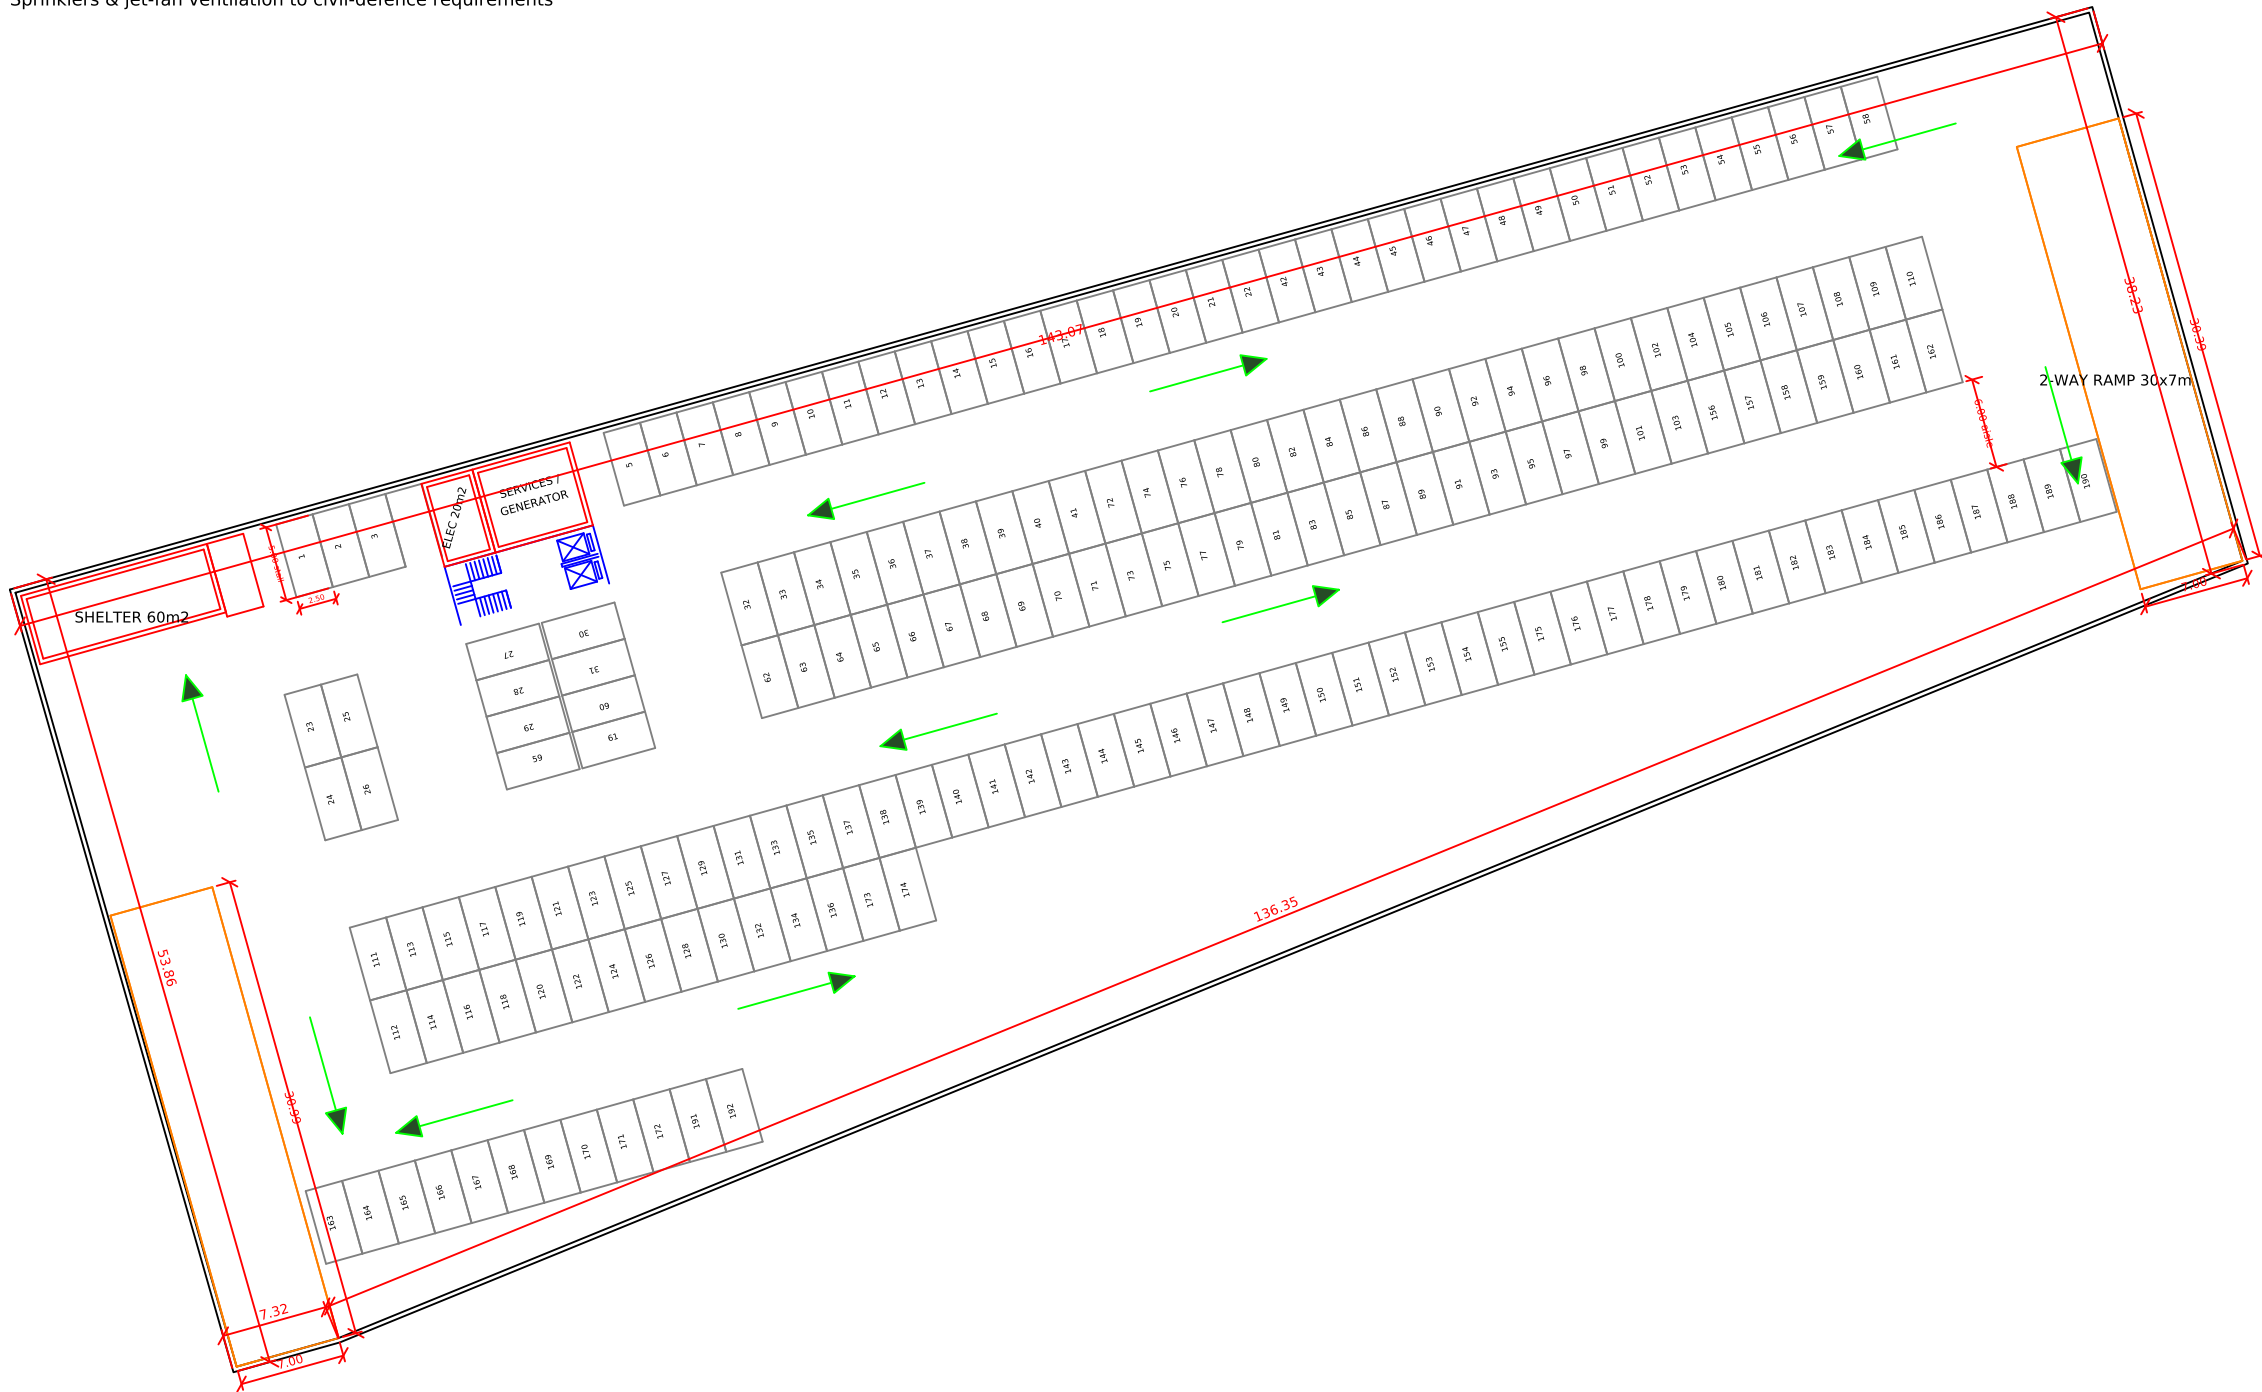

GENERAL NOTES

- ALL DIMENSIONS ARE IN METRES UNLESS OTHERWISE NOTED. LEVELS IN METRES.
- DO NOT SCALE FROM THIS DRAWING. USE FIGURED DIMENSIONS ONLY.
- VERIFY ALL DIMENSIONS ON SITE BEFORE STARTING ANY WORK.
- READ WITH ALL RELEVANT STRUCTURAL AND MEP DRAWINGS AND SPECIFICATIONS.
- COPYRIGHT OF THIS DRAWING IS RESERVED BY THE OFFICE.

KEY PLAN

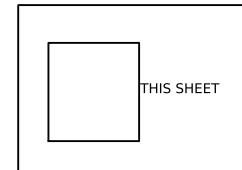

NORTH



REVISIONS

REV	DATE	DESCRIPTION	BY
00	30/09/2026	FIRST ISSUE	--

PROJECT
AL-YARMOUK COMMERCIAL SOUQ

LOCATION
MOSUL, IRAQ

CLIENT / OWNER
CLIENT NAME

PROJECT No.
PRJ-2026-002


DRAWING TITLE
BASEMENT CAR PARK
LEVEL -3.50 (192 CARS)

ROLE	NAME	SIGN.	DATE
DESIGNED	IBRAHIM MAHFOUDH		30/09/26
DRAWN	IBRAHIM MAHFOUDH		30/09/26
CHECKED	-		30/09/26
APPROVED	-		30/09/26

SCALE 1:500 @ A3	DATE 30/09/2026
---------------------	--------------------

PHASE DESIGN DEVELOPMENT	STATUS FOR REVIEW
-----------------------------	----------------------


DRAWING No. A-004	SHEET 05 OF 21
-----------------------------	-----------------------------

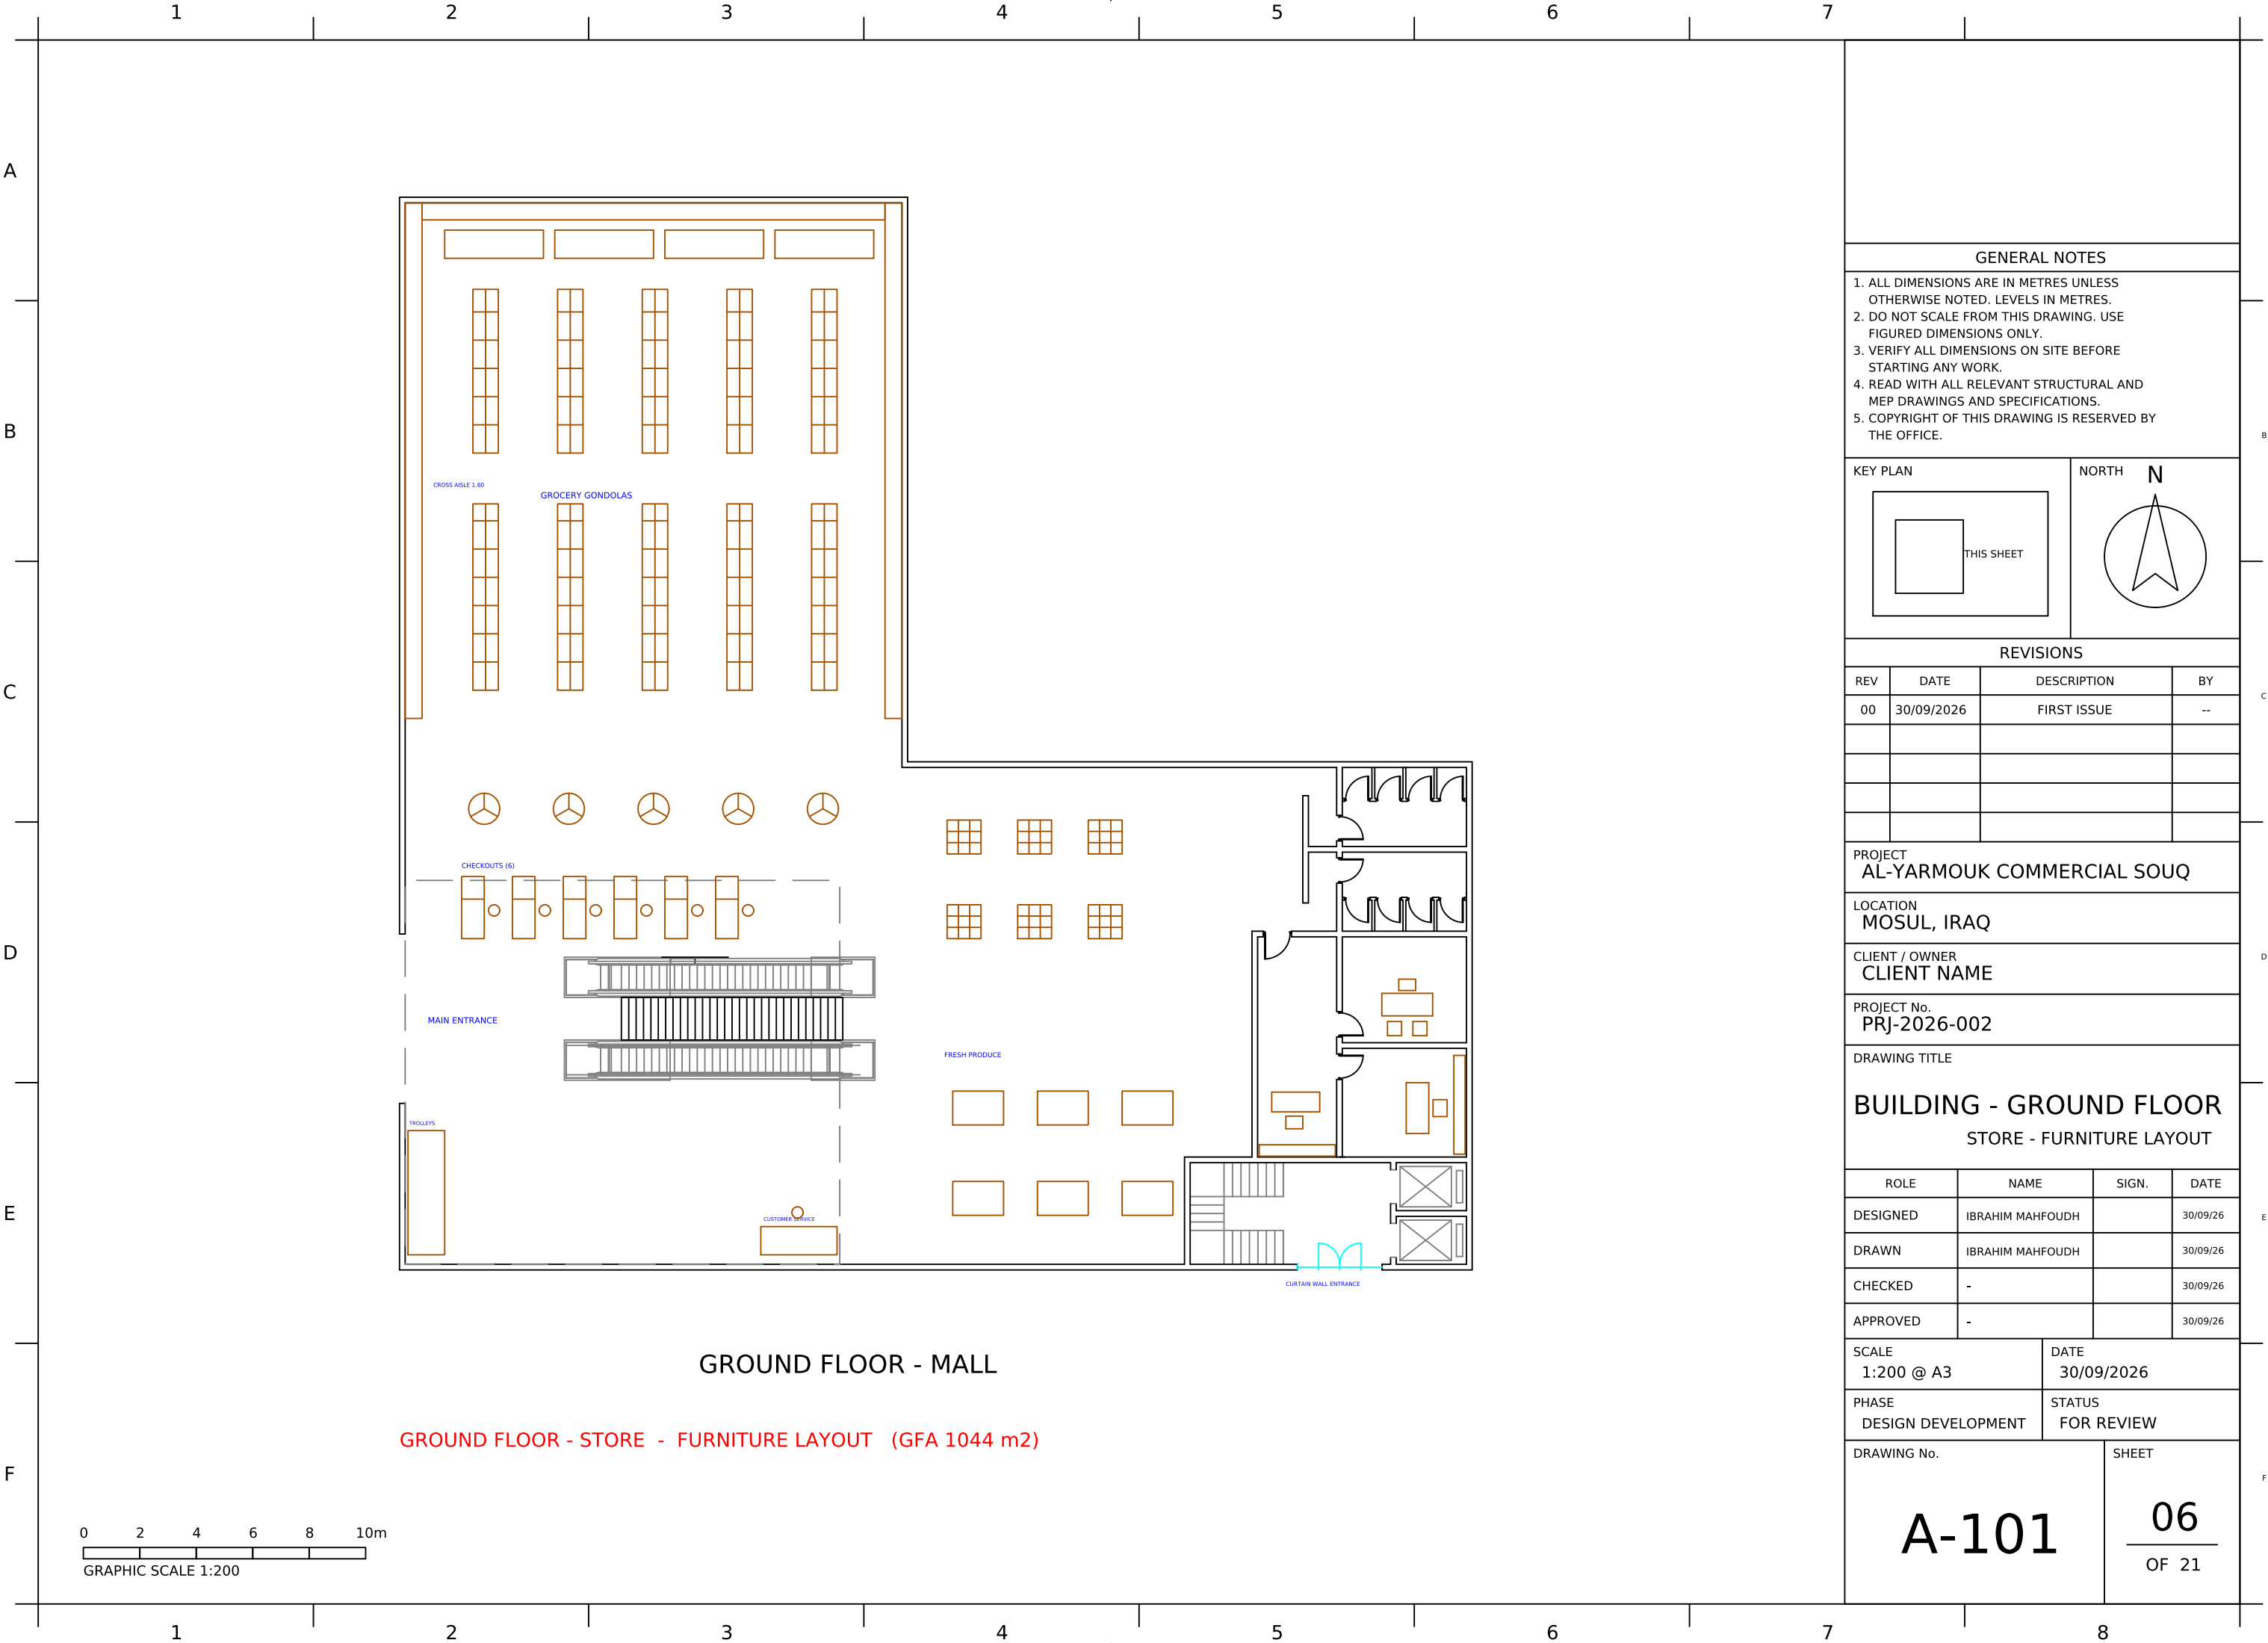

GENERAL NOTES

1. ALL DIMENSIONS ARE IN METRES UNLESS OTHERWISE NOTED. LEVELS IN METRES.
2. DO NOT SCALE FROM THIS DRAWING. USE FIGURED DIMENSIONS ONLY.
3. VERIFY ALL DIMENSIONS ON SITE BEFORE STARTING ANY WORK.
4. READ WITH ALL RELEVANT STRUCTURAL AND MEP DRAWINGS AND SPECIFICATIONS.
5. COPYRIGHT OF THIS DRAWING IS RESERVED BY THE OFFICE.

KEY PLAN

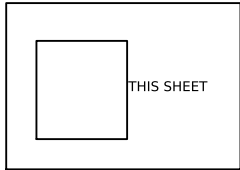

THIS SHEET

NORTH

N



REVISIONS

REV	DATE	DESCRIPTION	BY
00	30/09/2026	FIRST ISSUE	--

PROJECT
AL-YARMOUK COMMERCIAL SOUQ

LOCATION
MOSUL, IRAQ

CLIENT / OWNER
CLIENT NAME

PROJECT No.
PRJ-2026-002

DRAWING TITLE
BUILDING - GROUND FLOOR
STORE - FURNITURE LAYOUT

ROLE	NAME	SIGN.	DATE
DESIGNED	IBRAHIM MAHFOUDH		30/09/26
DRAWN	IBRAHIM MAHFOUDH		30/09/26
CHECKED	-		30/09/26
APPROVED	-		30/09/26

SCALE
1:200 @ A3

DATE
30/09/2026

PHASE
DESIGN DEVELOPMENT

STATUS
FOR REVIEW


DRAWING No.

A-101

SHEET

06


OF 21

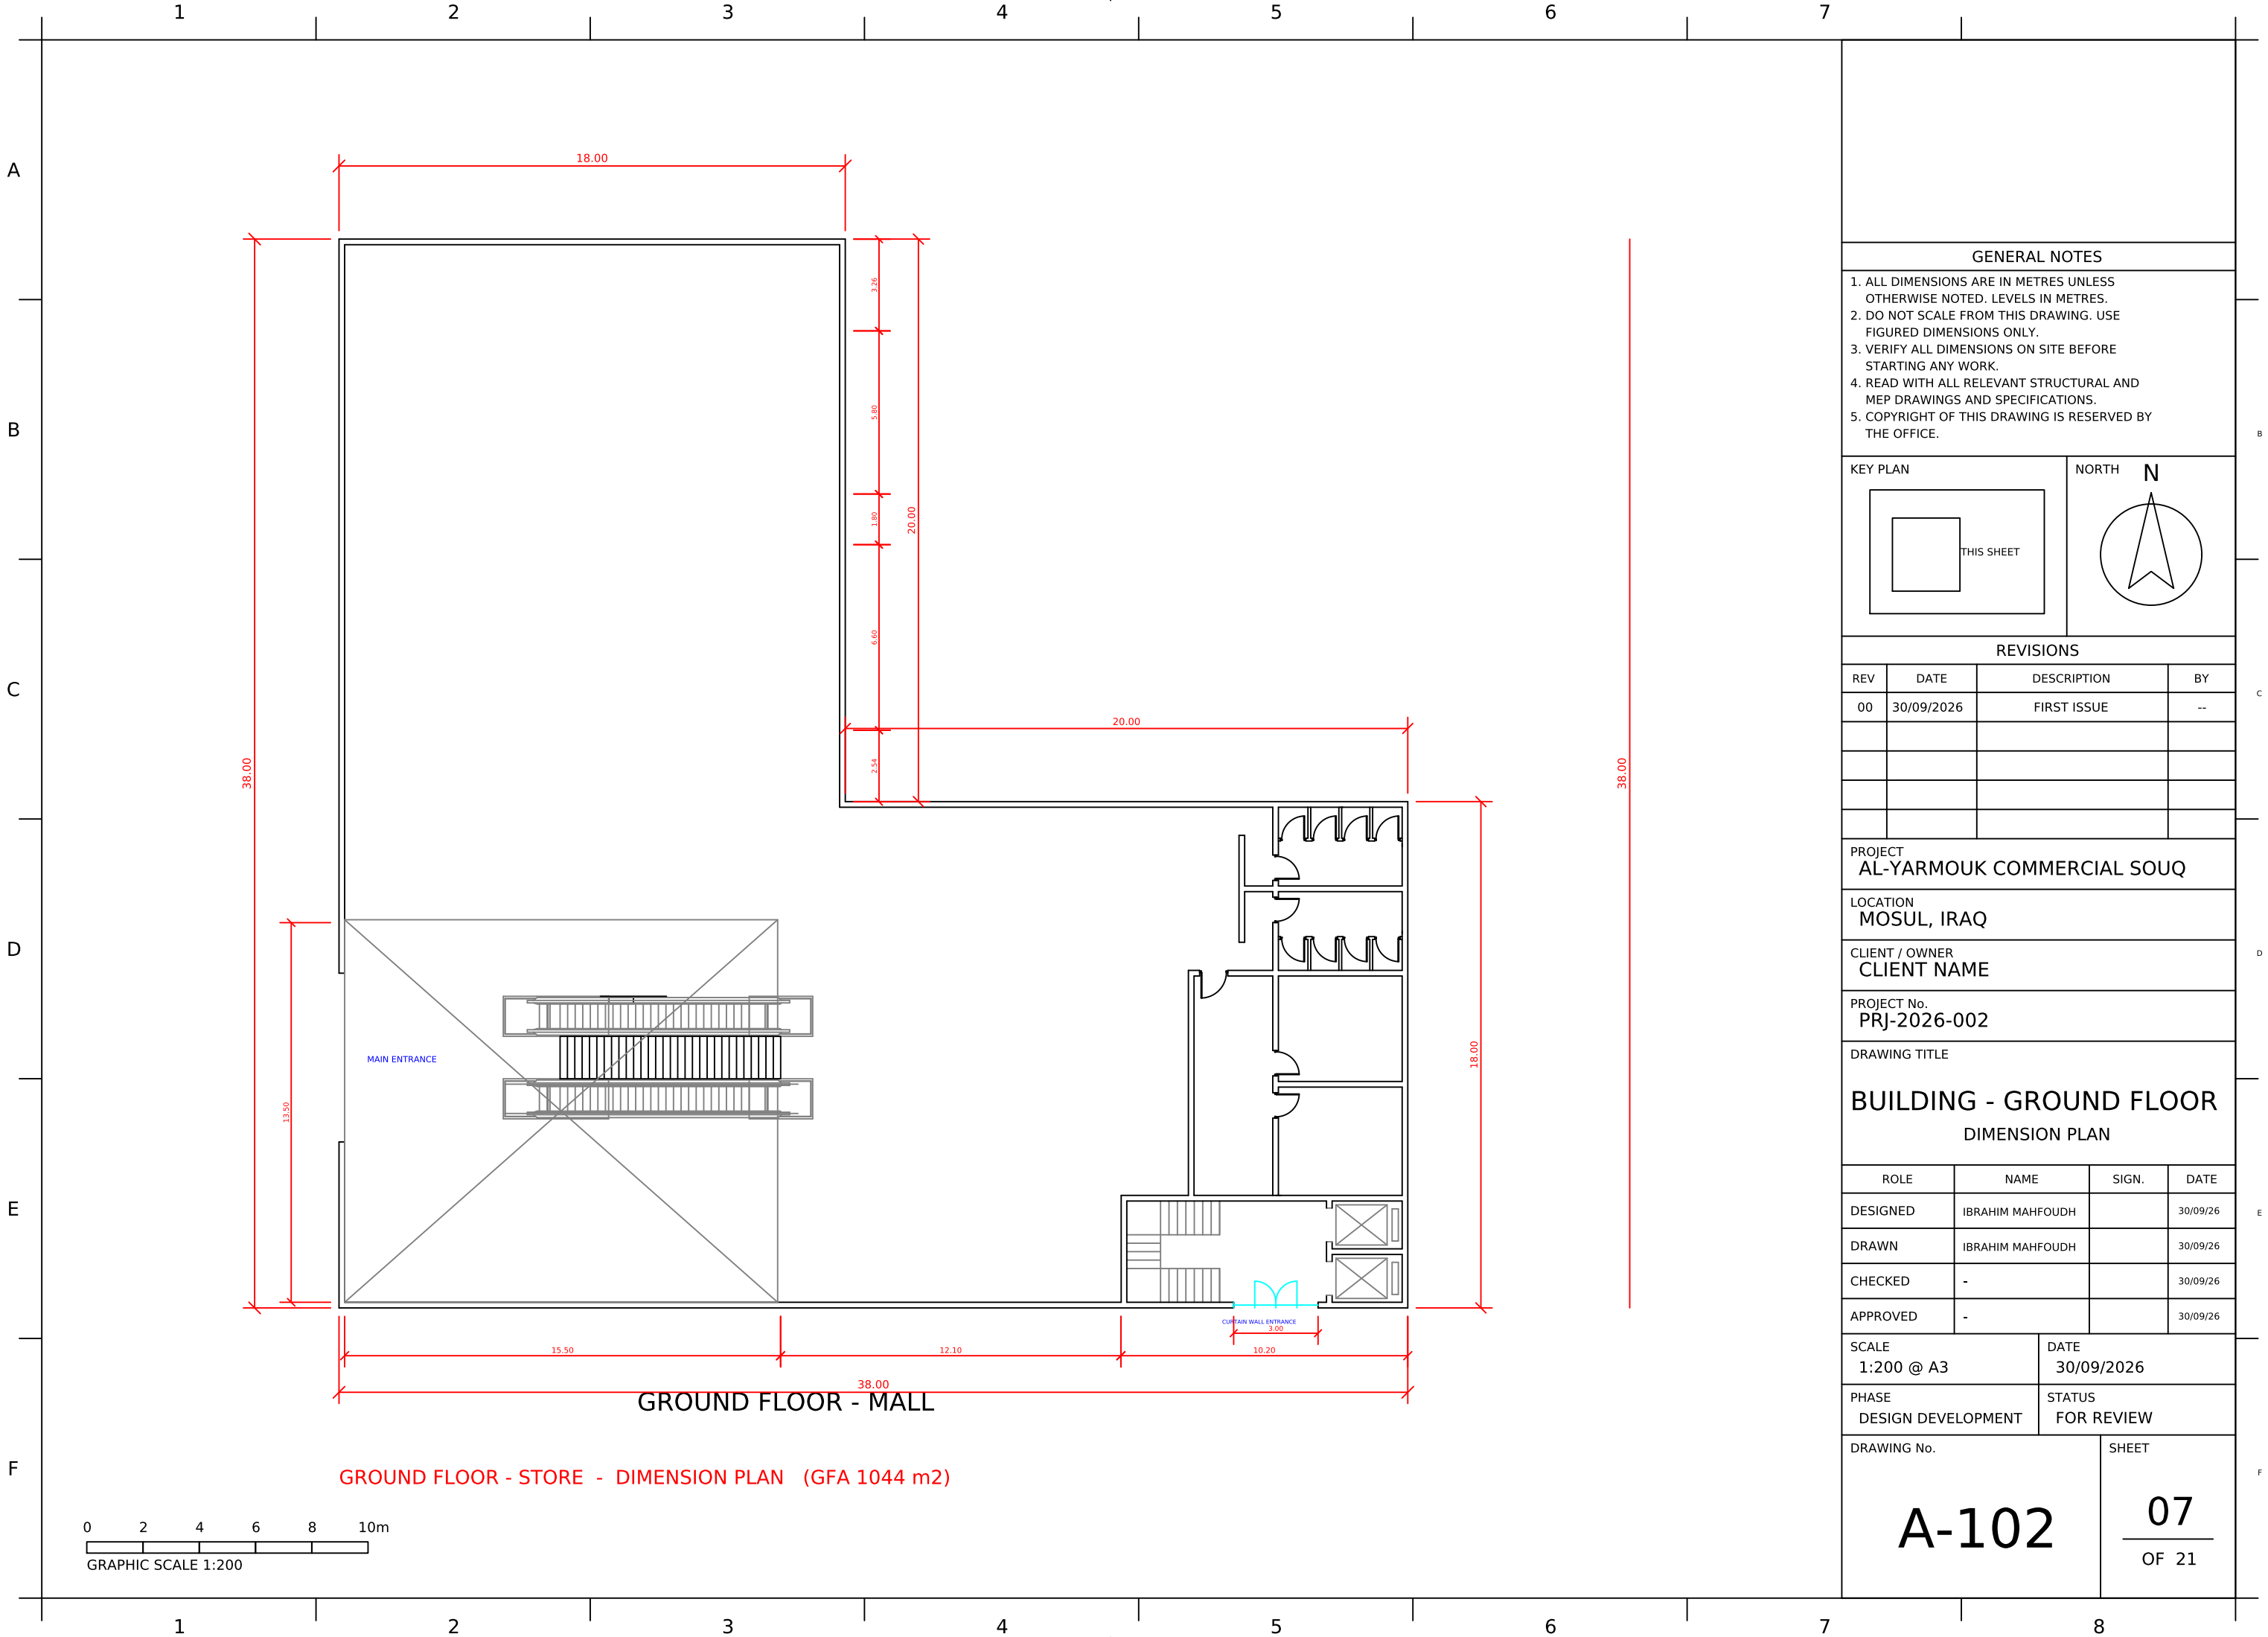

GENERAL NOTES

1. ALL DIMENSIONS ARE IN METRES UNLESS OTHERWISE NOTED. LEVELS IN METRES.
2. DO NOT SCALE FROM THIS DRAWING. USE FIGURED DIMENSIONS ONLY.
3. VERIFY ALL DIMENSIONS ON SITE BEFORE STARTING ANY WORK.
4. READ WITH ALL RELEVANT STRUCTURAL AND MEP DRAWINGS AND SPECIFICATIONS.
5. COPYRIGHT OF THIS DRAWING IS RESERVED BY THE OFFICE.

KEY PLAN

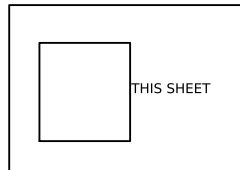

NORTH



REVISIONS

REV	DATE	DESCRIPTION	BY
00	30/09/2026	FIRST ISSUE	--

PROJECT
AL-YARMOUK COMMERCIAL SOUQ

LOCATION
MOSUL, IRAQ

CLIENT / OWNER
CLIENT NAME

PROJECT No.
PRJ-2026-002

DRAWING TITLE
BUILDING - GROUND FLOOR
DIMENSION PLAN

ROLE	NAME	SIGN.	DATE
DESIGNED	IBRAHIM MAHFOUDH		30/09/26
DRAWN	IBRAHIM MAHFOUDH		30/09/26
CHECKED	-		30/09/26
APPROVED	-		30/09/26

SCALE
1:200 @ A3

DATE
30/09/2026

PHASE
DESIGN DEVELOPMENT

STATUS
FOR REVIEW


DRAWING No.


A-102

SHEET

07

OF 21

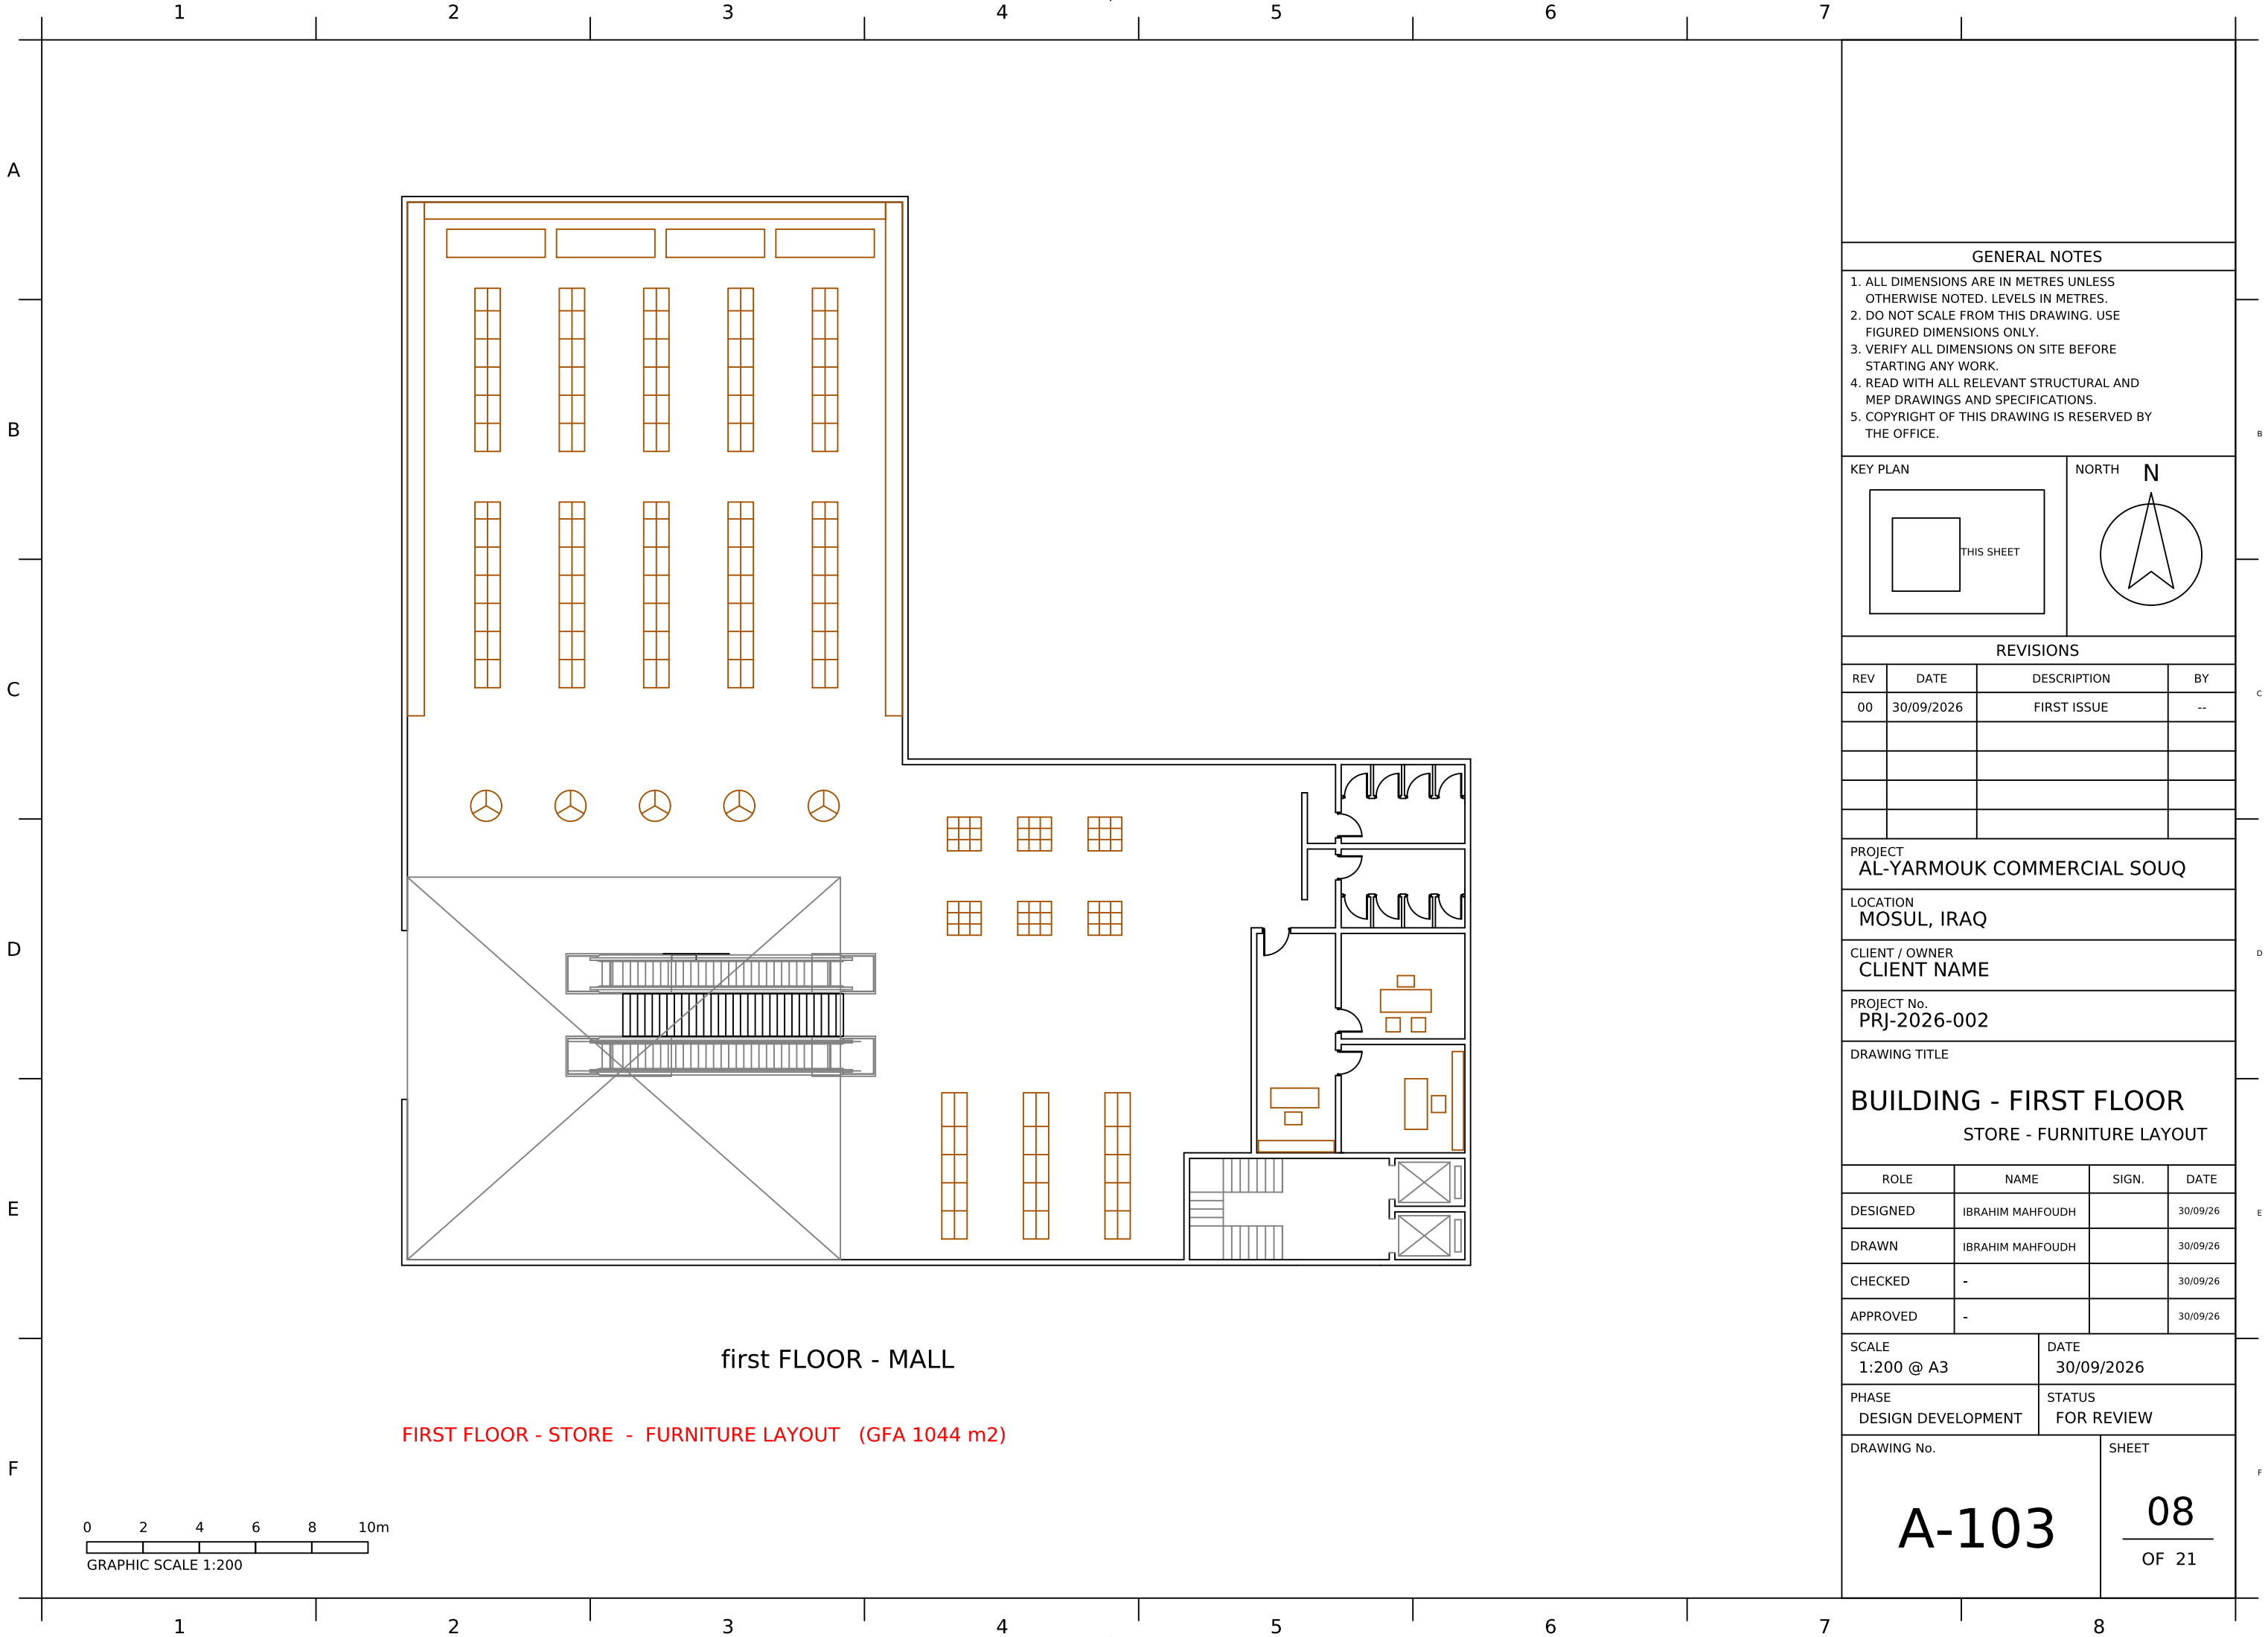


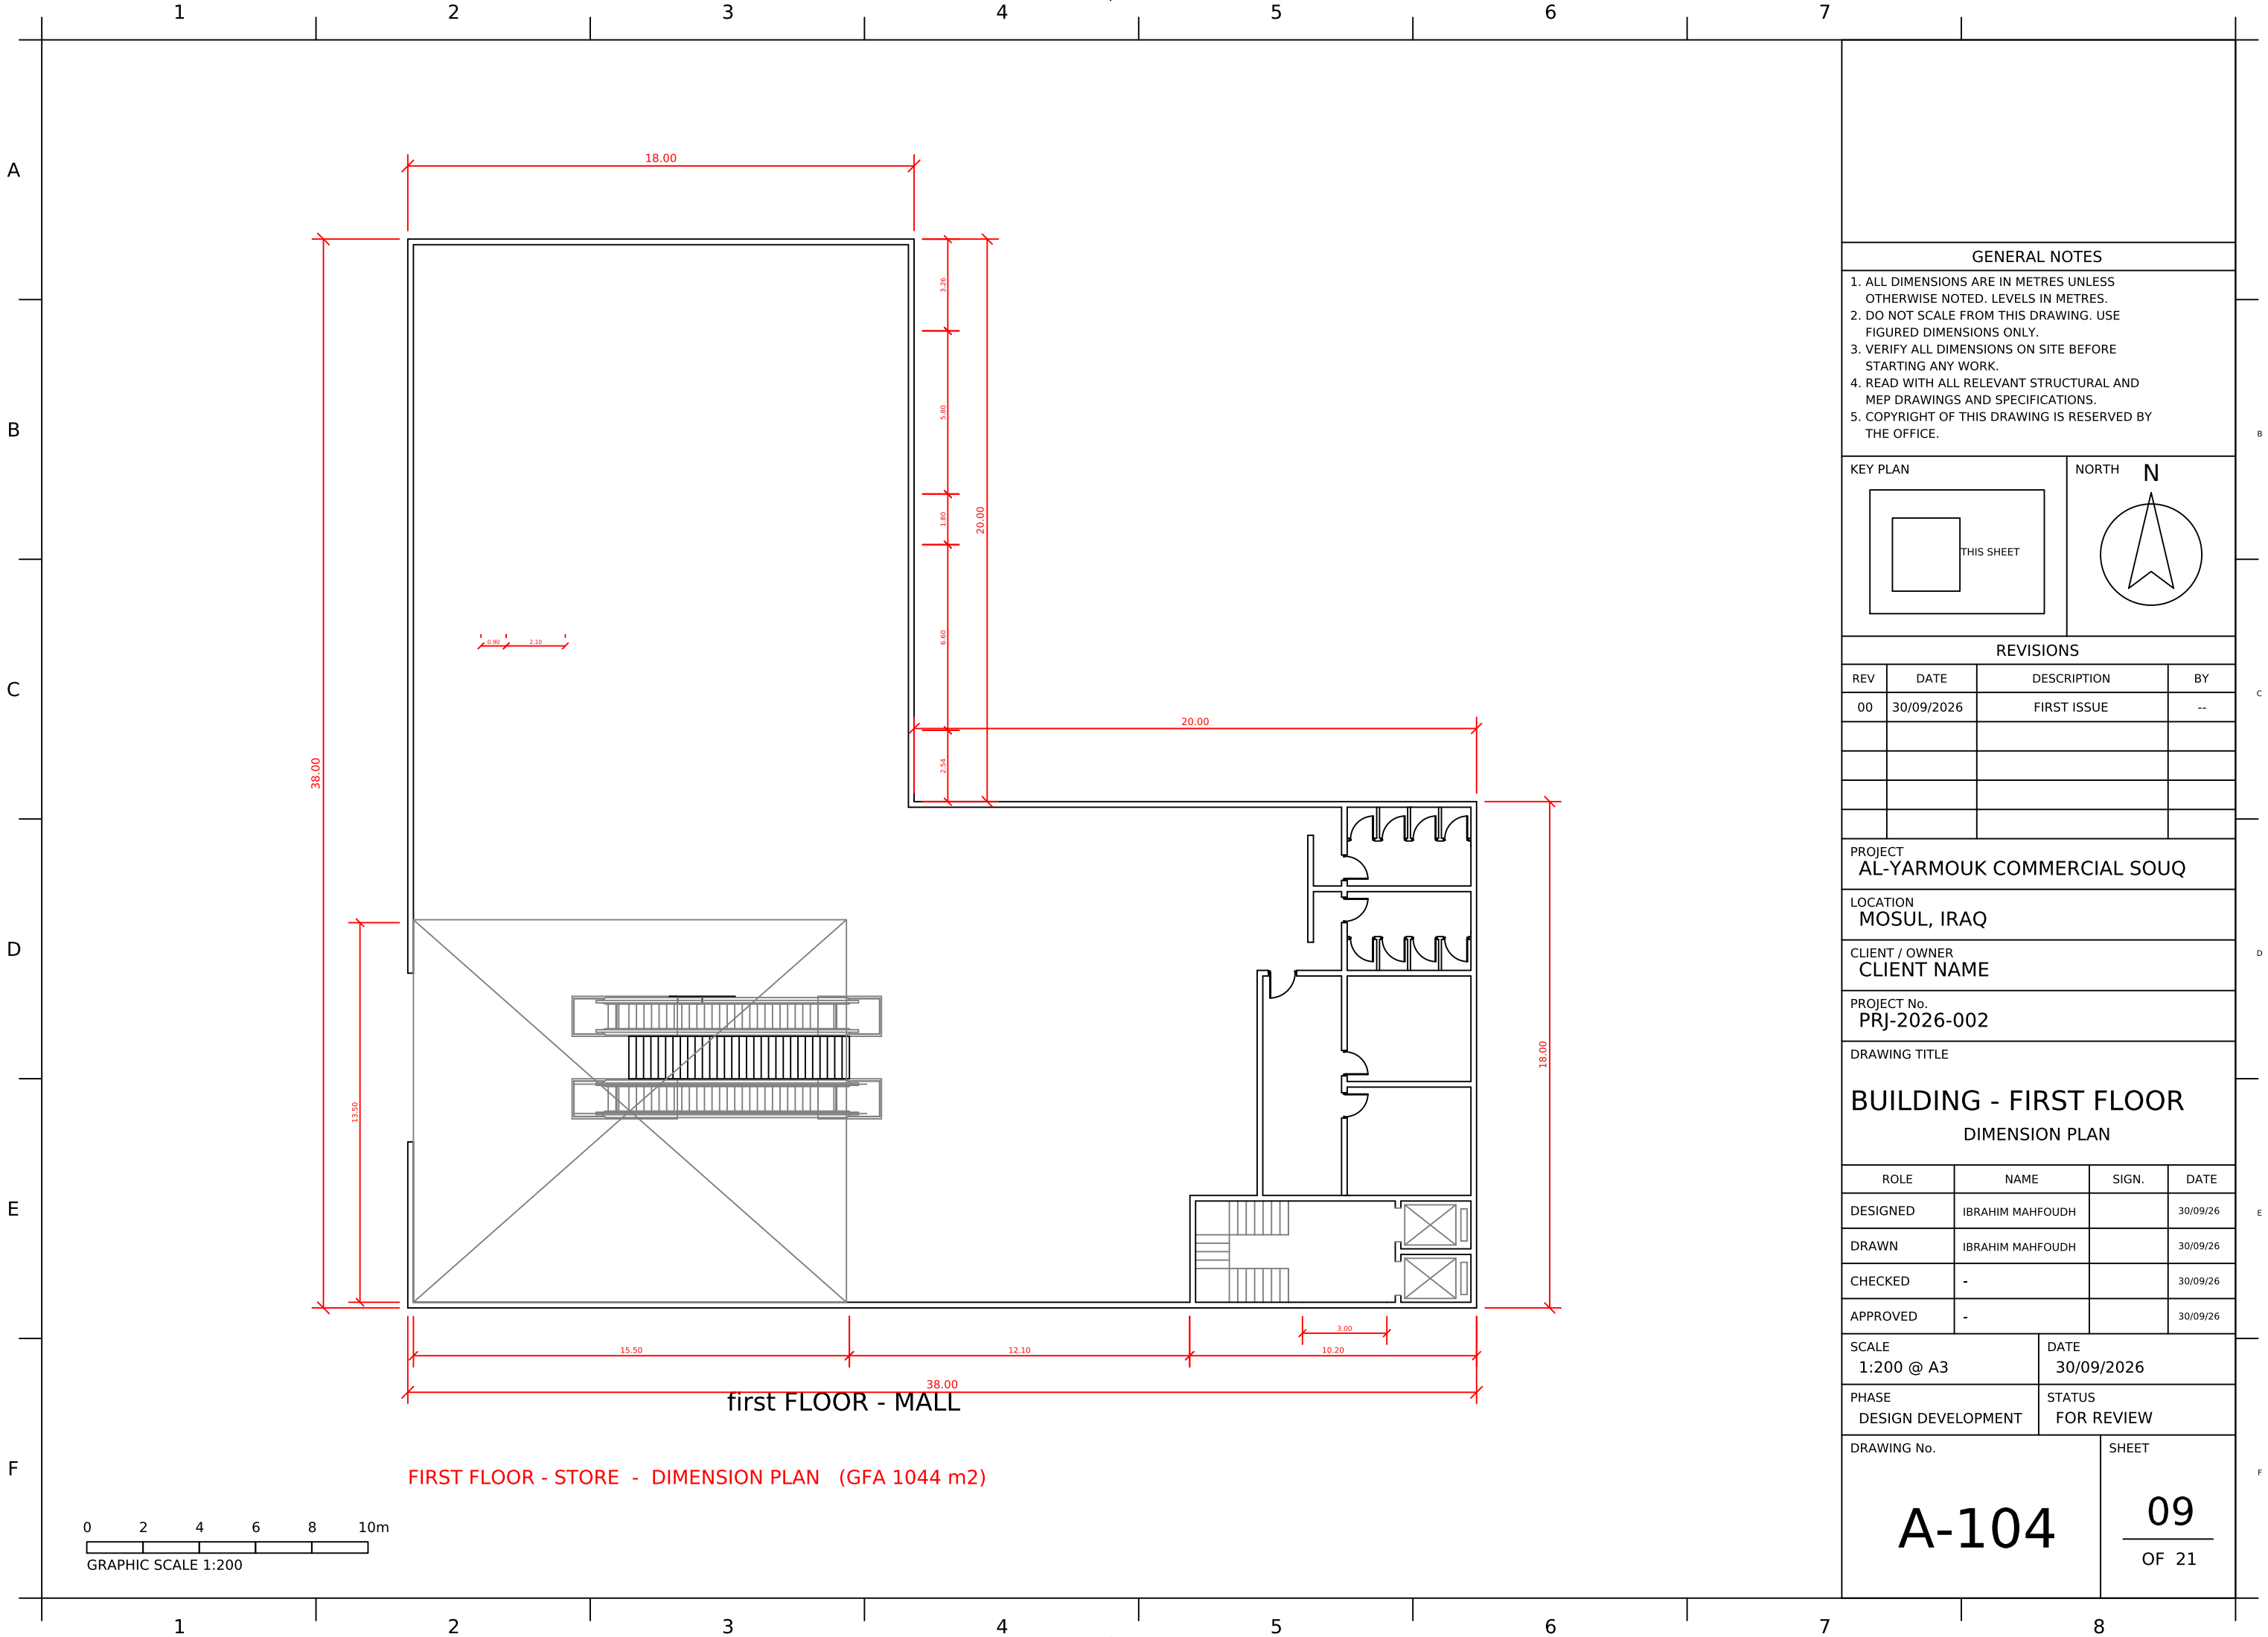

GENERAL NOTES

1. ALL DIMENSIONS ARE IN METRES UNLESS OTHERWISE NOTED. LEVELS IN METRES.
2. DO NOT SCALE FROM THIS DRAWING. USE FIGURED DIMENSIONS ONLY.
3. VERIFY ALL DIMENSIONS ON SITE BEFORE STARTING ANY WORK.
4. READ WITH ALL RELEVANT STRUCTURAL AND MEP DRAWINGS AND SPECIFICATIONS.
5. COPYRIGHT OF THIS DRAWING IS RESERVED BY THE OFFICE.

KEY PLAN

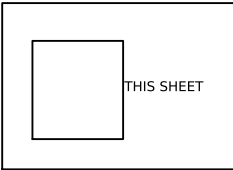

NORTH

N



REVISIONS

REV	DATE	DESCRIPTION	BY
00	30/09/2026	FIRST ISSUE	--

PROJECT
AL-YARMOUK COMMERCIAL SOUQ

LOCATION
MOSUL, IRAQ

CLIENT / OWNER
CLIENT NAME

PROJECT No.
PRJ-2026-002

DRAWING TITLE

BUILDING - FIRST FLOOR
DIMENSION PLAN

ROLE	NAME	SIGN.	DATE
DESIGNED	IBRAHIM MAHFOUDH		30/09/26
DRAWN	IBRAHIM MAHFOUDH		30/09/26
CHECKED	-		30/09/26
APPROVED	-		30/09/26

SCALE
1:200 @ A3

DATE
30/09/2026

PHASE
DESIGN DEVELOPMENT

STATUS
FOR REVIEW

DRAWING No.

A-104

SHEET

09
OF 21



- GENERAL NOTES
1. ALL DIMENSIONS ARE IN METRES UNLESS OTHERWISE NOTED. LEVELS IN METRES.

2. DO NOT SCALE FROM THIS DRAWING. USE FIGURED DIMENSIONS ONLY.

3. VERIFY ALL DIMENSIONS ON SITE BEFORE STARTING ANY WORK.

4. READ WITH ALL RELEVANT STRUCTURAL AND MEP DRAWINGS AND SPECIFICATIONS.

5. COPYRIGHT OF THIS DRAWING IS RESERVED BY THE OFFICE.

KEY PLAN

THIS SHEET

NORTH

N

REVISIONS			
REV	DATE	DESCRIPTION	BY
00	30/09/2026	FIRST ISSUE	--

PROJECT

AL-YARMOUK COMMERCIAL SOUQ

LOCATION

MOSUL, IRAQ

CLIENT / OWNER

CLIENT NAME

PROJECT No.

PRJ-2026-002

DRAWING TITLE

BUILDING - TYPICAL FLOOR

OFFICE APARTMENTS - FURNITURE

ROLE	NAME	SIGN.	DATE
DESIGNED	IBRAHIM MAHFOUDH		30/09/26
DRAWN	IBRAHIM MAHFOUDH		30/09/26
CHECKED	-		30/09/26
APPROVED	-		30/09/26

SCALE

1:200 @ A3

DATE

30/09/2026

PHASE

DESIGN DEVELOPMENT

STATUS

FOR REVIEW


DRAWING No.

A-105

SHEET

10

OF 21

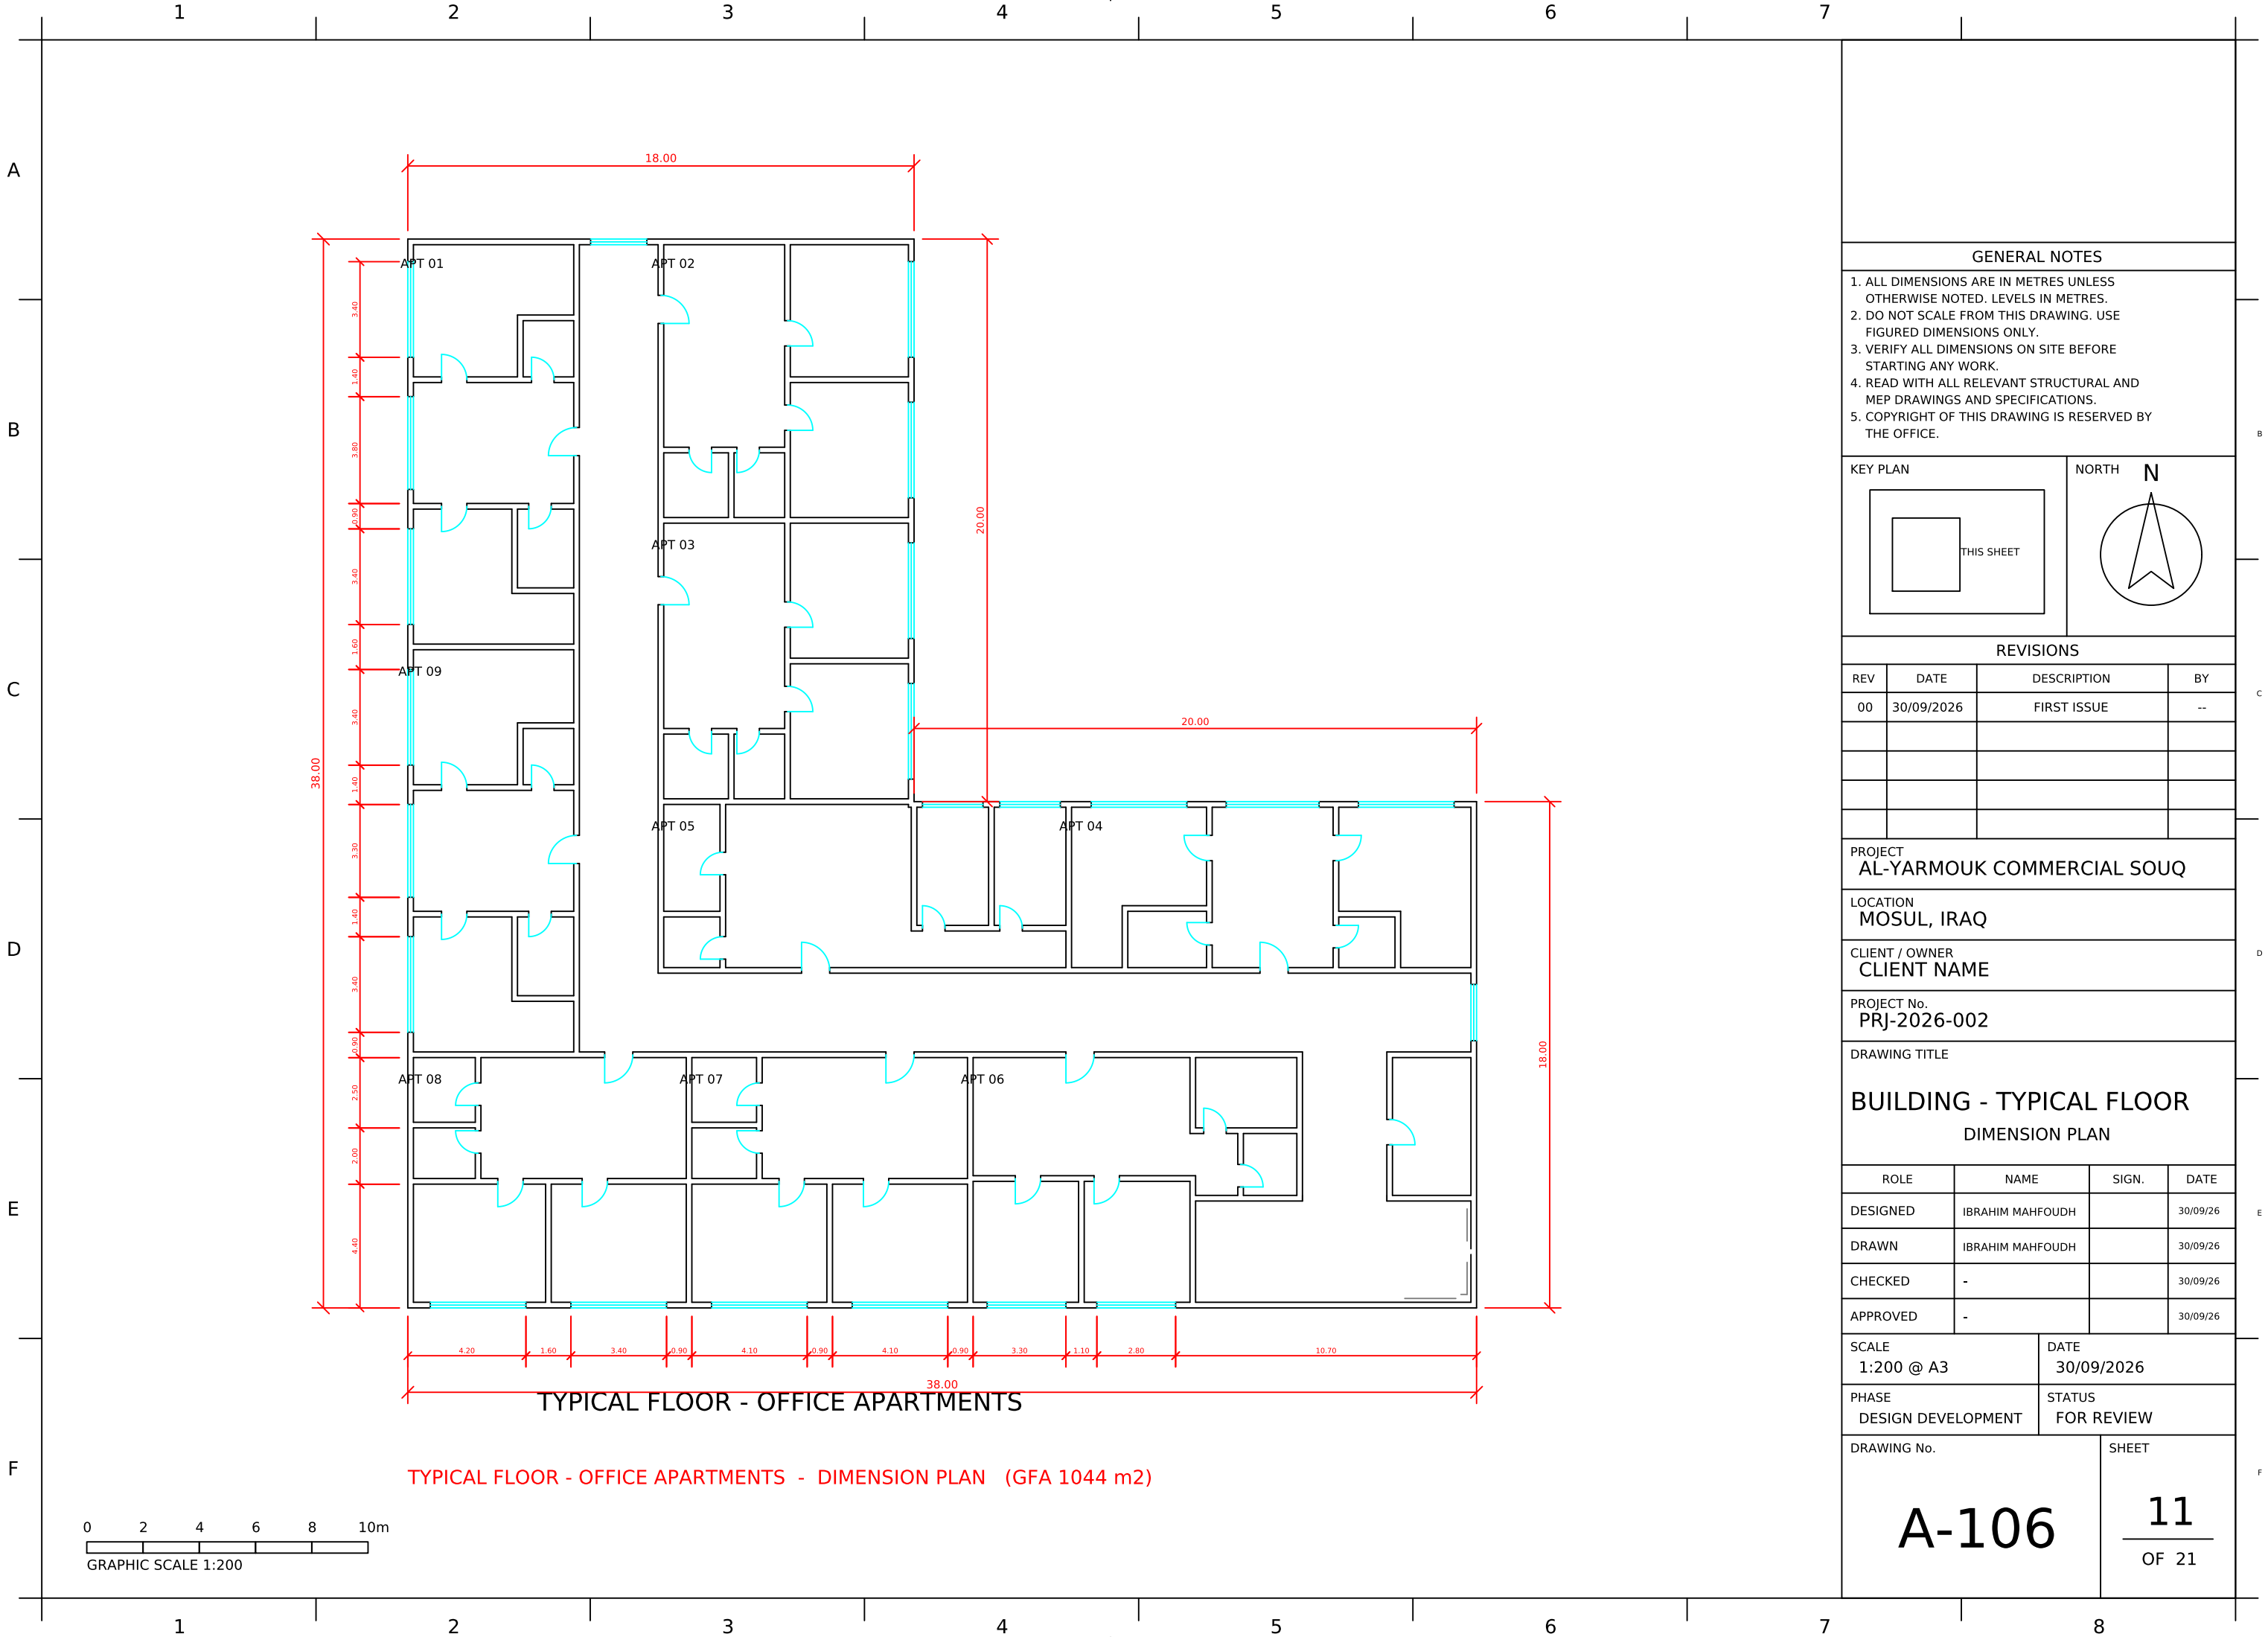

- GENERAL NOTES
1. ALL DIMENSIONS ARE IN METRES UNLESS OTHERWISE NOTED. LEVELS IN METRES.
 2. DO NOT SCALE FROM THIS DRAWING. USE FIGURED DIMENSIONS ONLY.
 3. VERIFY ALL DIMENSIONS ON SITE BEFORE STARTING ANY WORK.
 4. READ WITH ALL RELEVANT STRUCTURAL AND MEP DRAWINGS AND SPECIFICATIONS.
 5. COPYRIGHT OF THIS DRAWING IS RESERVED BY THE OFFICE.

KEY PLAN

NORTH

REVISIONS			
REV	DATE	DESCRIPTION	BY
00	30/09/2026	FIRST ISSUE	--

PROJECT
AL-YARMOUK COMMERCIAL SOUQ

LOCATION
MOSUL, IRAQ

CLIENT / OWNER
CLIENT NAME

PROJECT No.
PRJ-2026-002

DRAWING TITLE

BUILDING - TYPICAL FLOOR
DIMENSION PLAN

ROLE	NAME	SIGN.	DATE
DESIGNED	IBRAHIM MAHFOUDH		30/09/26
DRAWN	IBRAHIM MAHFOUDH		30/09/26
CHECKED	-		30/09/26
APPROVED	-		30/09/26

SCALE 1:200 @ A3	DATE 30/09/2026
---------------------	--------------------

PHASE DESIGN DEVELOPMENT	STATUS FOR REVIEW
-----------------------------	----------------------


DRAWING No.

A-106


SHEET

11
OF 21


SHOP MODEL 2 - EXTERIOR SHOP - PLANS (GF / UPPER / ROOF)

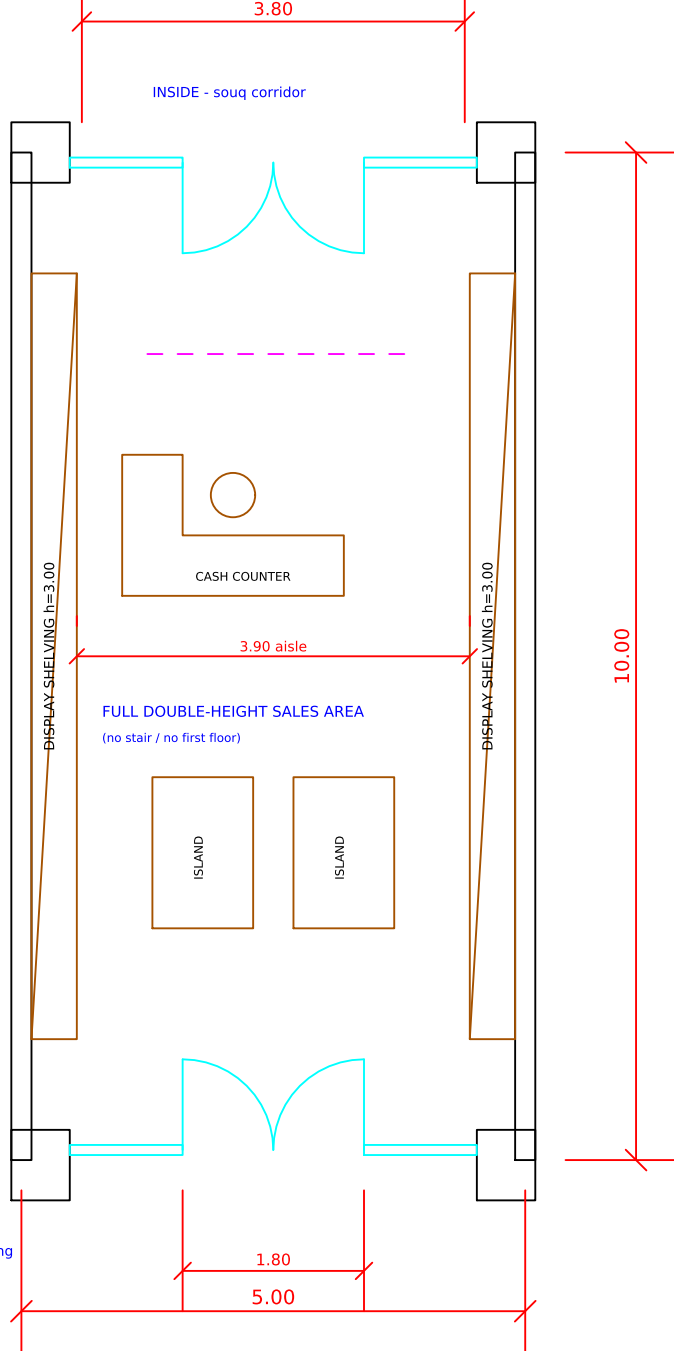


GROUND FLOOR PLAN (48 m2)

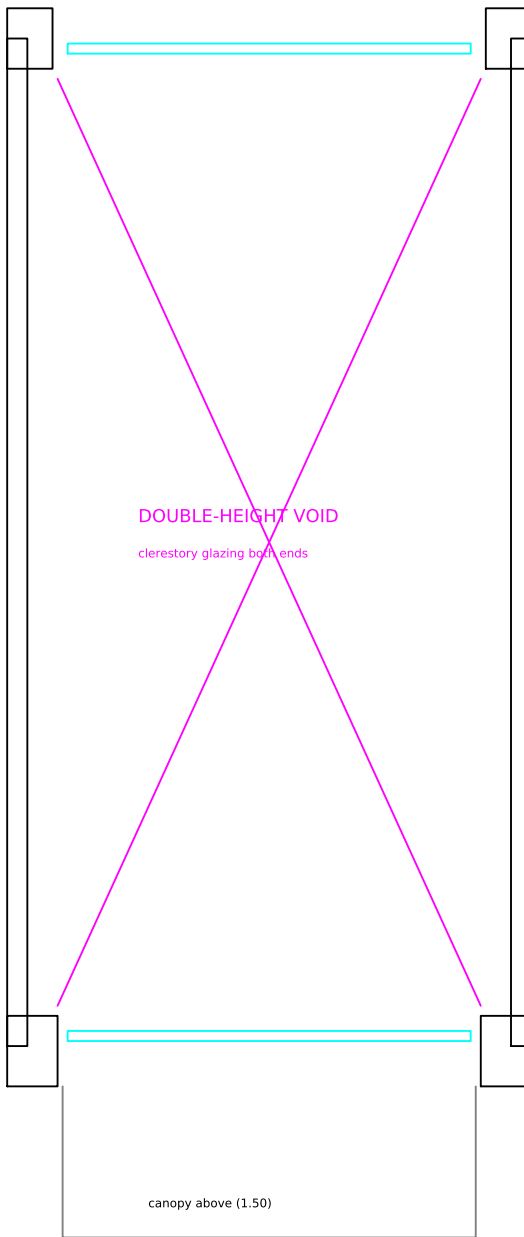

UPPER LEVEL (cut +4.50)

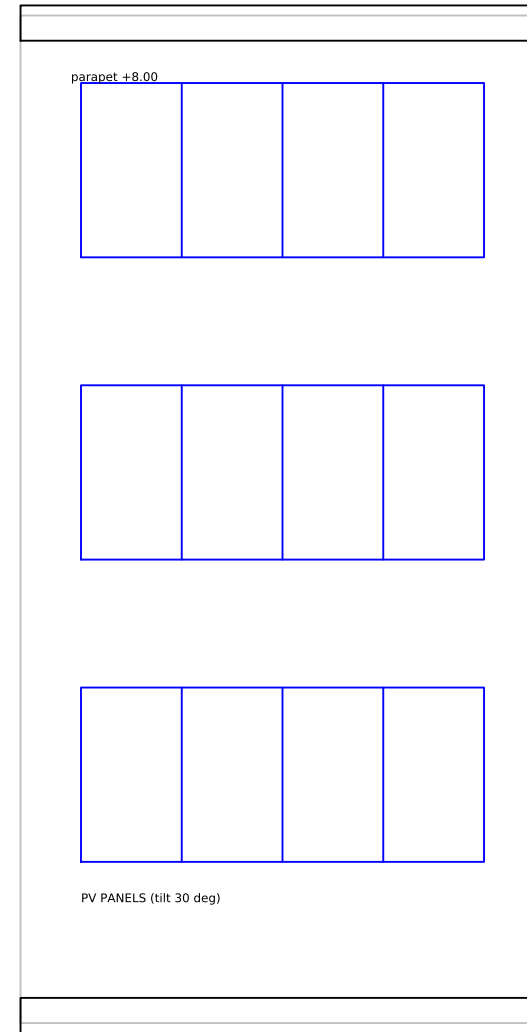


ROOF PLAN (+6.40)

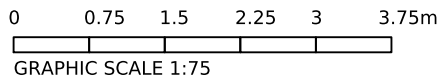

GENERAL NOTES

1. ALL DIMENSIONS ARE IN METRES UNLESS OTHERWISE NOTED. LEVELS IN METRES.
2. DO NOT SCALE FROM THIS DRAWING. USE FIGURED DIMENSIONS ONLY.
3. VERIFY ALL DIMENSIONS ON SITE BEFORE STARTING ANY WORK.
4. READ WITH ALL RELEVANT STRUCTURAL AND MEP DRAWINGS AND SPECIFICATIONS.
5. COPYRIGHT OF THIS DRAWING IS RESERVED BY THE OFFICE.

KEY PLAN

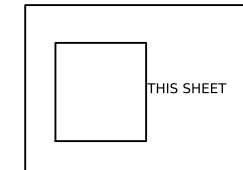

NORTH



REVISIONS

REV	DATE	DESCRIPTION	BY
00	30/09/2026	FIRST ISSUE	--

PROJECT
AL-YARMOUK COMMERCIAL SOUQ

LOCATION
MOSUL, IRAQ

CLIENT / OWNER
CLIENT NAME

PROJECT No.
PRJ-2026-002

DRAWING TITLE
SHOP MODEL - EXTERIOR
PLANS

ROLE	NAME	SIGN.	DATE
DESIGNED	IBRAHIM MAHFOUDH		30/09/26
DRAWN	IBRAHIM MAHFOUDH		30/09/26
CHECKED	-		30/09/26
APPROVED	-		30/09/26

SCALE
1:75 @ A3

DATE
30/09/2026

PHASE
DESIGN DEVELOPMENT


STATUS
FOR REVIEW

DRAWING No.

A-201

SHEET

12
OF 21

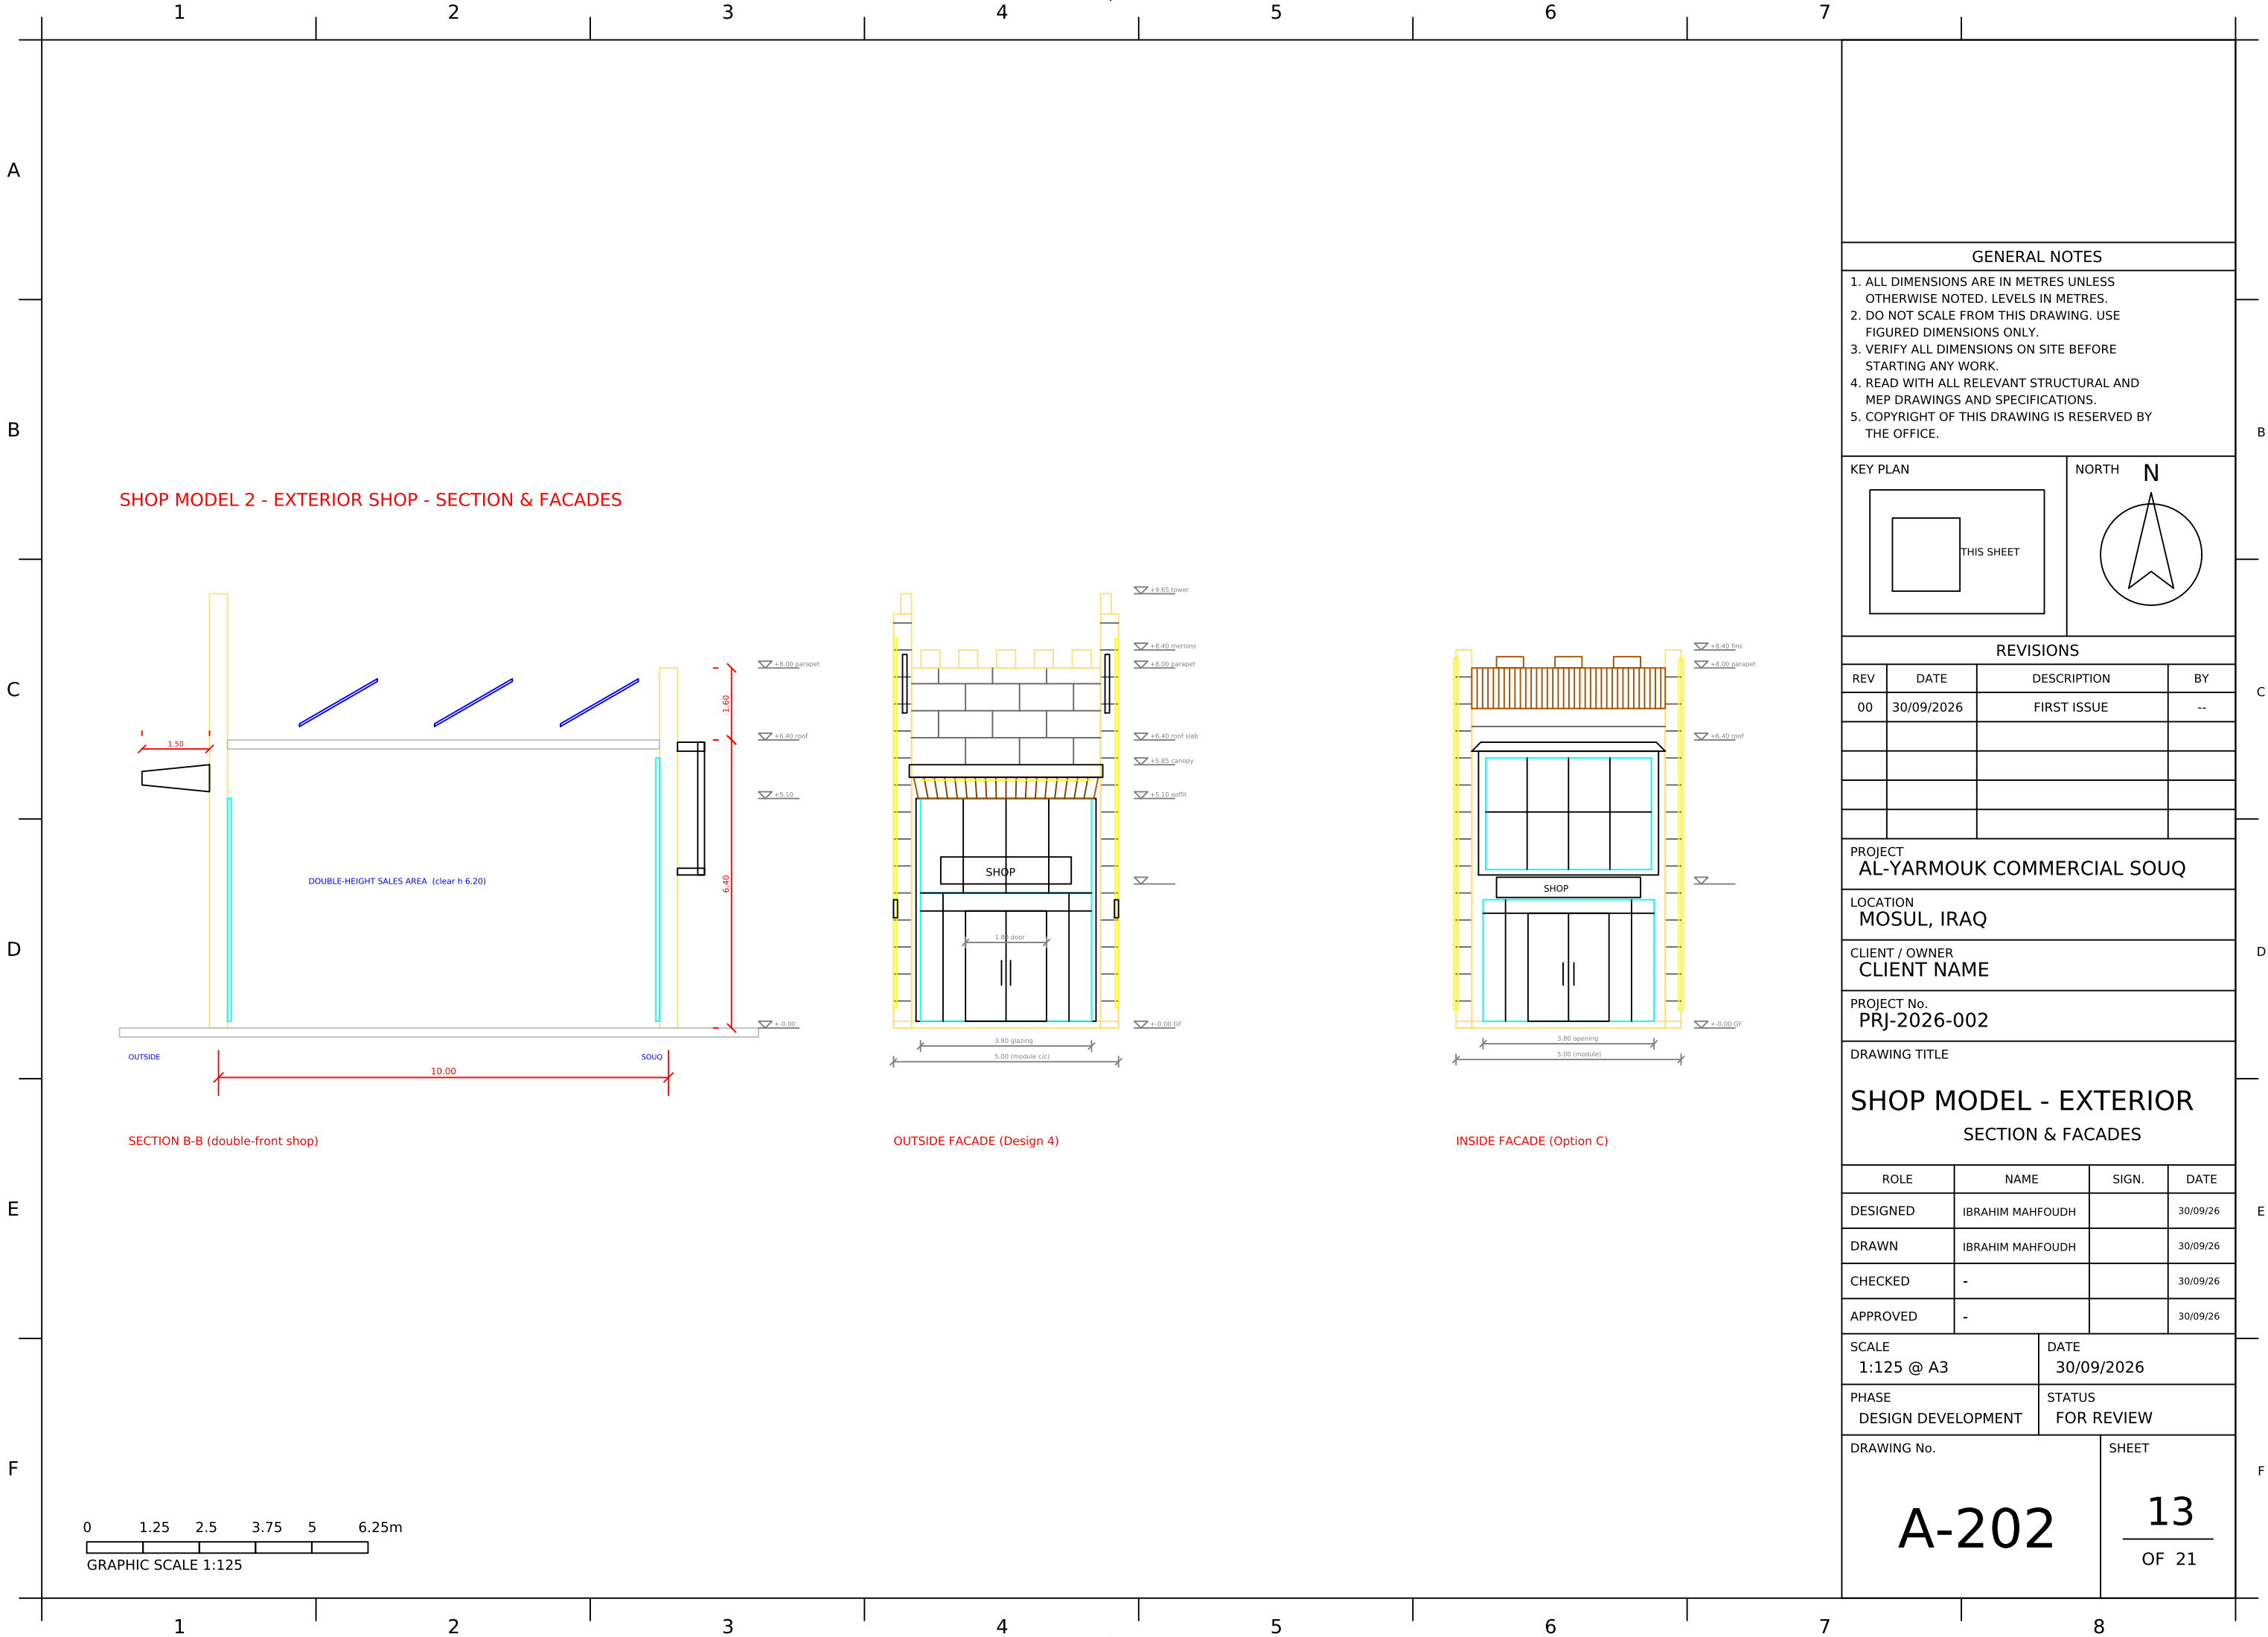

- GENERAL NOTES
1. ALL DIMENSIONS ARE IN METRES UNLESS OTHERWISE NOTED. LEVELS IN METRES.
 2. DO NOT SCALE FROM THIS DRAWING. USE FIGURED DIMENSIONS ONLY.
 3. VERIFY ALL DIMENSIONS ON SITE BEFORE STARTING ANY WORK.
 4. READ WITH ALL RELEVANT STRUCTURAL AND MEP DRAWINGS AND SPECIFICATIONS.
 5. COPYRIGHT OF THIS DRAWING IS RESERVED BY THE OFFICE.

KEY PLAN

NORTH

REVISIONS			
REV	DATE	DESCRIPTION	BY
00	30/09/2026	FIRST ISSUE	--

PROJECT
AL-YARMOUK COMMERCIAL SOUQ

LOCATION
MOSUL, IRAQ

CLIENT / OWNER
CLIENT NAME

PROJECT No.
PRJ-2026-002

DRAWING TITLE

SHOP MODEL - EXTERIOR
SECTION & FACADES

ROLE	NAME	SIGN.	DATE
DESIGNED	IBRAHIM MAHFOUDH		30/09/26
DRAWN	IBRAHIM MAHFOUDH		30/09/26
CHECKED	-		30/09/26
APPROVED	-		30/09/26

SCALE 1:125 @ A3	DATE 30/09/2026
---------------------	--------------------

PHASE DESIGN DEVELOPMENT	STATUS FOR REVIEW
-----------------------------	----------------------

DRAWING No.

A-202

SHEET


13
OF 21

The floor plan shows a rectangular store layout with the following features and dimensions:



- Overall Dimensions:** 5.00m wide by 10.00m deep.
- Entrance:** A double-height entrance at the bottom center, 3.80m wide, with a 1.80m wide side area on each side.
- Staircase:** Located on the right side, 2.20m wide, with an "UP" arrow indicating the direction.
- Display Shelving:** Along the left wall, with a height of 2.40m.
- Sales Area:** A central area with a height of 3.00m.
- Mannequin:** A rectangular area for a mannequin, 1.80m wide and 1.20m high.
- Display Table:** A rectangular table, 1.80m wide and 1.20m high, positioned in the center.
- Cash Counter:** An L-shaped counter, 1.80m wide and 1.20m high, positioned in the top right corner.
- Clearance:** A 4.80m clear width is indicated at the top.

The layout is designed to maximize the use of space, with a central sales area and a double-height entrance for a modern, open feel.


GROUND FLOOR PLAN (+-0.00, 48 m2)

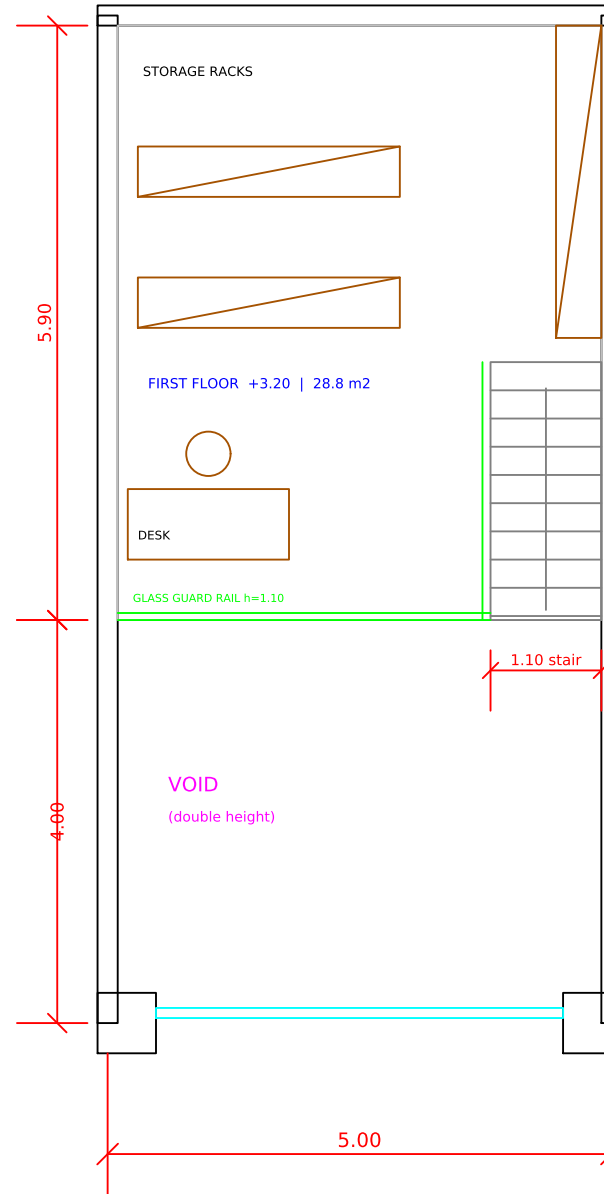


FIRST FLOOR PLAN (+3.20, 28.8 m2)

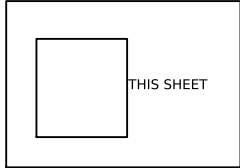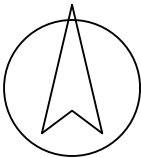GENERAL NOTES			
1. ALL DIMENSIONS ARE IN METRES UNLESS OTHERWISE NOTED. LEVELS IN METRES. 2. DO NOT SCALE FROM THIS DRAWING. USE FIGURED DIMENSIONS ONLY. 3. VERIFY ALL DIMENSIONS ON SITE BEFORE STARTING ANY WORK. 4. READ WITH ALL RELEVANT STRUCTURAL AND MEP DRAWINGS AND SPECIFICATIONS. 5. COPYRIGHT OF THIS DRAWING IS RESERVED BY THE OFFICE.			
KEY PLAN		NORTH	
			
REVISIONS			
REV	DATE	DESCRIPTION	BY
00	30/09/2026	FIRST ISSUE	--
PROJECT AL-YARMOUK COMMERCIAL SOUQ			
LOCATION MOSUL, IRAQ			
CLIENT / OWNER CLIENT NAME			
PROJECT No. PRJ-2026-002			
DRAWING TITLE SHOP MODEL - INTERIOR PLANS			
ROLE	NAME	SIGN.	DATE
DESIGNED	IBRAHIM MAHFOUDH		30/09/26
DRAWN	IBRAHIM MAHFOUDH		30/09/26
CHECKED	-		30/09/26
APPROVED	-		30/09/26
SCALE 1:75 @ A3		DATE 30/09/2026	
PHASE DESIGN DEVELOPMENT		STATUS FOR REVIEW	
DRAWING No.			SHEET
A-203			14 OF 21

SHOP MODEL 1 - INTERIOR SHOP - SECTION & FACADE

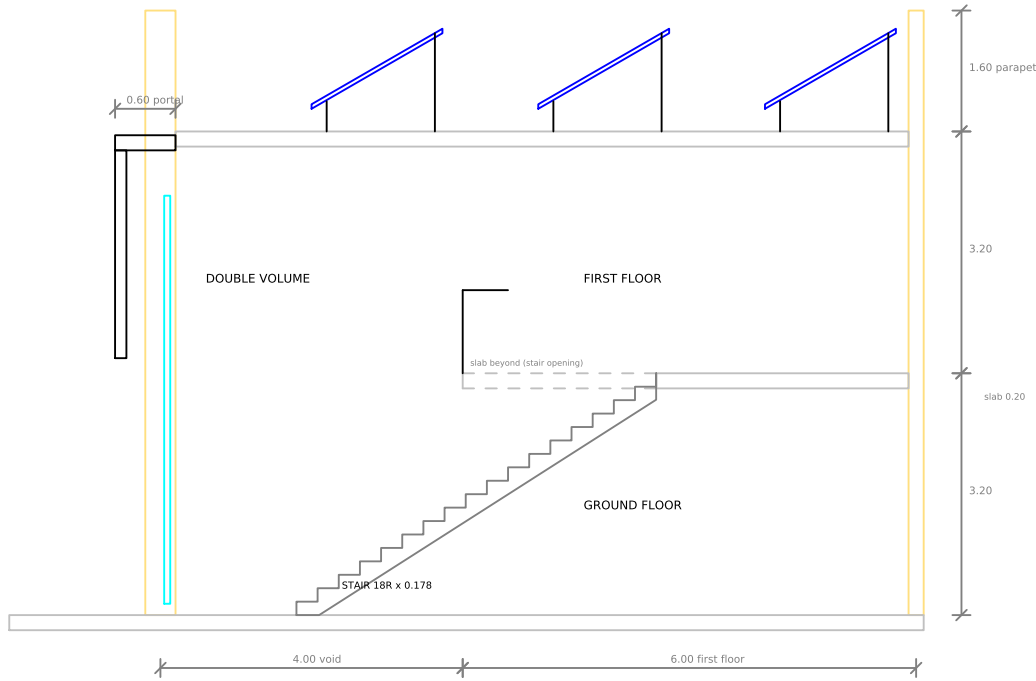

SECTION A-A (through stair)

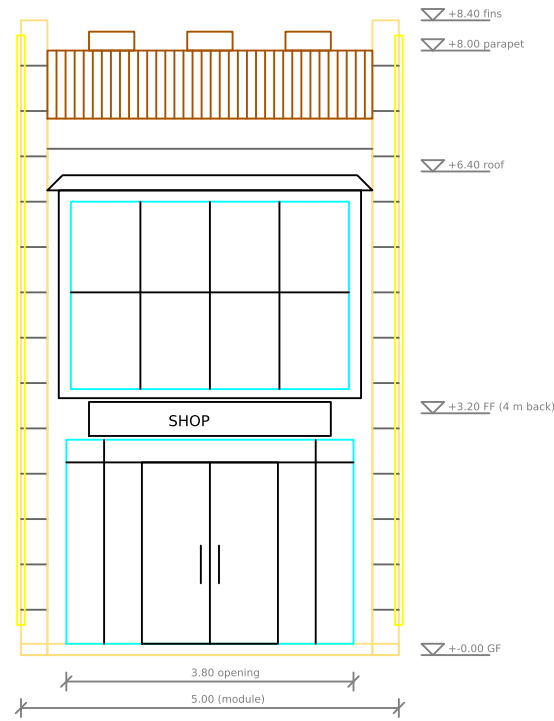


SHOP FRONT - INTERIOR FACADE (Option C)

GENERAL NOTES

1. ALL DIMENSIONS ARE IN METRES UNLESS OTHERWISE NOTED. LEVELS IN METRES.
2. DO NOT SCALE FROM THIS DRAWING. USE FIGURED DIMENSIONS ONLY.
3. VERIFY ALL DIMENSIONS ON SITE BEFORE STARTING ANY WORK.
4. READ WITH ALL RELEVANT STRUCTURAL AND MEP DRAWINGS AND SPECIFICATIONS.
5. COPYRIGHT OF THIS DRAWING IS RESERVED BY THE OFFICE.

KEY PLAN

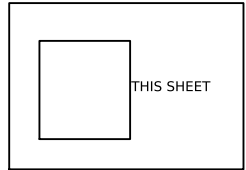

NORTH



REVISIONS

REV	DATE	DESCRIPTION	BY
00	30/09/2026	FIRST ISSUE	--

PROJECT
AL-YARMOUK COMMERCIAL SOUQ

LOCATION
MOSUL, IRAQ

CLIENT / OWNER
CLIENT NAME

PROJECT No.
PRJ-2026-002


DRAWING TITLE
SHOP MODEL - INTERIOR
SECTION & FACADE

ROLE	NAME	SIGN.	DATE
DESIGNED	IBRAHIM MAHFOUDH		30/09/26
DRAWN	IBRAHIM MAHFOUDH		30/09/26
CHECKED	-		30/09/26
APPROVED	-		30/09/26

SCALE 1:100 @ A3	DATE 30/09/2026
---------------------	--------------------

PHASE DESIGN DEVELOPMENT	STATUS FOR REVIEW
-----------------------------	----------------------

DRAWING No. A-204	SHEET 15 OF 21
-----------------------------	-----------------------------

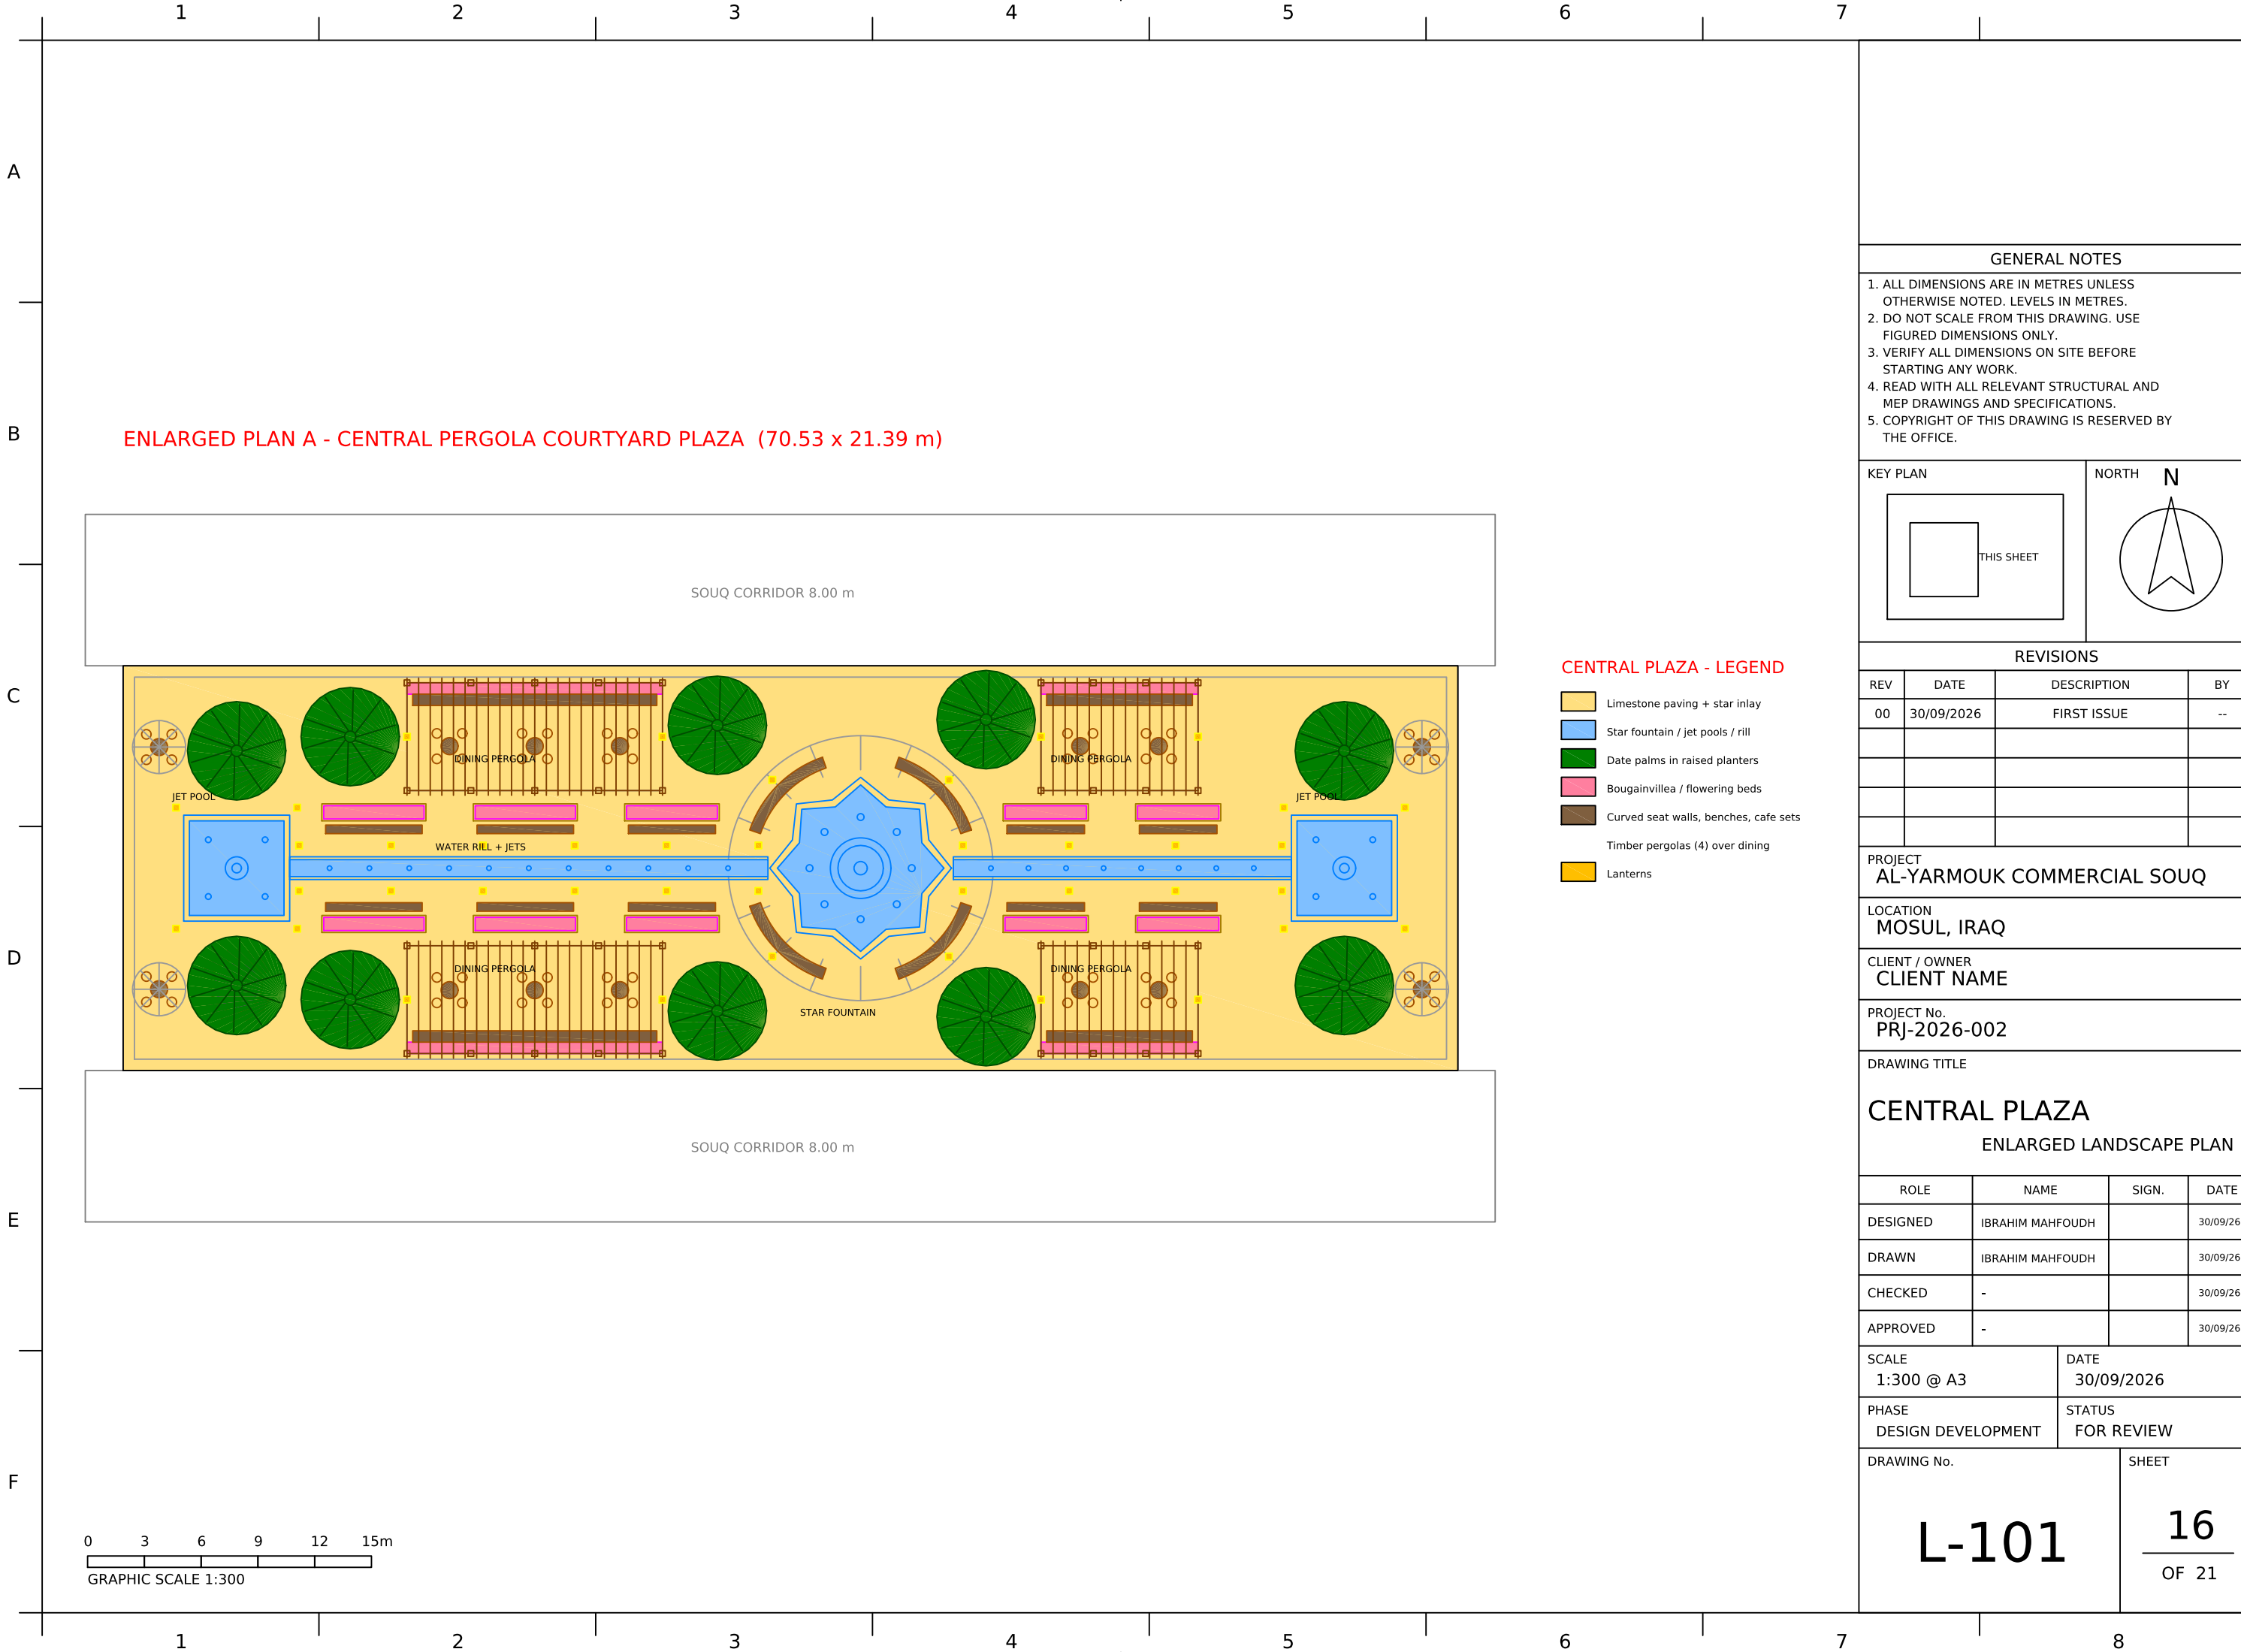

- GENERAL NOTES
1. ALL DIMENSIONS ARE IN METRES UNLESS OTHERWISE NOTED. LEVELS IN METRES.
 2. DO NOT SCALE FROM THIS DRAWING. USE FIGURED DIMENSIONS ONLY.
 3. VERIFY ALL DIMENSIONS ON SITE BEFORE STARTING ANY WORK.
 4. READ WITH ALL RELEVANT STRUCTURAL AND MEP DRAWINGS AND SPECIFICATIONS.
 5. COPYRIGHT OF THIS DRAWING IS RESERVED BY THE OFFICE.

KEY PLAN

THIS SHEET

NORTH
N

REVISIONS			
REV	DATE	DESCRIPTION	BY
00	30/09/2026	FIRST ISSUE	--

PROJECT
AL-YARMOUK COMMERCIAL SOUQ

LOCATION
MOSUL, IRAQ

CLIENT / OWNER
CLIENT NAME

PROJECT No.
PRJ-2026-002

DRAWING TITLE

CENTRAL PLAZA

ENLARGED LANDSCAPE PLAN

ROLE	NAME	SIGN.	DATE
DESIGNED	IBRAHIM MAHFOUDH		30/09/26
DRAWN	IBRAHIM MAHFOUDH		30/09/26
CHECKED	-		30/09/26
APPROVED	-		30/09/26

SCALE
1:300 @ A3

DATE
30/09/2026

PHASE
DESIGN DEVELOPMENT


STATUS
FOR REVIEW

DRAWING No.

L-101

SHEET

16
OF 21

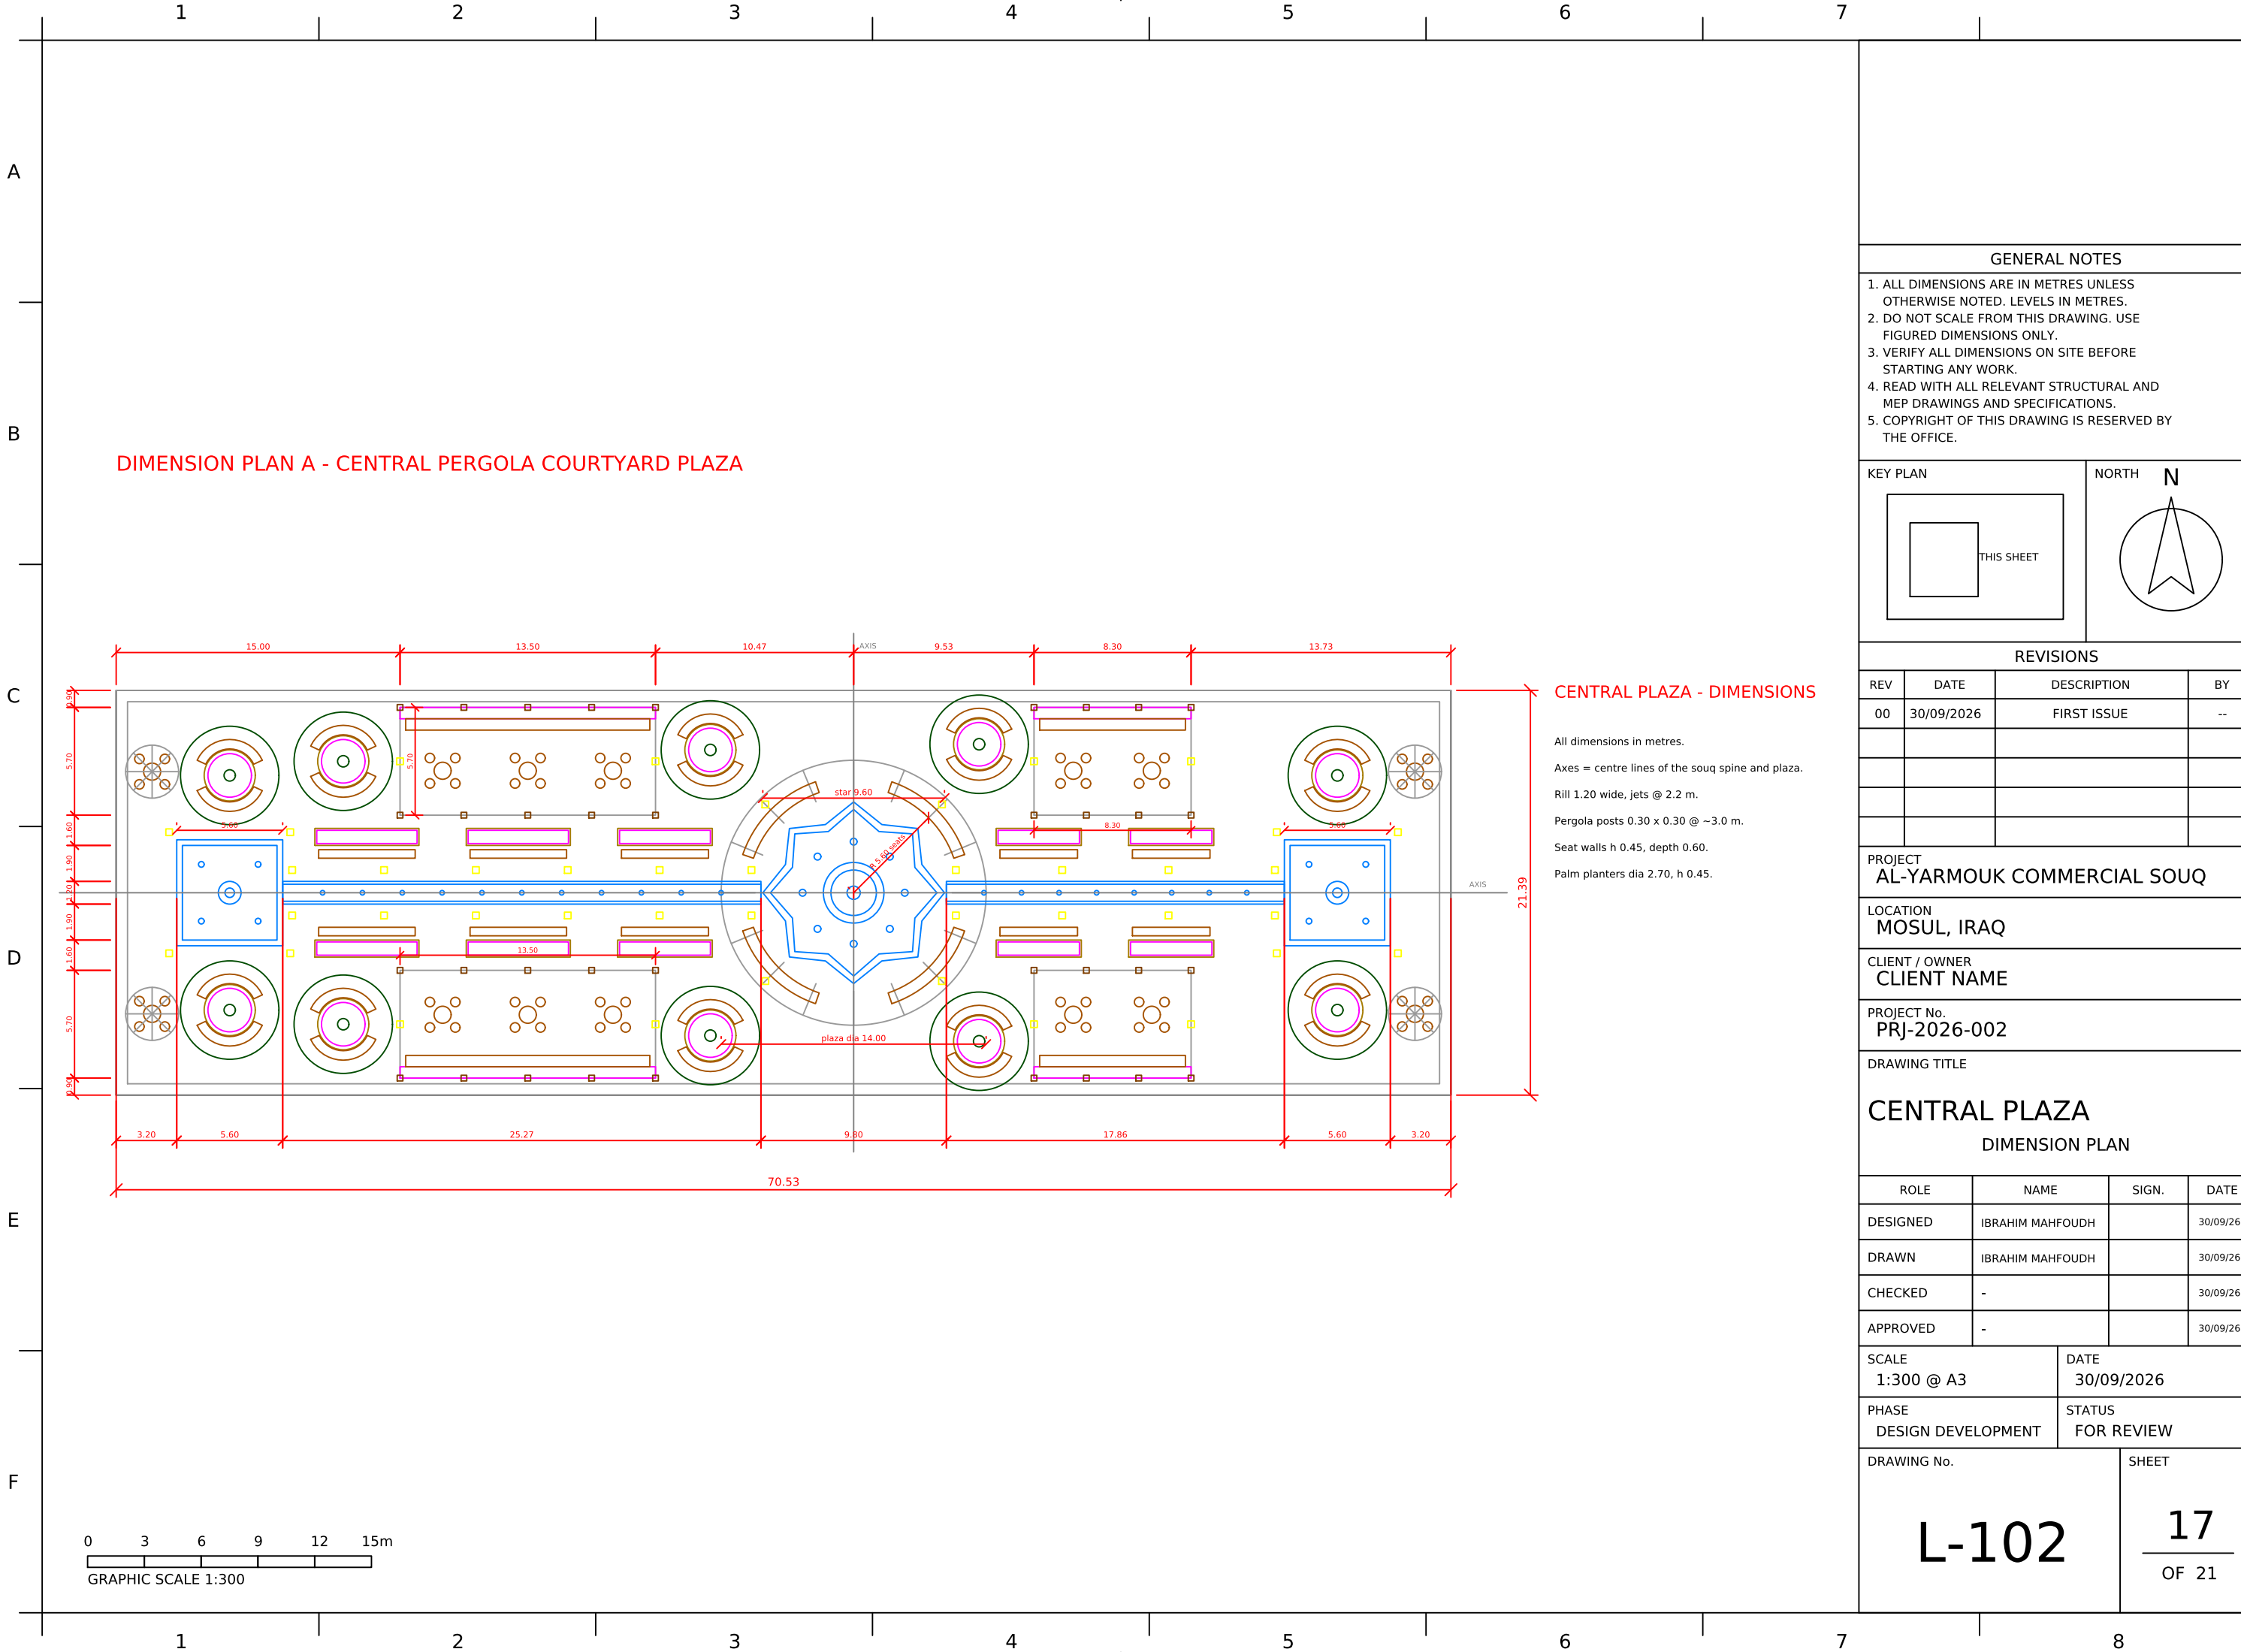

- GENERAL NOTES
1. ALL DIMENSIONS ARE IN METRES UNLESS OTHERWISE NOTED. LEVELS IN METRES.
 2. DO NOT SCALE FROM THIS DRAWING. USE FIGURED DIMENSIONS ONLY.
 3. VERIFY ALL DIMENSIONS ON SITE BEFORE STARTING ANY WORK.
 4. READ WITH ALL RELEVANT STRUCTURAL AND MEP DRAWINGS AND SPECIFICATIONS.
 5. COPYRIGHT OF THIS DRAWING IS RESERVED BY THE OFFICE.

KEY PLAN

NORTH

REVISIONS			
REV	DATE	DESCRIPTION	BY
00	30/09/2026	FIRST ISSUE	--

PROJECT
AL-YARMOUK COMMERCIAL SOUQ

LOCATION
MOSUL, IRAQ

CLIENT / OWNER
CLIENT NAME

PROJECT No.
PRJ-2026-002

DRAWING TITLE

CENTRAL PLAZA
DIMENSION PLAN

ROLE	NAME	SIGN.	DATE
DESIGNED	IBRAHIM MAHFOUDH		30/09/26
DRAWN	IBRAHIM MAHFOUDH		30/09/26
CHECKED	-		30/09/26
APPROVED	-		30/09/26

SCALE
1:300 @ A3

DATE
30/09/2026

PHASE
DESIGN DEVELOPMENT

STATUS
FOR REVIEW


DRAWING No.

L-102

SHEET

17
OF 21

ENLARGED PLAN B - FOUNTAIN COURT (next to the building) 20.00 x 20.00 m

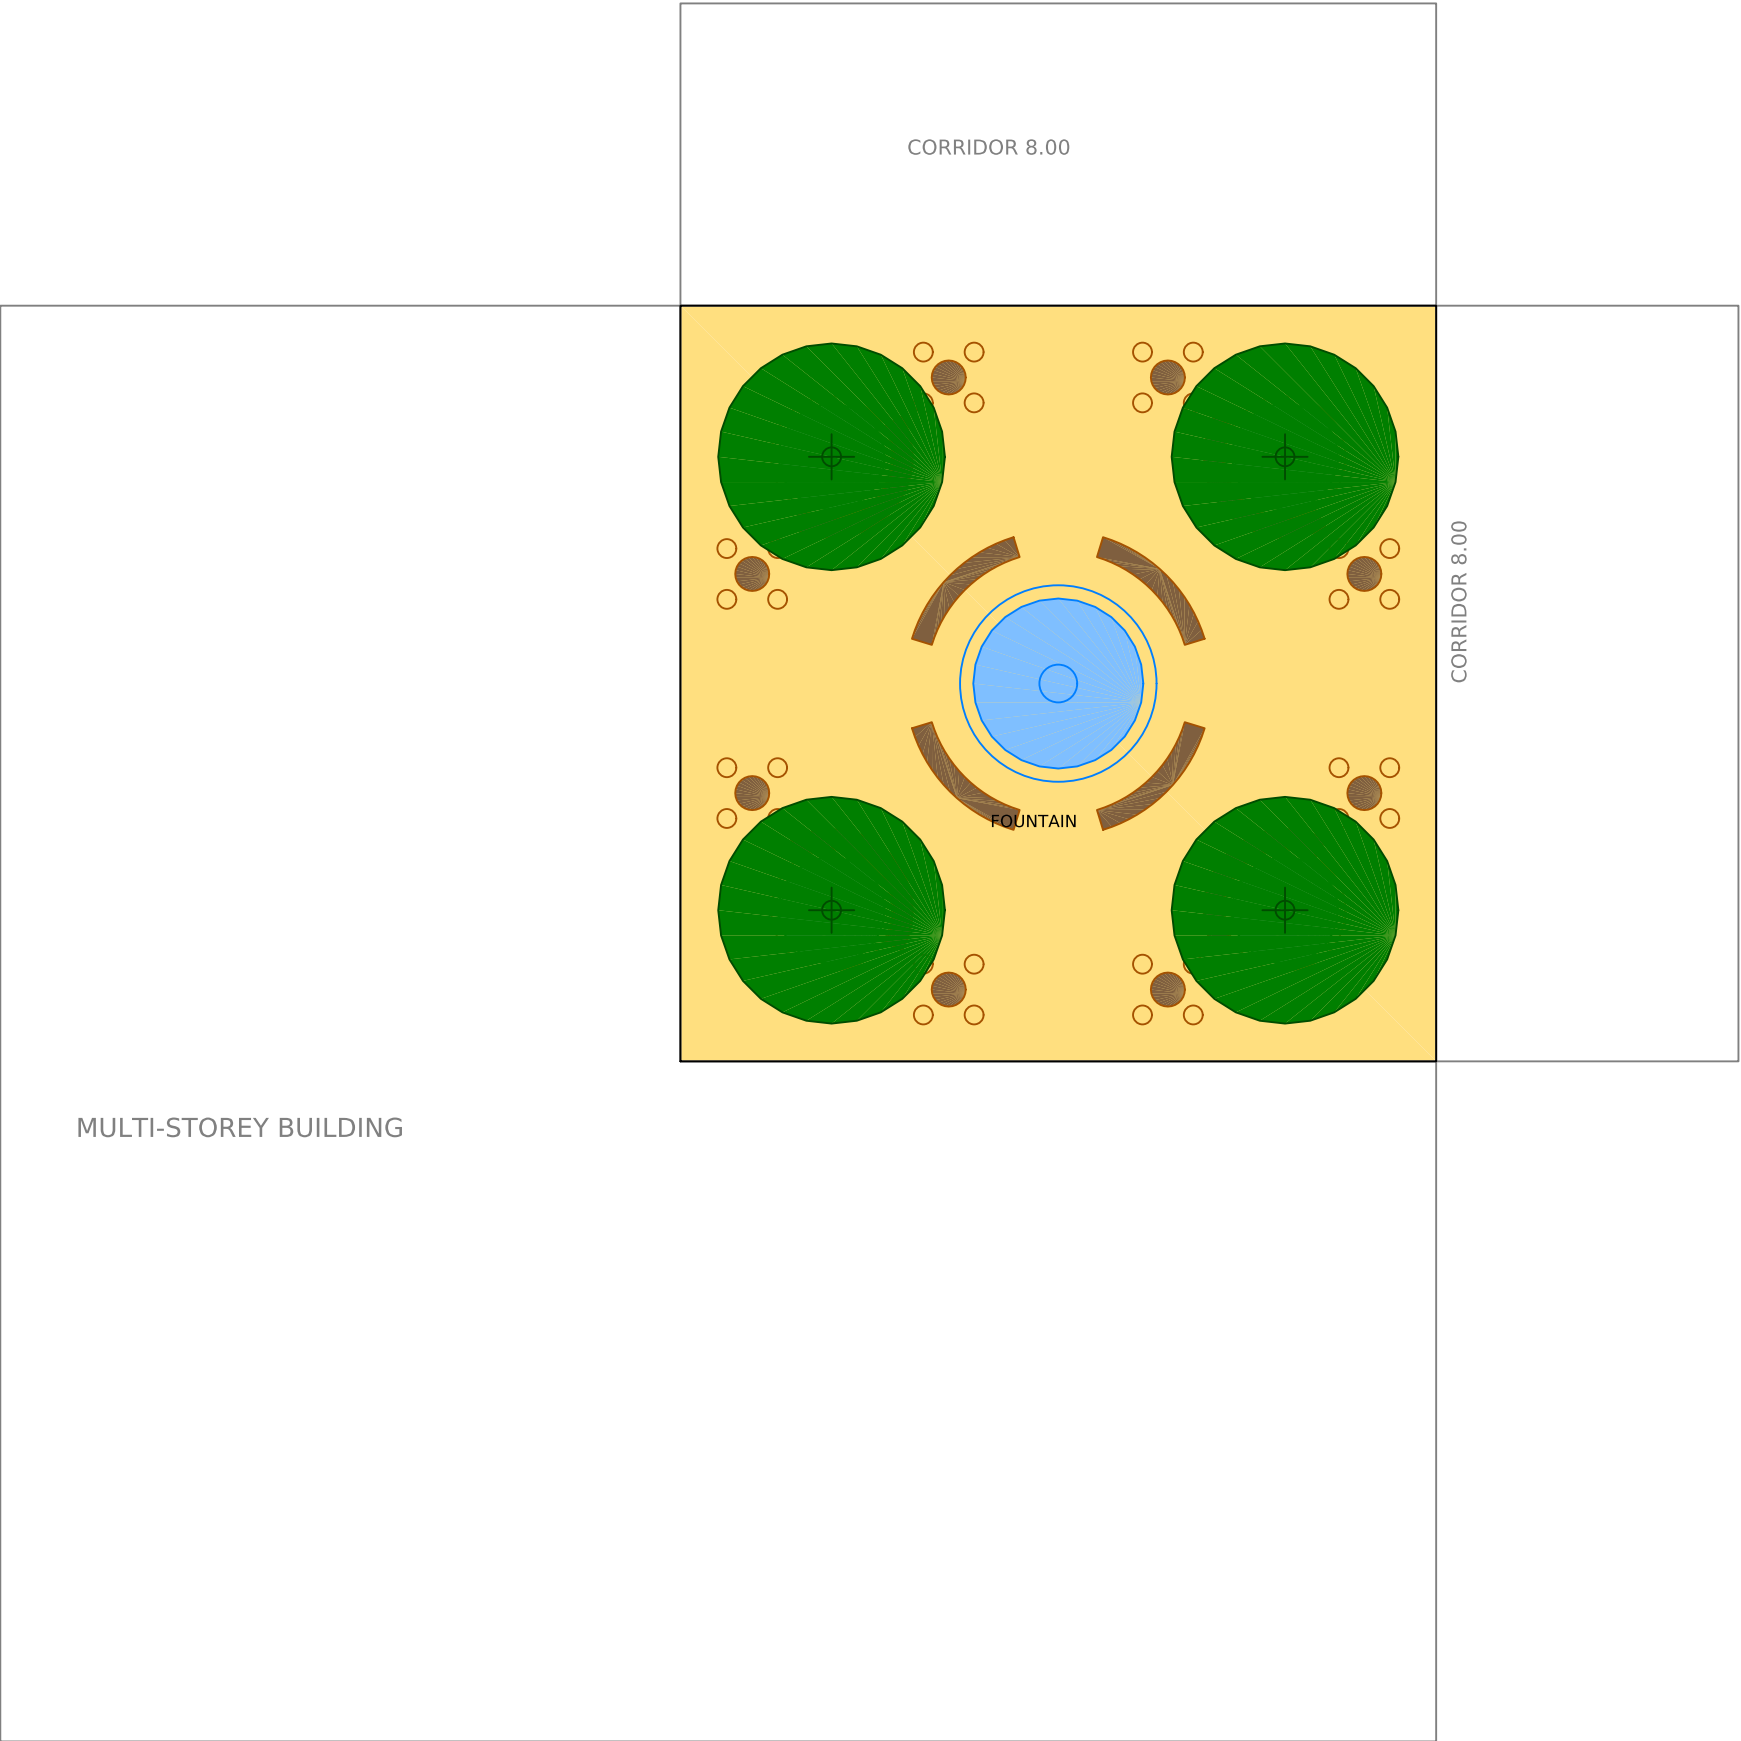

FOUNTAIN COURT - LEGEND

- Limestone paving
- Round fountain dia 5.20
- Shade trees in round planters (4)
- Curved benches + 8 cafe sets
- Planter seat walls

GENERAL NOTES

- ALL DIMENSIONS ARE IN METRES UNLESS OTHERWISE NOTED. LEVELS IN METRES.
- DO NOT SCALE FROM THIS DRAWING. USE FIGURED DIMENSIONS ONLY.
- VERIFY ALL DIMENSIONS ON SITE BEFORE STARTING ANY WORK.
- READ WITH ALL RELEVANT STRUCTURAL AND MEP DRAWINGS AND SPECIFICATIONS.
- COPYRIGHT OF THIS DRAWING IS RESERVED BY THE OFFICE.

KEY PLAN

NORTH

REVISIONS			
REV	DATE	DESCRIPTION	BY
00	30/09/2026	FIRST ISSUE	--

PROJECT
AL-YARMOUK COMMERCIAL SOUQ

LOCATION
MOSUL, IRAQ

CLIENT / OWNER
CLIENT NAME

PROJECT No.
PRJ-2026-002

DRAWING TITLE

FOUNTAIN COURT
ENLARGED LANDSCAPE PLAN

ROLE	NAME	SIGN.	DATE
DESIGNED	IBRAHIM MAHFOUDH		30/09/26
DRAWN	IBRAHIM MAHFOUDH		30/09/26
CHECKED	-		30/09/26
APPROVED	-		30/09/26

SCALE
1:200 @ A3

DATE
30/09/2026

PHASE
DESIGN DEVELOPMENT


STATUS
FOR REVIEW

DRAWING No.


L-103

SHEET

18
OF 21

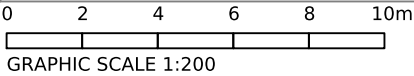

DIMENSION PLAN B - FOUNTAIN COURT

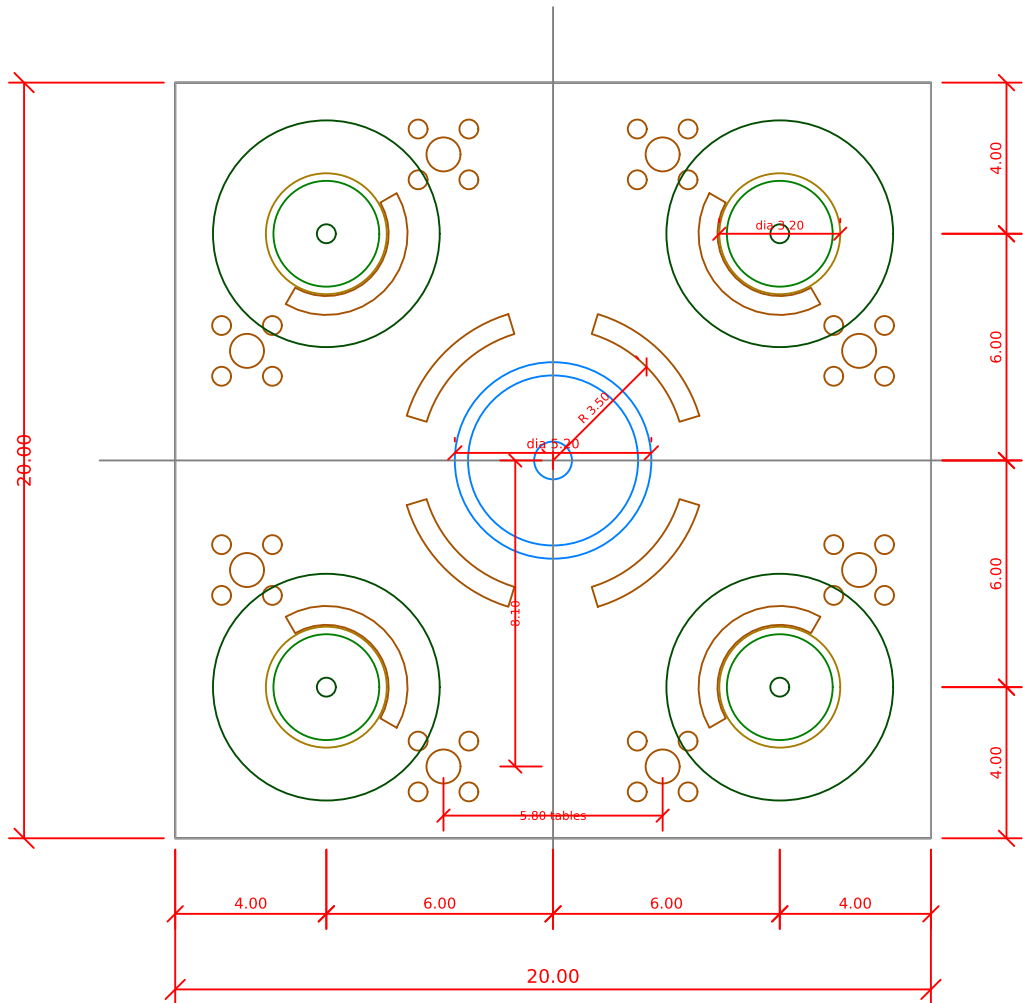

FOUNTAIN COURT - DIMENSIONS


All dimensions in metres.

Axes = centre of the fountain.

Planters on a 12.00 x 12.00 grid (+/-6.00).

Cafe sets 4 per side on +/-2.90 / 8.10.


Curved benches R 3.50, depth 0.55.

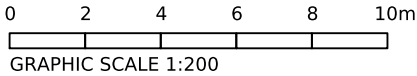

GENERAL NOTES


1. ALL DIMENSIONS ARE IN METRES UNLESS OTHERWISE NOTED. LEVELS IN METRES.
2. DO NOT SCALE FROM THIS DRAWING. USE FIGURED DIMENSIONS ONLY.
3. VERIFY ALL DIMENSIONS ON SITE BEFORE STARTING ANY WORK.
4. READ WITH ALL RELEVANT STRUCTURAL AND MEP DRAWINGS AND SPECIFICATIONS.
5. COPYRIGHT OF THIS DRAWING IS RESERVED BY THE OFFICE.

KEY PLAN

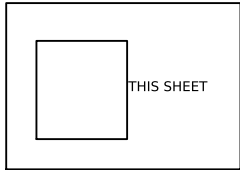

NORTH

N

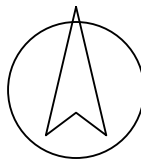

REVISIONS

REV	DATE	DESCRIPTION	BY
00	30/09/2026	FIRST ISSUE	--

PROJECT
AL-YARMOUK COMMERCIAL SOUQ

LOCATION
MOSUL, IRAQ

CLIENT / OWNER
CLIENT NAME

PROJECT No.
PRJ-2026-002

DRAWING TITLE

FOUNTAIN COURT
DIMENSION PLAN

ROLE	NAME	SIGN.	DATE
DESIGNED	IBRAHIM MAHFOUDH		30/09/26
DRAWN	IBRAHIM MAHFOUDH		30/09/26
CHECKED	-		30/09/26
APPROVED	-		30/09/26

SCALE
1:200 @ A3

DATE
30/09/2026

PHASE
DESIGN DEVELOPMENT

STATUS
FOR REVIEW


DRAWING No.

L-104

SHEET

19
OF 21

PRAYER HALL & ABLUTION - PLAN WITH DIMENSIONS & FURNITURE

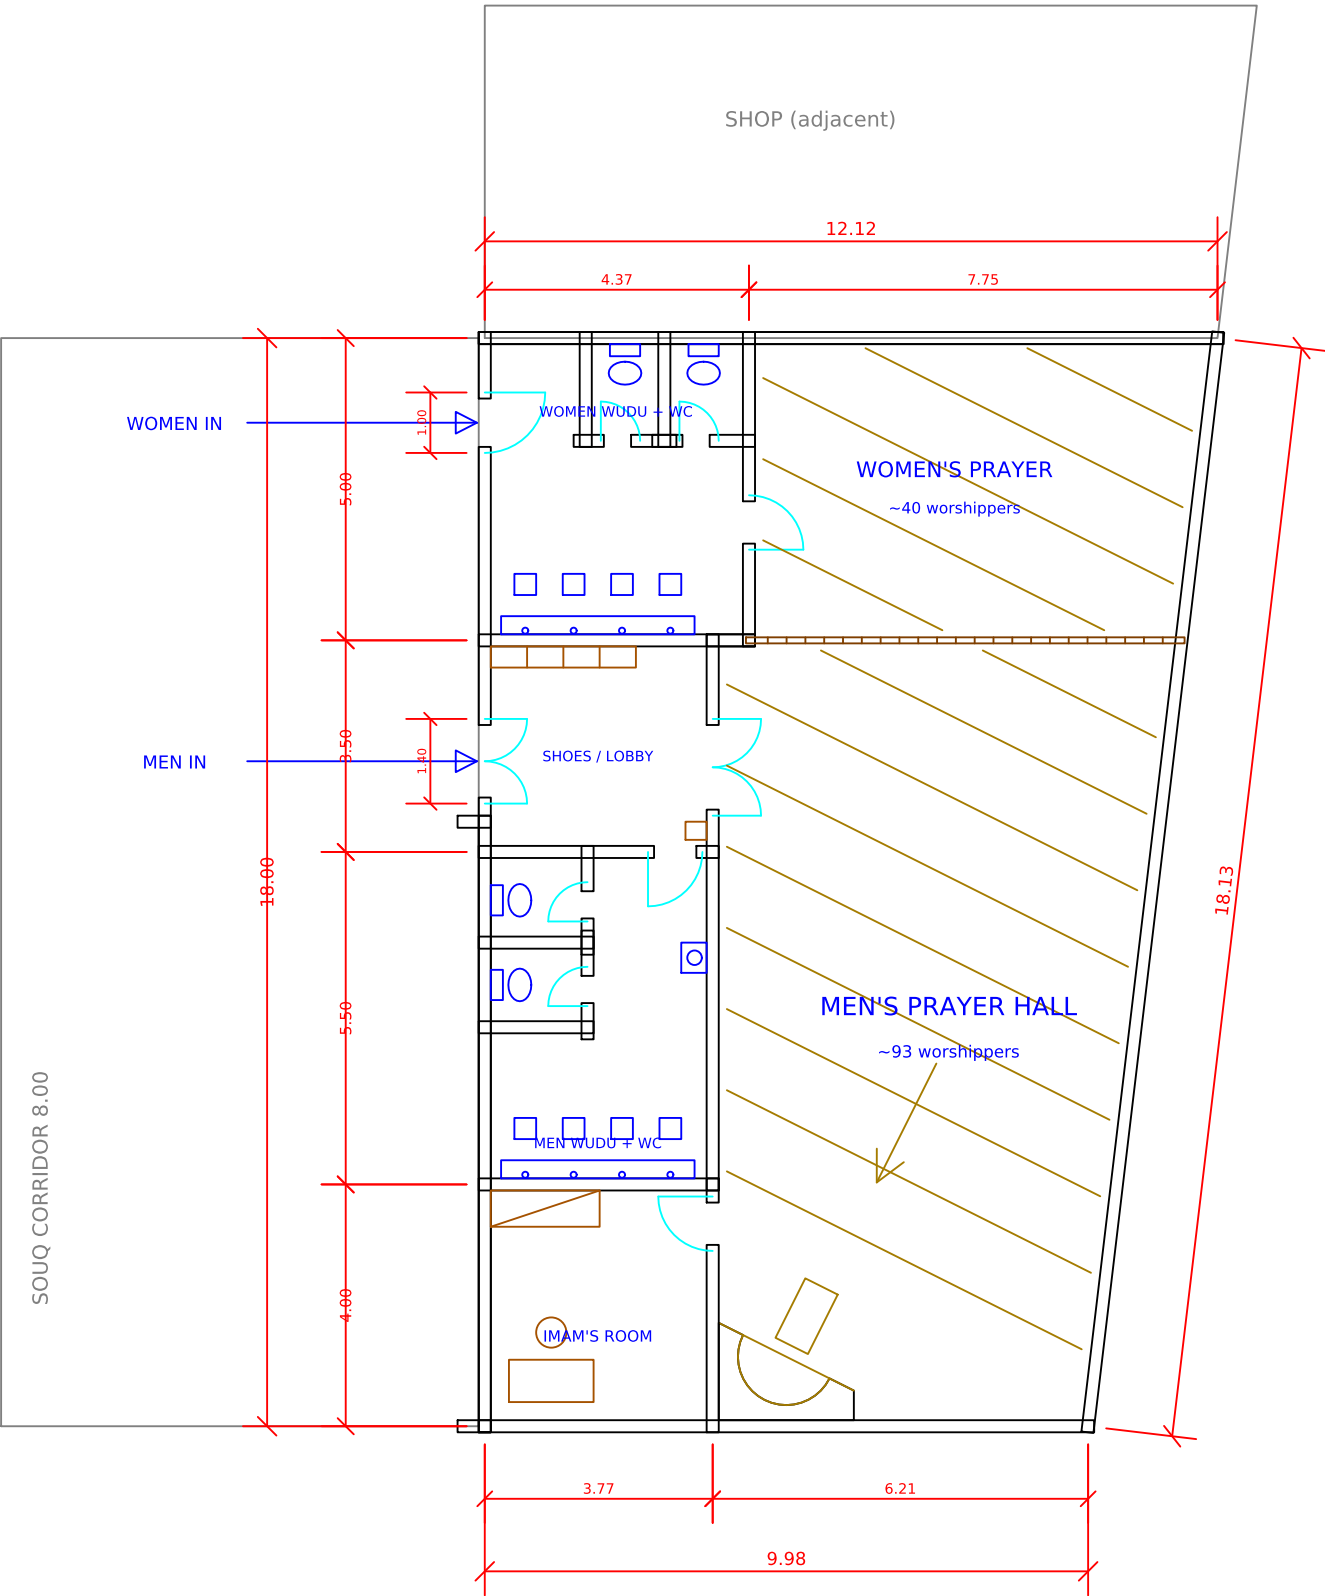

PRAYER HALL - SCHEDULE


Men's prayer hall	91 m2 (~93 persons)
Women's prayer	37 m2 (~40 persons)
Men wudu: 4 taps + 2 WC + basin	21 m2
Women wudu: 4 taps + 2 WC	22 m2
Shoe lobby	13 m2
Imam's room	15 m2
TOTAL	199 m2

Mihrab recessed in the qibla wall, axis 191 deg
(qibla assumes drawing +Y = north - to verify).
Mashrabiya screen between men / women halls.
Separate entrances from the souq corridor.
Prayer rows @ 1.20 m, perpendicular to qibla.

GENERAL NOTES

1. ALL DIMENSIONS ARE IN METRES UNLESS OTHERWISE NOTED. LEVELS IN METRES.
2. DO NOT SCALE FROM THIS DRAWING. USE FIGURED DIMENSIONS ONLY.
3. VERIFY ALL DIMENSIONS ON SITE BEFORE STARTING ANY WORK.
4. READ WITH ALL RELEVANT STRUCTURAL AND MEP DRAWINGS AND SPECIFICATIONS.
5. COPYRIGHT OF THIS DRAWING IS RESERVED BY THE OFFICE.

KEY PLAN

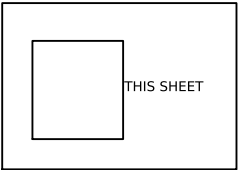

NORTH

N



REVISIONS

REV	DATE	DESCRIPTION	BY
00	30/09/2026	FIRST ISSUE	--

PROJECT
AL-YARMOUK COMMERCIAL SOUQ

LOCATION
MOSUL, IRAQ

CLIENT / OWNER
CLIENT NAME

PROJECT No.
PRJ-2026-002

DRAWING TITLE
PRAYER HALL & ABLUTION
PLAN - DIMENSIONS & FURNITURE

ROLE	NAME	SIGN.	DATE
DESIGNED	IBRAHIM MAHFOUDH		30/09/26
DRAWN	IBRAHIM MAHFOUDH		30/09/26
CHECKED	-		30/09/26
APPROVED	-		30/09/26

SCALE
1:125 @ A3


DATE
30/09/2026

PHASE
DESIGN DEVELOPMENT

STATUS
FOR REVIEW


DRAWING No.
A-401

SHEET
20
OF 21

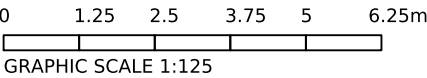



PUBLIC TOILETS - PLANS WITH DIMENSIONS & FIXTURES

PUBLIC WC 1 (north-west) - 5 + 5 cubicles

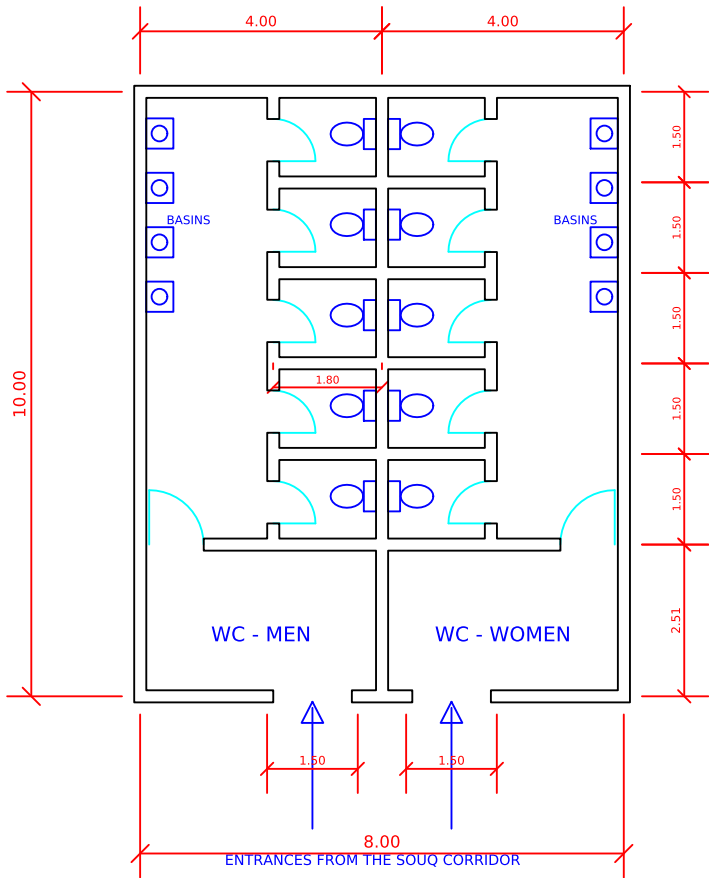

Cubicles ~1.30 x 1.60, doors open inward 0.70; basins on outer walls; 1.50 open entrances.


PUBLIC WC 2 (north-east) - men + women side by side

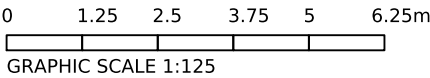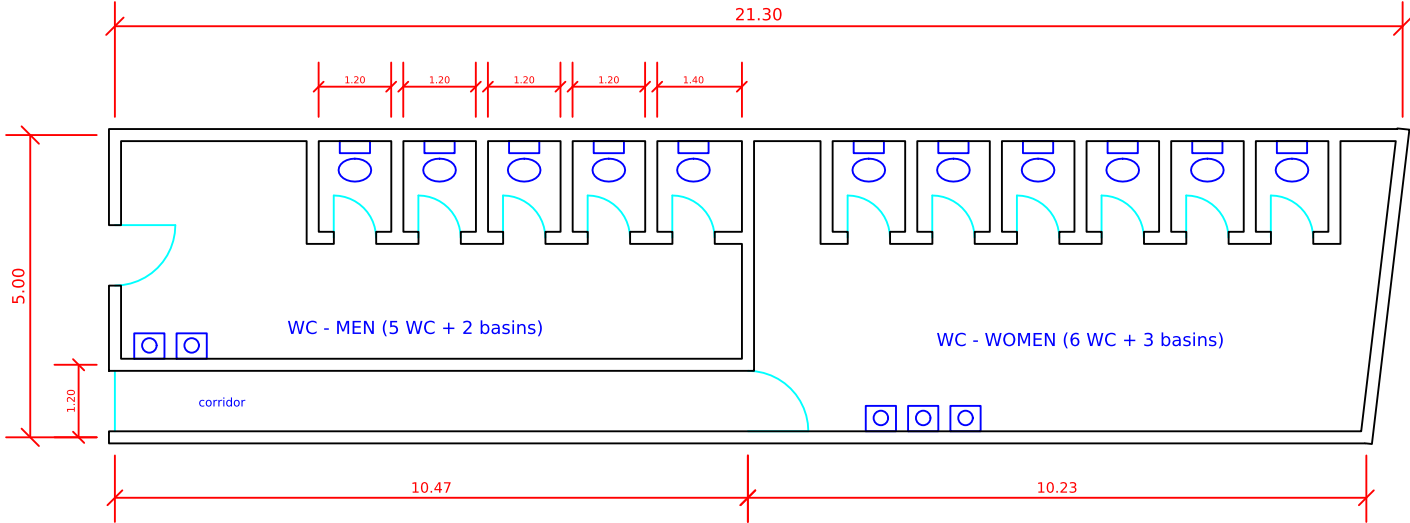

GENERAL NOTES

1. ALL DIMENSIONS ARE IN METRES UNLESS OTHERWISE NOTED. LEVELS IN METRES.
2. DO NOT SCALE FROM THIS DRAWING. USE FIGURED DIMENSIONS ONLY.
3. VERIFY ALL DIMENSIONS ON SITE BEFORE STARTING ANY WORK.
4. READ WITH ALL RELEVANT STRUCTURAL AND MEP DRAWINGS AND SPECIFICATIONS.
5. COPYRIGHT OF THIS DRAWING IS RESERVED BY THE OFFICE.

KEY PLAN

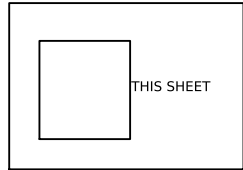

NORTH



REVISIONS

REV	DATE	DESCRIPTION	BY
00	30/09/2026	FIRST ISSUE	--

PROJECT
AL-YARMOUK COMMERCIAL SOUQ

LOCATION
MOSUL, IRAQ

CLIENT / OWNER
CLIENT NAME

PROJECT No.
PRJ-2026-002

DRAWING TITLE
PUBLIC TOILETS
PLANS - DIMENSIONS & FIXTURES

ROLE	NAME	SIGN.	DATE
DESIGNED	IBRAHIM MAHFOUDH		30/09/26
DRAWN	IBRAHIM MAHFOUDH		30/09/26
CHECKED	-		30/09/26
APPROVED	-		30/09/26

SCALE
1:125 @ A3

DATE
30/09/2026

PHASE
DESIGN DEVELOPMENT

STATUS
FOR REVIEW

DRAWING No.

A-402

SHEET

21
OF 21