
CIRCULATION + RELATIONSHIPS - VARIANT 1 | مخطط المسارات والعلاقات - البديل 1: الحلقة الخضراء (تعديل 1)

مجمع الشلالات السكني - القطعة 157 م53 بابيوخت - فرصة هيئة استثمار نينوى 5/2026

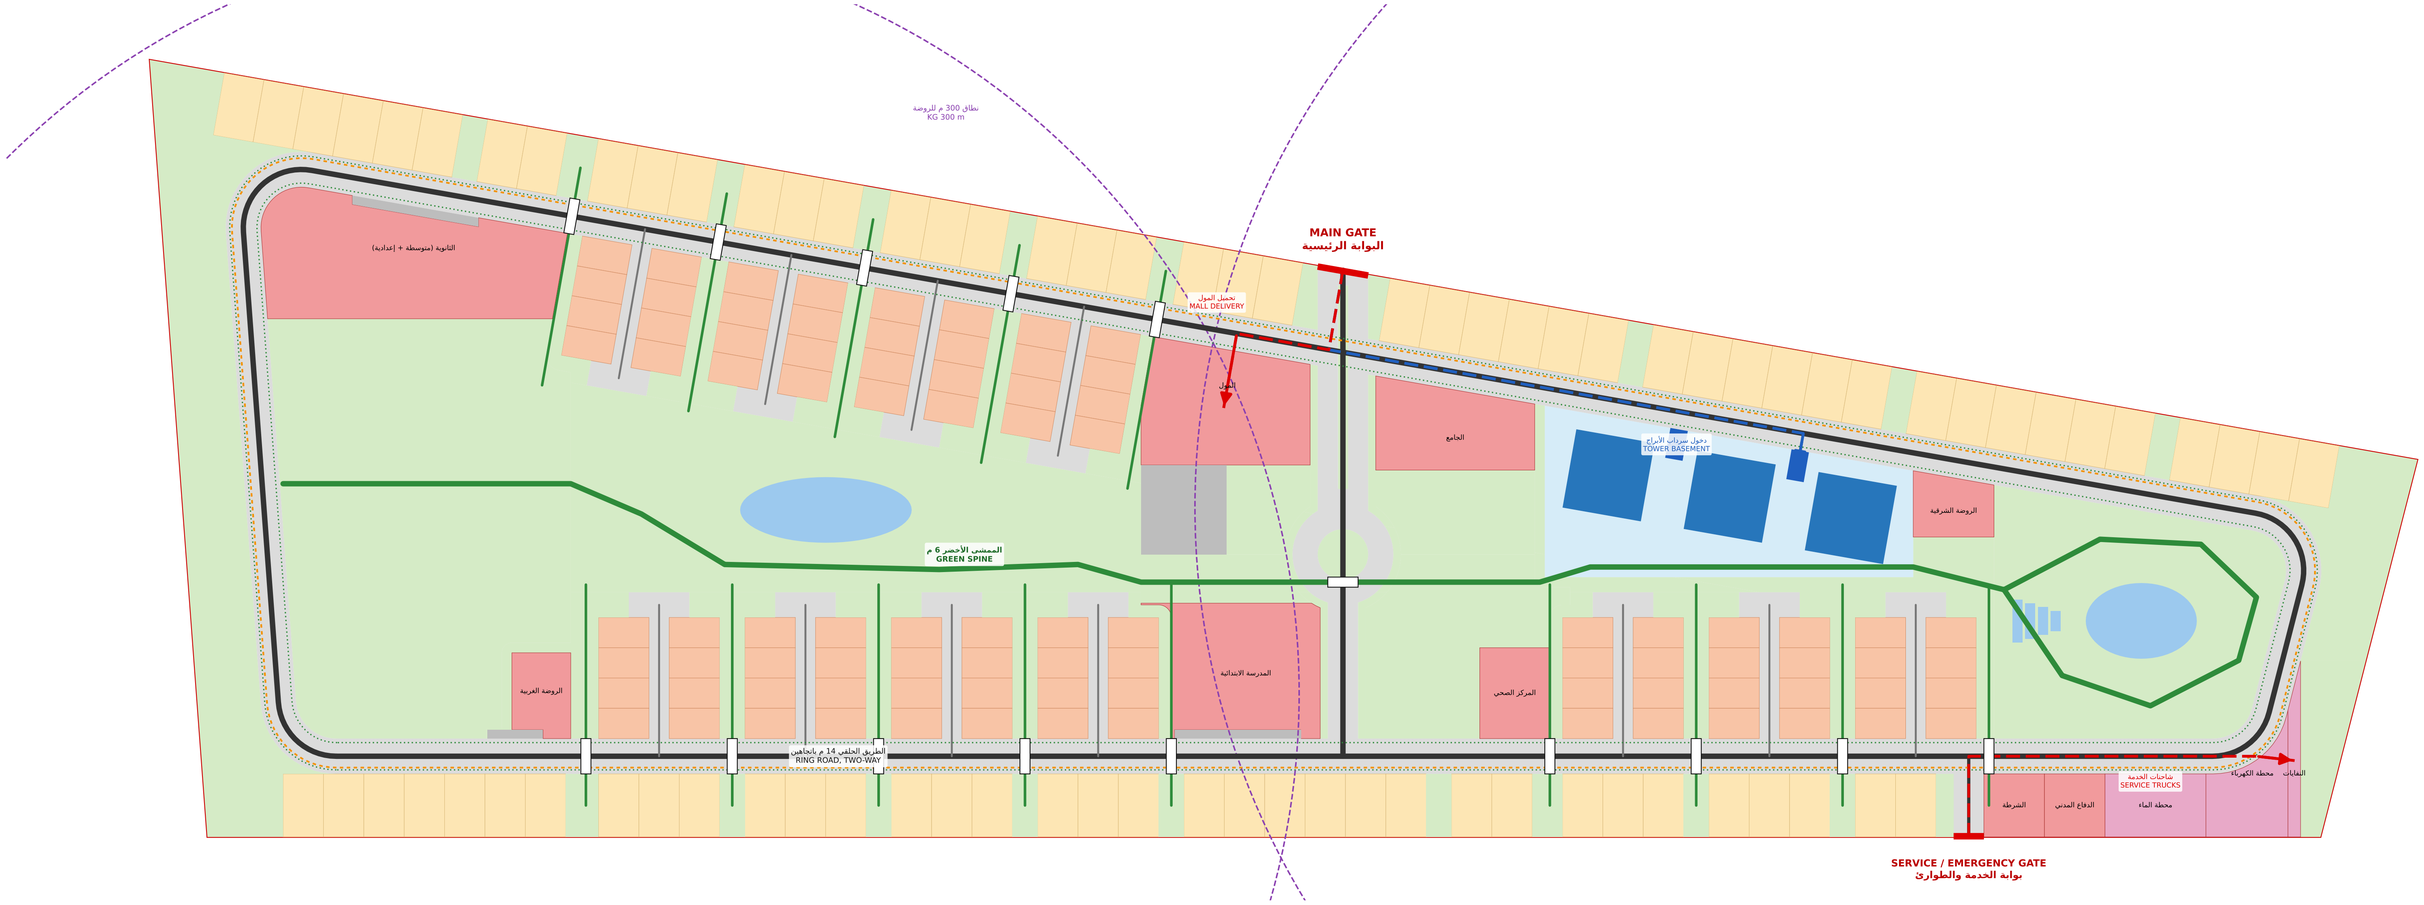

العلاقات:

- الفلل: واجهة على الحلقة، ظهر للسور؛ كل مجموعة تطل على حديقة جيب ومعبر إلى إصبع أخضر.
- الدور: أزقة قصيرة بلا مرور عابر، تنتهي على الممشى الأخضر والحديقة المركزية.
- الأبراج: على المحور قرب البوابة، سياراتها لا تمر بالأحياء، والروضة الشرقية بجانبها.
- المركز المدني على محور البوابة: المول والجامع عند الدخول، الابتدائية والصحي جنوب الدوار.
- الأطفال: الروضتان والابتدائية على الممشى الأخضر، والوصول مشيا دون عبور غير معبر واحد.
- الخدمة: الماء والكهرباء والنفايات والشرطة والدفاع المدني على بوابة الخدمة بعيدا عن السكن.
- الطوارئ: الحلقة دائرة مغلقة بمدخلين، وكل زقاق برأس دوران 24×10 م لسيارة الإطفاء.
- لا شارع عند الطرفين القصيرين، ولا شارع داخلي يفتح على الشوارع الخارجية.

أبعد مسافة مشي من أي سكن (خط مستقيم)

الخدمة	المسافة م
الروضتان (750+750)	290
المدرسة الابتدائية	408
الجامع	463
المول	398
المركز الصحي	536
الثانوية	699

الروضة كانت 538 م قبل التقسيم؛ دليل الإسكان: 300 م للروضة.

- Ring + gate axis - الطريق الحلقي ومحور البوابة (سيارات)
- Cul-de-sacs - أزقة العناقيد المغلقة (8 دور لكل زقاق)
- Tower cars to basement - سيارات الأبراج إلى السرداب
- Service + delivery - شاحنات الخدمة وتحميل المول
- Emergency loop - مسار الطوارئ: الحلقة كاملة + رؤوس الأزقة
- Green spine - الممشى الأخضر 6 م
- Finger walks - ممرات الأصابع الخضراء
- Tree-lined ring walk - ممشى الحلقة المشجّر 1.9 كم
- KG catchments - نطاق مشي 300 م للروضتين
- Parking + drop-off bays - موقف المول وأماكن إنزال الطلاب
- Raised zebra crossing - معبر مشاة مرتفع