MASTER PLAN - VARIANT 1: THE GREEN RING - REV 1 | المخطط العام - البديل 1: الحلقة الخضراء (تعديل 1)

مجمع الشلالات السكني - القطعة 157 م53 بايبوخت - فرصة هيئة استثمار نينوى 5/2026 - بنفس إظهار مقترح ابراهيم المطوّر

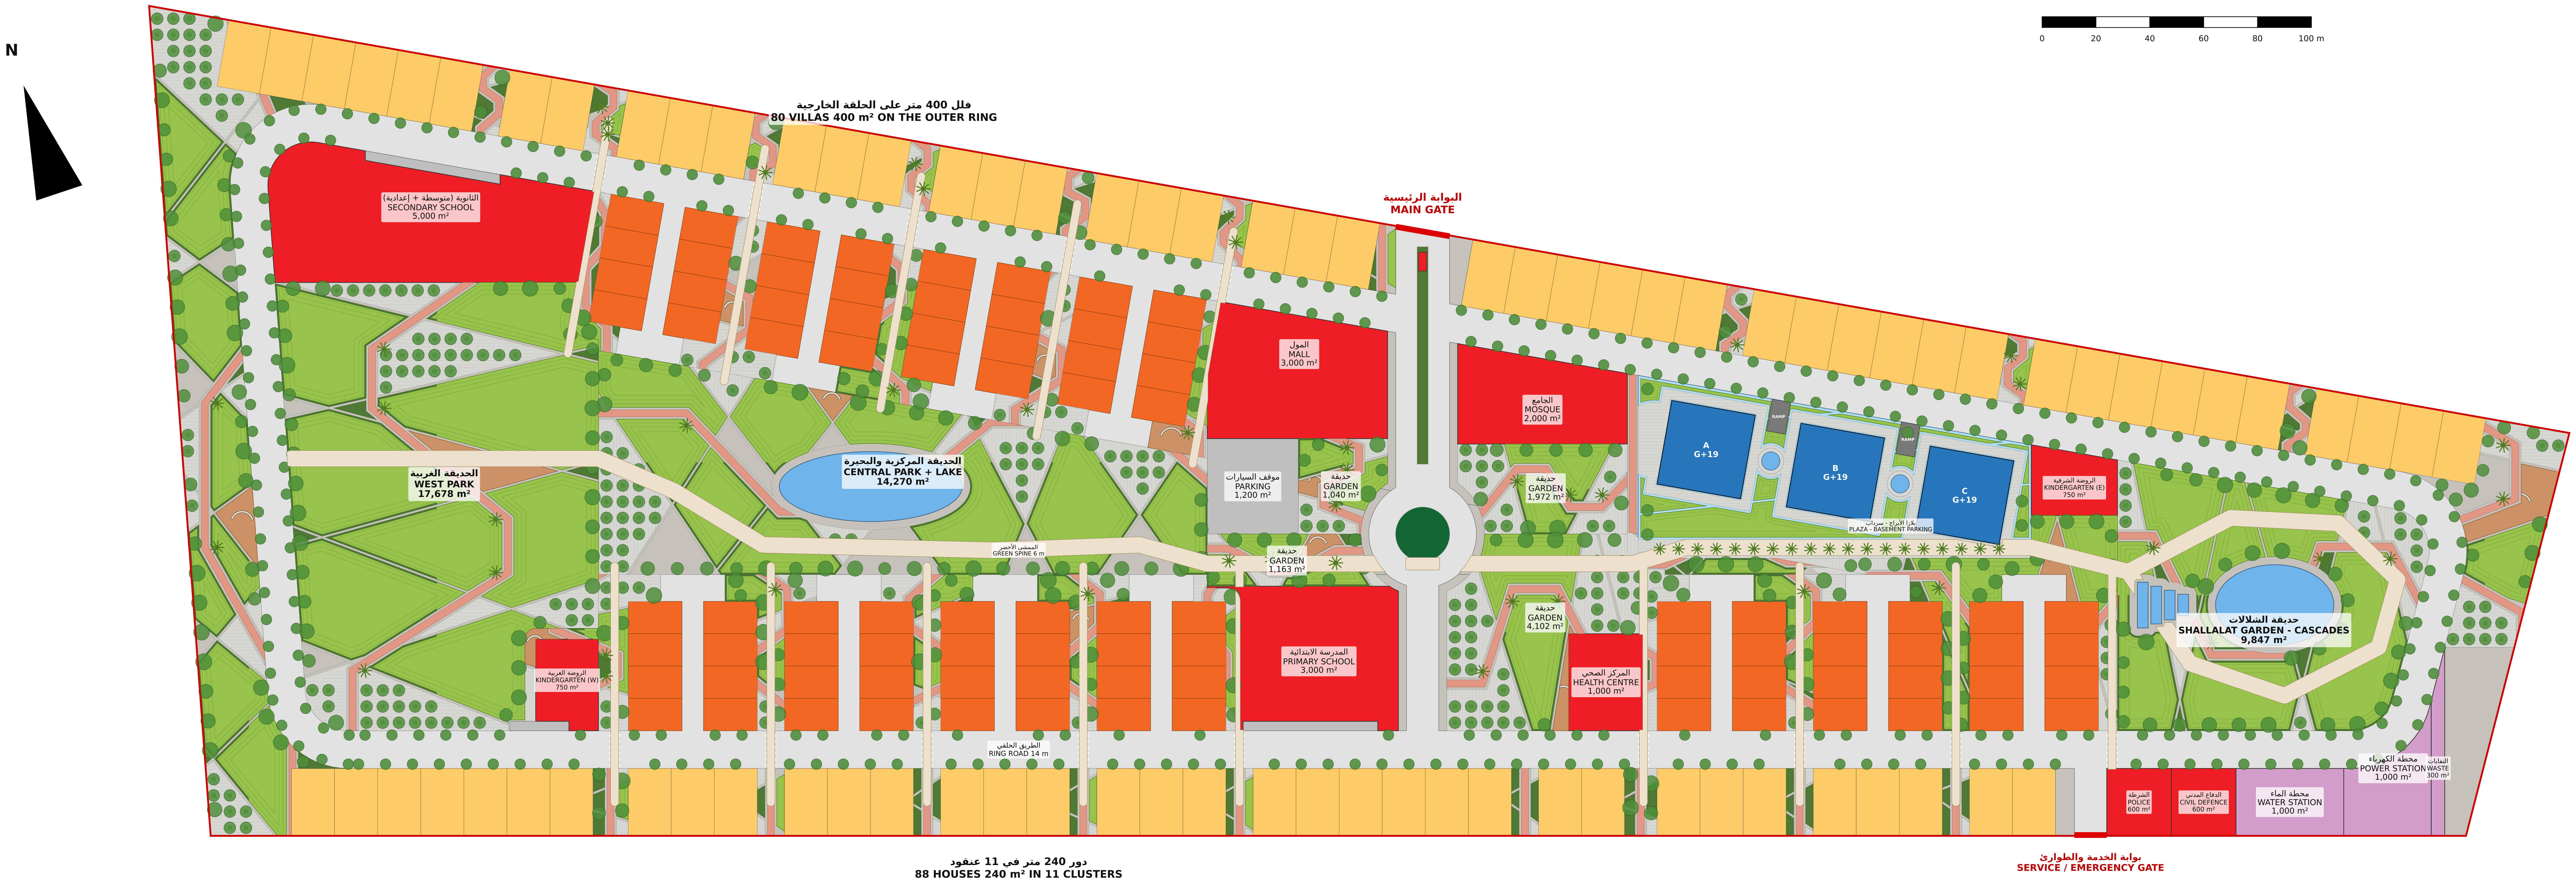

```
Plot 157 / District 53 Baybokht - NIC 5/2026 - UTM 38S
UNITS: 80 villas 400 m2 + 88 houses 240 m2 + 240 flats = 408
Towers: 3 x 20 floors x 4 flats; parking 360 cars in a basement under the plaza
Entrances: 1 main gate (north road) + 1 service / emergency gate (south road)
```

LAND USE	m²	%	استعمالات الأرض
Villas 400 m2 (80)	32,000	16.1	فلل 400 م2
Houses 240 m2 (88)	21,120	10.6	دور 240 م2
Towers (3) + plaza	8,032	4.0	الأبراج والبلازا
Community services	16,700	8.4	الخدمات
Utilities	2,300	1.2	المرافق الفنية
Parks, gardens, green fingers	80,648	40.5	الحدائق والأصابع الخضراء
Parking: mall + school drop-off bays	1,630	0.8	مواقف المول وأماكن إنزال الطلاب
Roads	36,746	18.4	الشوارع
TOTAL	199,177	100.0	المجموع

🟨	Villa plot 400 m² - فلل 400 متر
🟧	House plot 240 m² - دور 240 متر
🟦	Tower G+19 - الأبراج
🟦	Plaza over the basement car park - البلازا فوق السرداب
🟥	Community services - الخدمات
🟪	Utilities - المرافق الفنية
🟩	Lawns, raised mounds - مسطحات خضراء مرتفعة
🟫	Coloured jogging track - مسار ملون
🟩	Shrub beds - أحواض شجيرات
🟦	Lake, cascades, fountains - بحيرة وشلالات ونوافير
⬜	Parking, drop-off bays - مواقف وأماكن إنزال
⬜	Roads - الشوارع
⬜	Green spine + finger walks - الممشى الأخضر وممرات الأصابع
—	Gate - بوابة

الفكرة: طريق حلقي مشجّر بعرض 14 م يطوّق المجمع؛ الفلل خارجه والدور في عناقيد داخله.

تعديل 1 (العلاقات والمسارات):

1. كل إصبع أخضر (10 م) يقابل حديقة جيب بين الفلل ومعبر مشاة مرتفع على الحلقة:
   الفيلا تمشي مباشرة عبر الإصبع إلى الممشى الأخضر والحديقة المركزية.
2. ممشى أخضر 6 م من الحديقة الغربية إلى حديقة الشلالات، يعبر المحور بمعبر واحد.
3. الروضة قسمت إلى روضتين 750+750 م2 (غرب وشرق): أبعد بيت 290 م بدل 538 م.
4. أماكن إنزال طلاب على الحلقة أمام الابتدائية والثانوية والروضة الغربية.
5. سيارات الأبراج تدخل السرداب من منحدرين بين الأبراج مباشرة من الحلقة.
6. شاحنات الخدمة: بوابة الخدمة ثم القوس الجنوبي الشرقي فقط، بلا مرور بين البيوت.
7. كشك حراسة عند البوابة الرئيسية؛ الشرطة عند بوابة الخدمة.
8. حذف النادي (طلب المعماري) وتحويل أرضه إلى الحديقة الغربية.

الشوارع 18% والخضرة 40%؛ سرداب 360 سيارة.

مخطط المسارات والعلاقات في لوحة مستقلة.

Layers MP_*, circulation on MP_CIRC_*; colours and landscape follow Ibrahim's proposal.