
MASTER PLAN - PROPOSAL C - GREEN VALLEY

مجمعالشلالات السكني - المقترح :الوادي الأخضر

المخطط العام - القطعة 157 مقاطعة 53بابيوخت - 199,175 م² إحداثيات UTM 38S

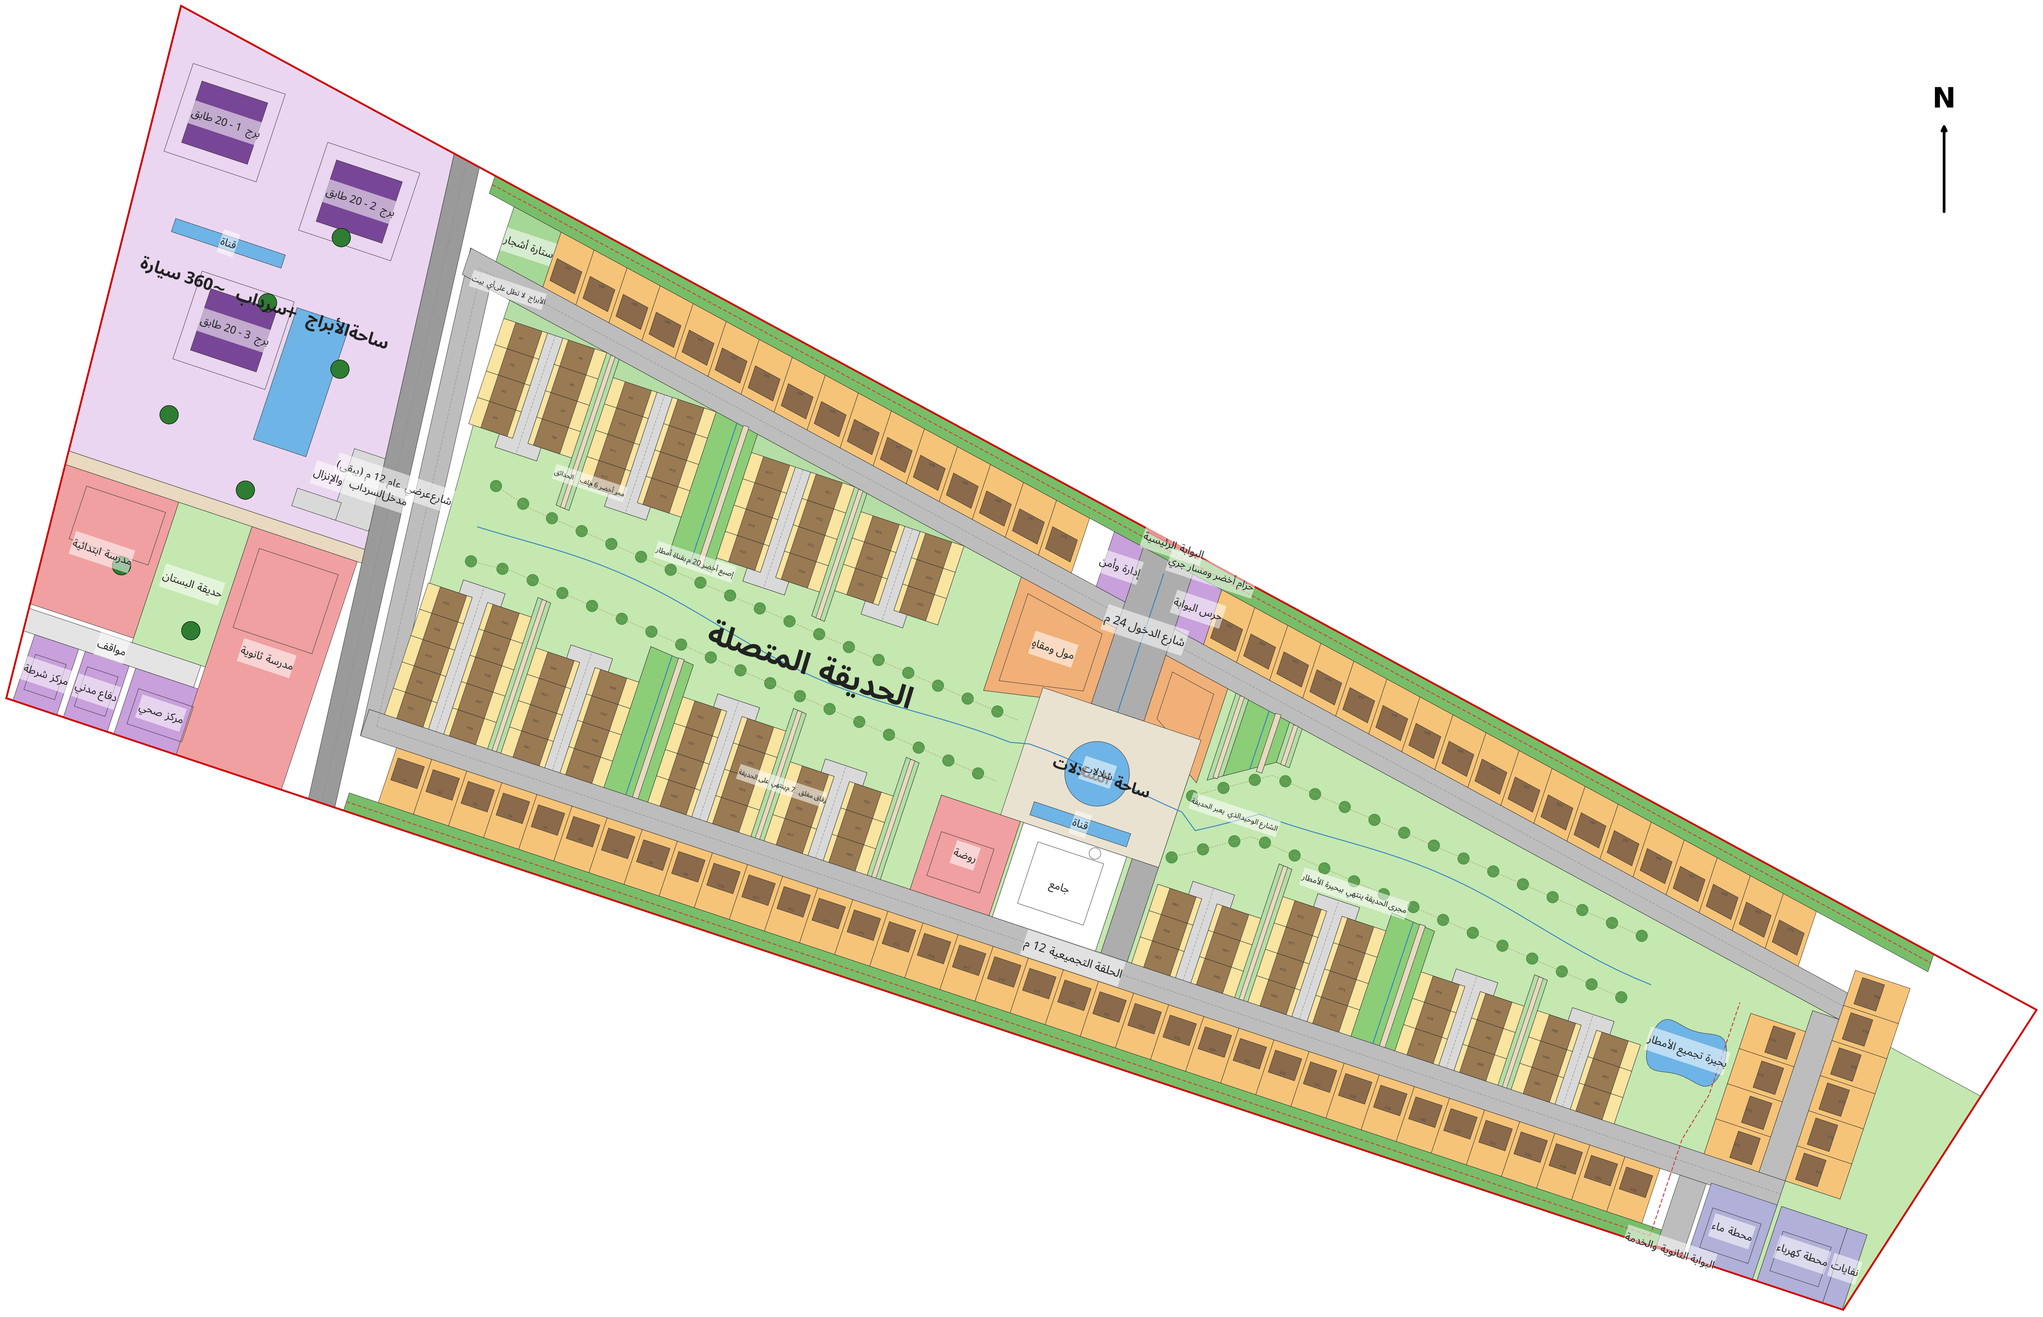

0 20 40 60 80 100 m

- بنى تحتية
- حديقة
- إصبع أخضر
- حزام أخضر
- ماء
- شوارع
- فيلا 400 م²
- دار 240 م²
- برج 20 طابق
- تعليم
- خدمات عامة
- تجاري
- مسار جري

البرنامج

- فلل 400 م²: 80
- دور 240 م²: 88
- شقق الأبراج : 240 (3أبراج × 20 طابقاً × 4)
- المجموع: 408 وحدة
- السكان التقريبي : 2,208 نسمة
- الخضرة: 30%من القطعة
- الشوارعوالمواقف : 17%من القطعة
- كلبيت يطلمنالخلف على خضرة

استعمالات الأرض

- فلل 400 م²: 32,000 م² (16.1%)
- دور 240 م²: 21,120 م² (10.6%)
- ساحةالأبراج : 24,712 م² (12.4%)
- الخدمات العامة والتعليمية والتجارية والبنى التحتية: 19,796 م² (9.9%)
- الشوارعوالمواقف والساحة: 34,460 م² (17.3%)
- الحدائق والمساحات الخضراءوالممرات : 59,650 م² (29.9%)
- فضلاتوحواف : 7,439 م² (3.7%)
- المجموع: 199,177 م²

الخدمات - المرسوم /البرنامج (م²)

- الشارعالعرضي العام: 3,403
- مركز شرطة: 600 / 600
- دفاعمدني : 600 / 600
- مركز صحي: 990 / 1,000
- مدرسة ثانوية: 4,992 / 5,000
- مدرسة ابتدائية: 3,064 / 3,000
- حديقةالبستان : 2,137
- ساحةالأبراج +سرداب ~360 سيارة: 24,712
- إدارةوأمن البوابات : 700
- مول ومقاهٍ: 3,073 / 3,000
- جامع: 2,021 / 2,000
- روضة: 1,548 / 1,500
- محطة ماء: 1,020 / 1,000
- محطة كهرباء: 1,020 / 1,000
- نفايات : 306 / 300