
المخطط العام - المقترح ب: القلب الأخضر

MASTER PLAN - PROPOSAL B: THE GREEN HEART

مجمع الشلالات السكني · القطعة 157 مقاطعة 53 بابيوخت · فرصة هيئة استثمار نينوى 5/2026

UTM 38S · SCALE 1:2500 (A3) · 199,177 m2 · 2026-10-21

- فلل 400 م² (66)
- دور 200 م² (125)
- برجان 20 طابقاً (152 شقة)
- خدمات وبنى تحتية
- الحديقة المركزية
- حدائق وبستان ووادي
- طرق
- ماء

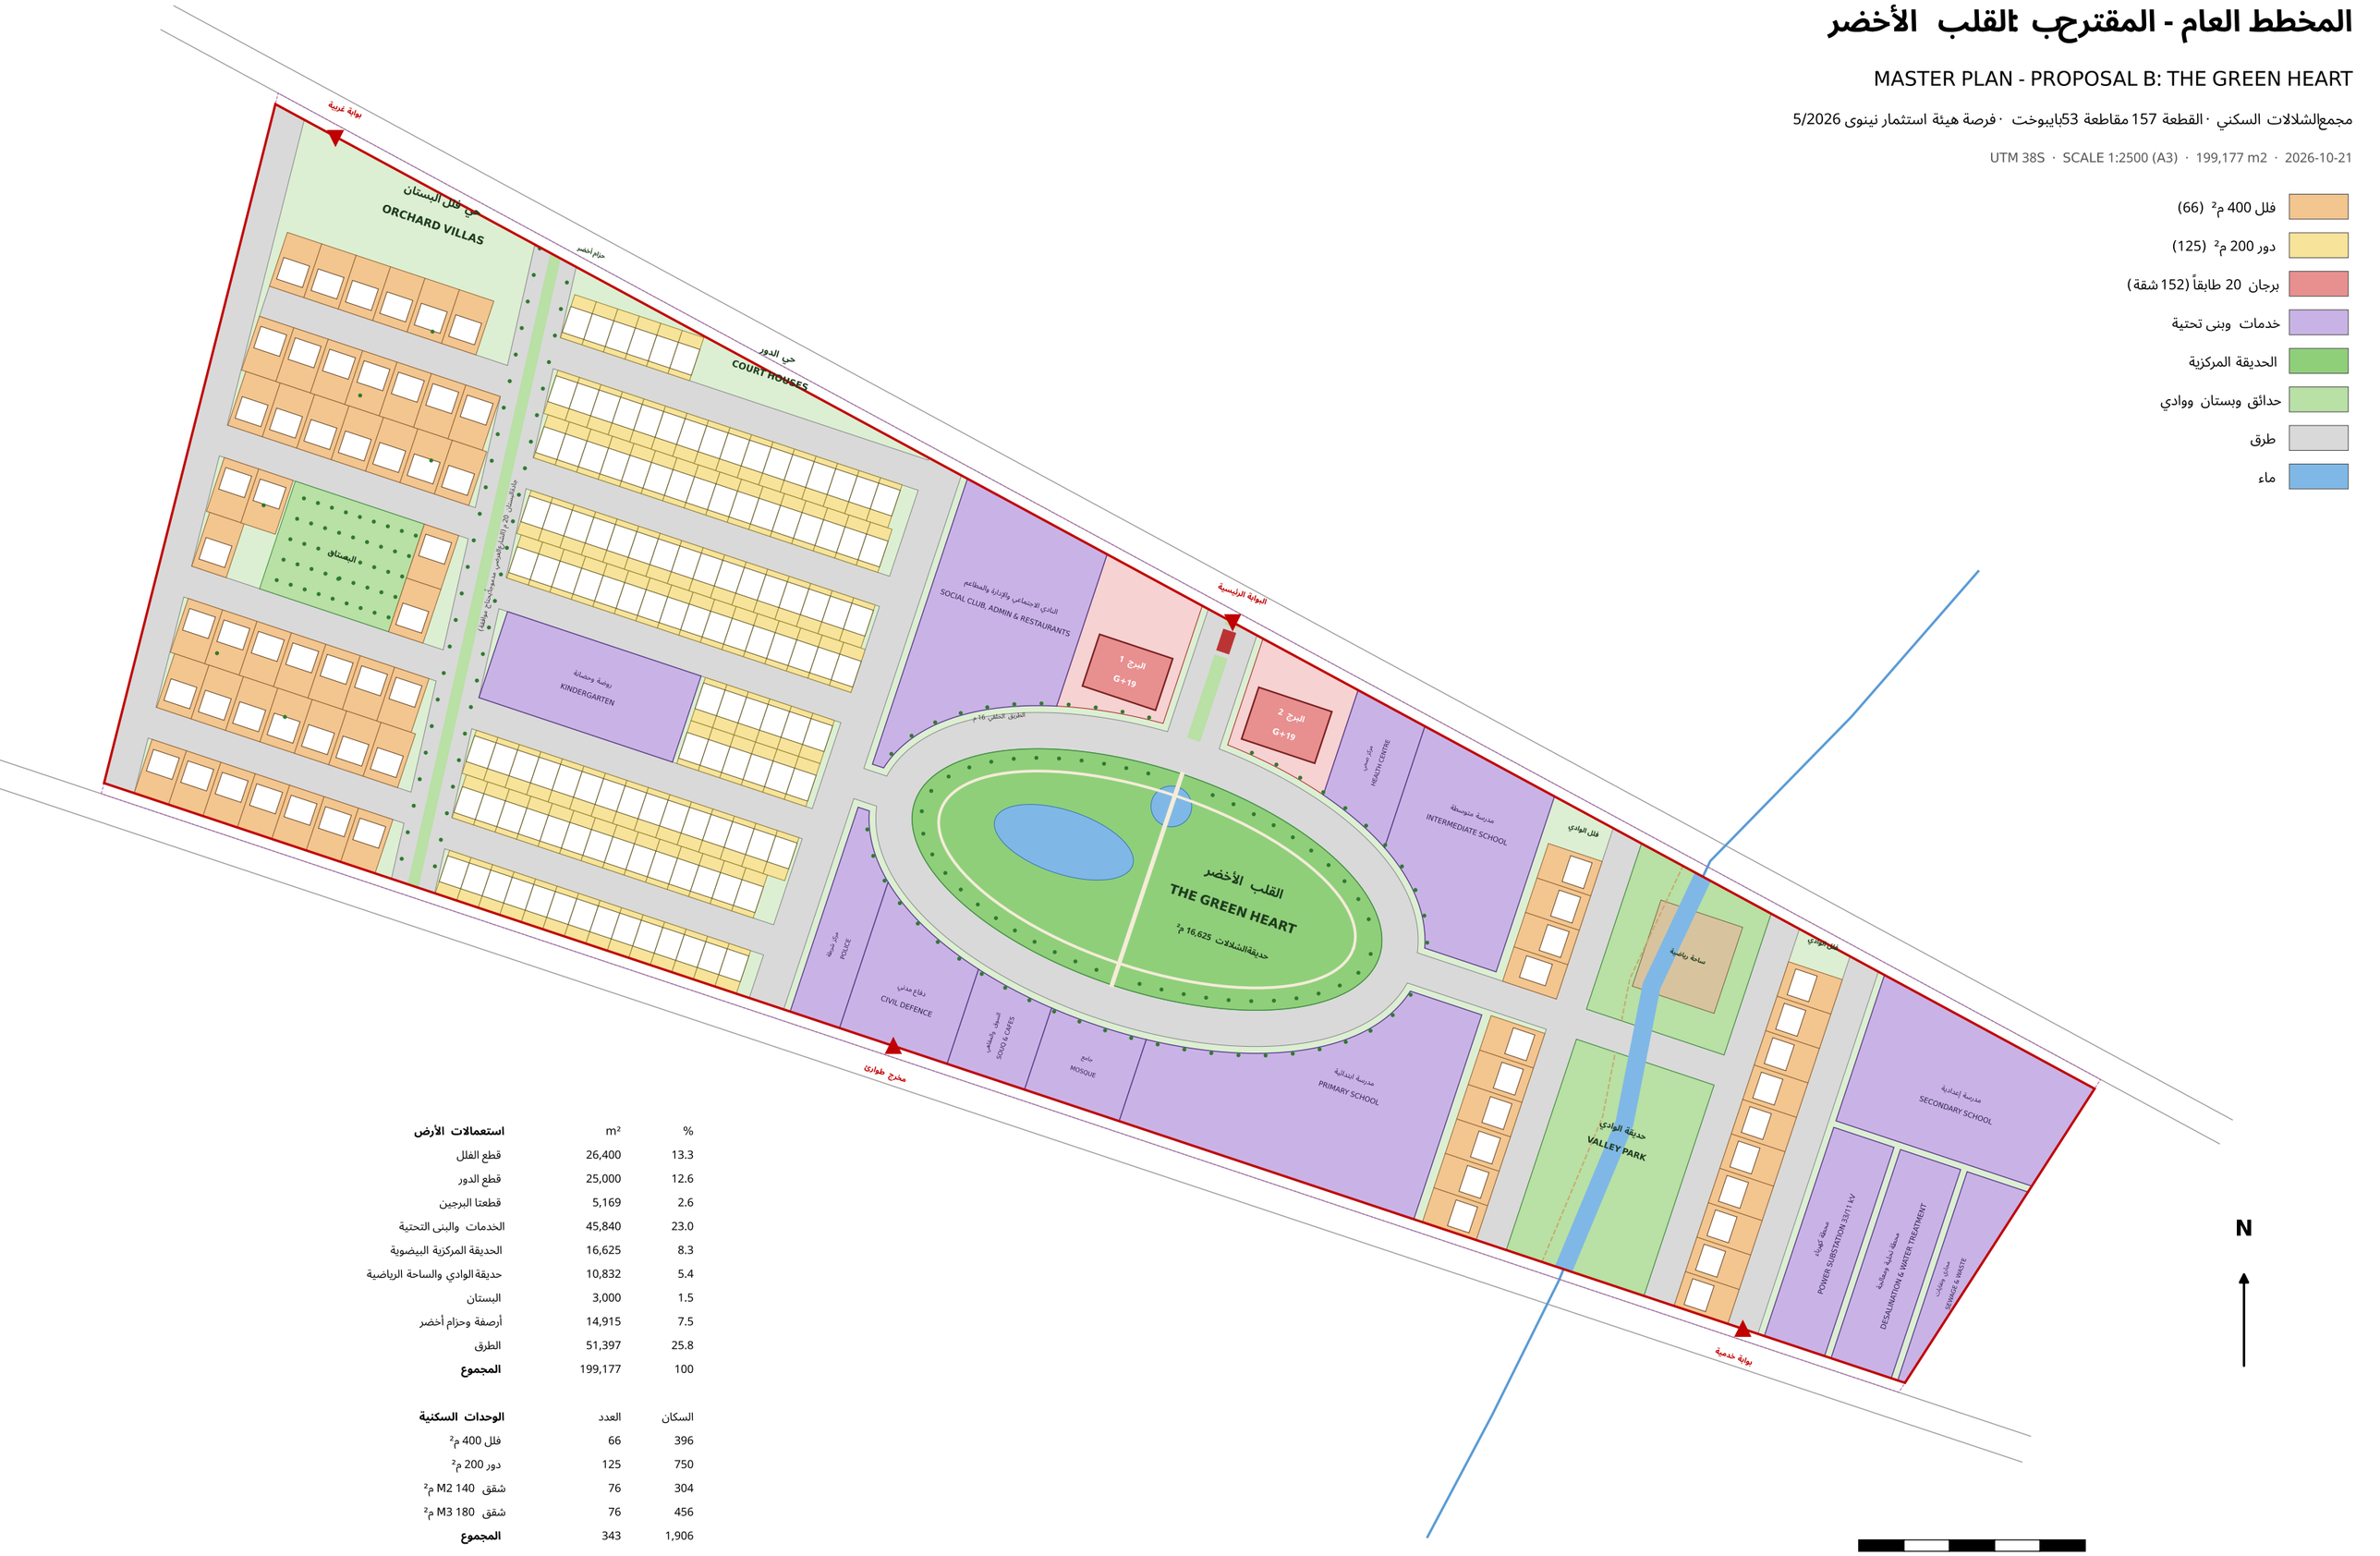

استعمالات الأرض	m²	%
قطع الفلل	26,400	13.3
قطع الدور	25,000	12.6
قطعتا البرجين	5,169	2.6
الخدمات والبنى التحتية	45,840	23.0
الحديقة المركزية البيضوية	16,625	8.3
حديقة الوادي والساحة الرياضية	10,832	5.4
البستان	3,000	1.5
أرصفة وحزام أخضر	14,915	7.5
الطرق	51,397	25.8
المجموع	199,177	100

الوحدات السكنية	العدد	السكان
فلل 400 م²	66	396
دور 200 م²	125	750
شقق M2 140 م²	76	304
شقق M3 180 م²	76	456
المجموع	343	1,906

الكثافة الإجمالية 96 شخص/هكتار

الخضرة العامة 16.0 م² للفرد