
المخطط العام - المقترح ب: القلب الأخضر (التعديل 2)

MASTER PLAN - PROPOSAL B: THE GREEN HEART - REV. 2

مجمع الشلالات السكني · القطعة 157 مقاطعة 53بابيوخت · فرصة هيئة استثمار نينوى 5/2026

UTM 38S · SCALE 1:2500 (A3) · 199,177 m2 · 2026-10-21

- فلل 400 م² (80)
- دور 240 م² (88)
- 3أبراج 20 طابقاً (240 شقة)
- خدمات وبنى تحتية
- الحديقة المركزية
- حدائق جيرةوبستان وأحزمة خضراء
- طرق
- ماء

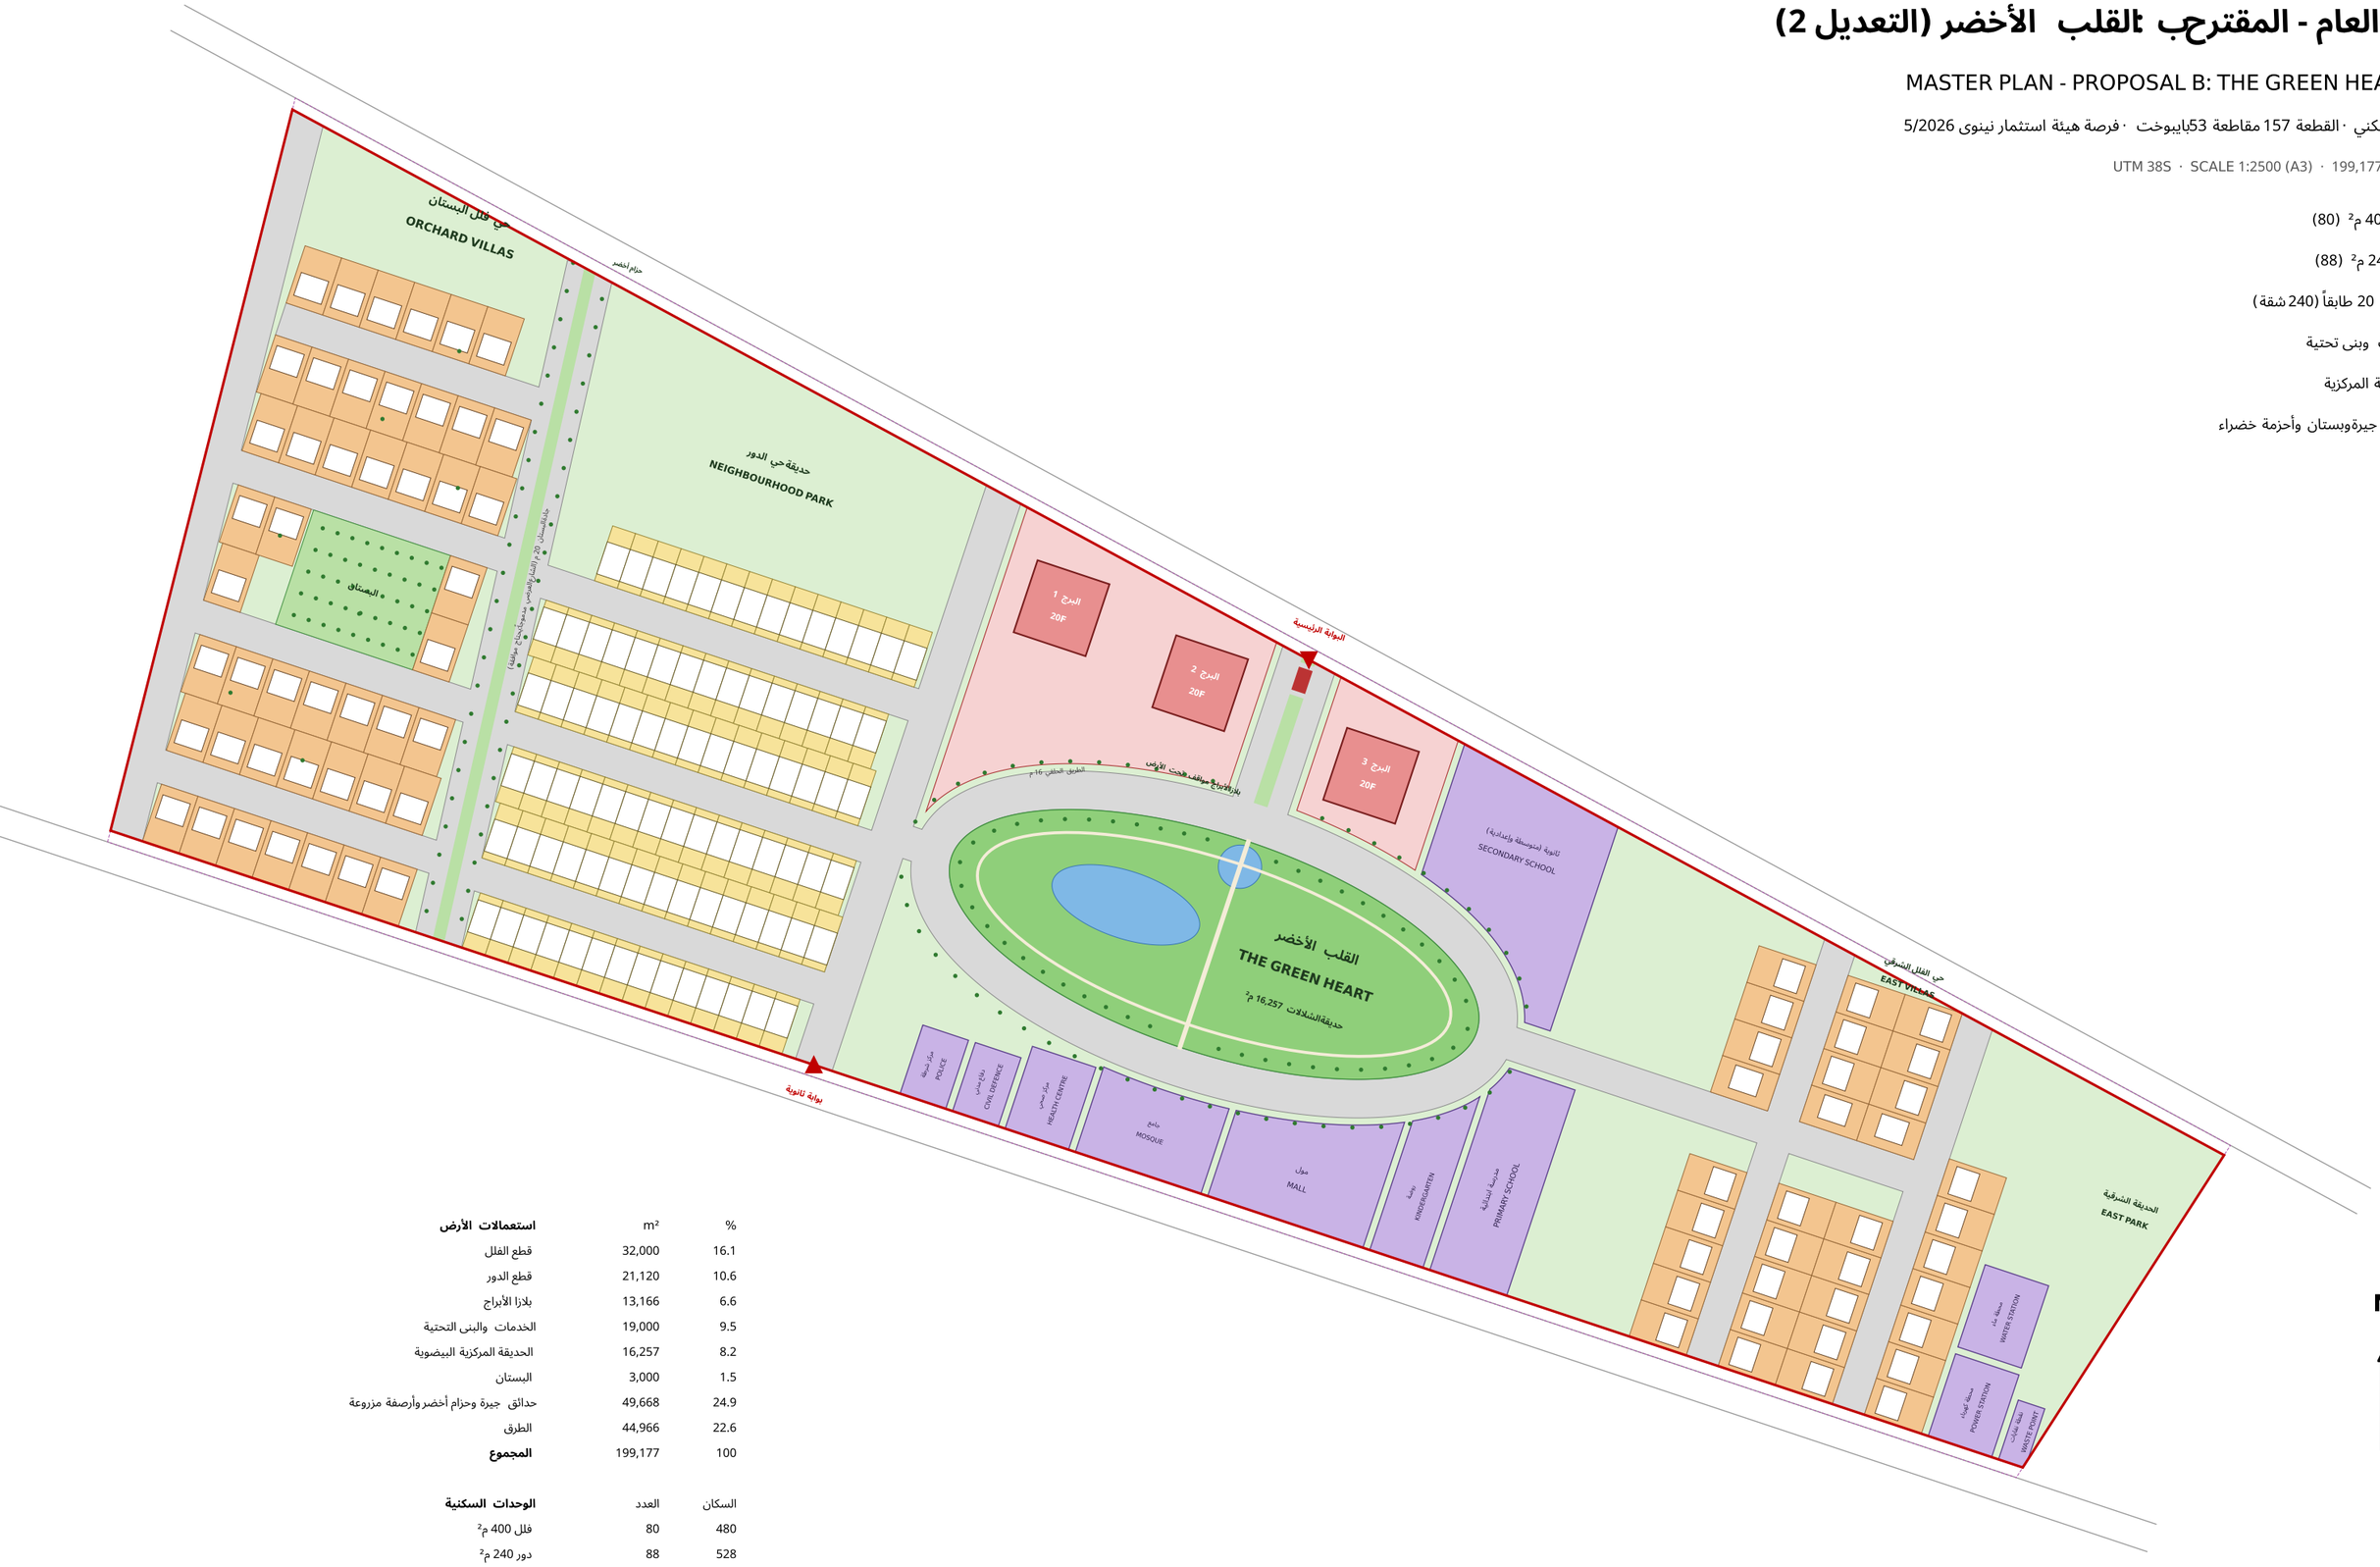

استعمالات الأرض	m²	%
قطع الفلل	32,000	16.1
قطع الدور	21,120	10.6
بلازا الأبراج	13,166	6.6
الخدمات والبنى التحتية	19,000	9.5
الحديقة المركزية البيضوية	16,257	8.2
البستان	3,000	1.5
حدائق جيرة وحزام أخضر وأرصفة مزروعة	49,668	24.9
الطرق	44,966	22.6
المجموع	199,177	100

الوحدات السكنية	العدد	السكان
فلل 400 م²	80	480
دور 240 م²	88	528
شقق M2 140 م²	120	480
شقق M3 180 م²	120	720
المجموع	408	2,208

الكثافة الإجمالية 111 شخص/هكتار

الخضرة العامة 31.2 م² للفرد