





GENERAL NOTES

1. ALL DIMENSIONS ARE IN METRES UNLESS OTHERWISE NOTED. LEVELS IN METRES.
2. DO NOT SCALE FROM THIS DRAWING. USE FIGURED DIMENSIONS ONLY.
3. VERIFY ALL DIMENSIONS ON SITE BEFORE STARTING ANY WORK.
4. READ WITH ALL RELEVANT STRUCTURAL AND MEP DRAWINGS AND SPECIFICATIONS.
5. COPYRIGHT OF THIS DRAWING IS RESERVED BY THE OFFICE.

KEY PLAN

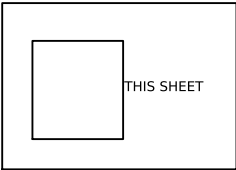

NORTH

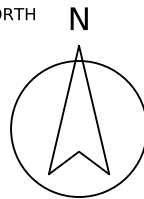

REVISIONS

REV	DATE	DESCRIPTION	BY
00	30/09/2026	FIRST ISSUE	--

PROJECT
AL-YARMOUK COMMERCIAL SOUQ

LOCATION
MOSUL, IRAQ

CLIENT / OWNER
CLIENT NAME

PROJECT No.
PRJ-2026-002

DRAWING TITLE

AERIAL VIEW
3D PERSPECTIVE

ROLE	NAME	SIGN.	DATE
DESIGNED	IBRAHIM MAHFOUDH		30/09/26
DRAWN	IBRAHIM MAHFOUDH		30/09/26
CHECKED	-		30/09/26
APPROVED	-		30/09/26

SCALE AS SHOWN	DATE 30/09/2026
-------------------	--------------------

PHASE DESIGN DEVELOPMENT	STATUS FOR REVIEW
-----------------------------	----------------------


DRAWING No.

A-001

SHEET

01


OF 21

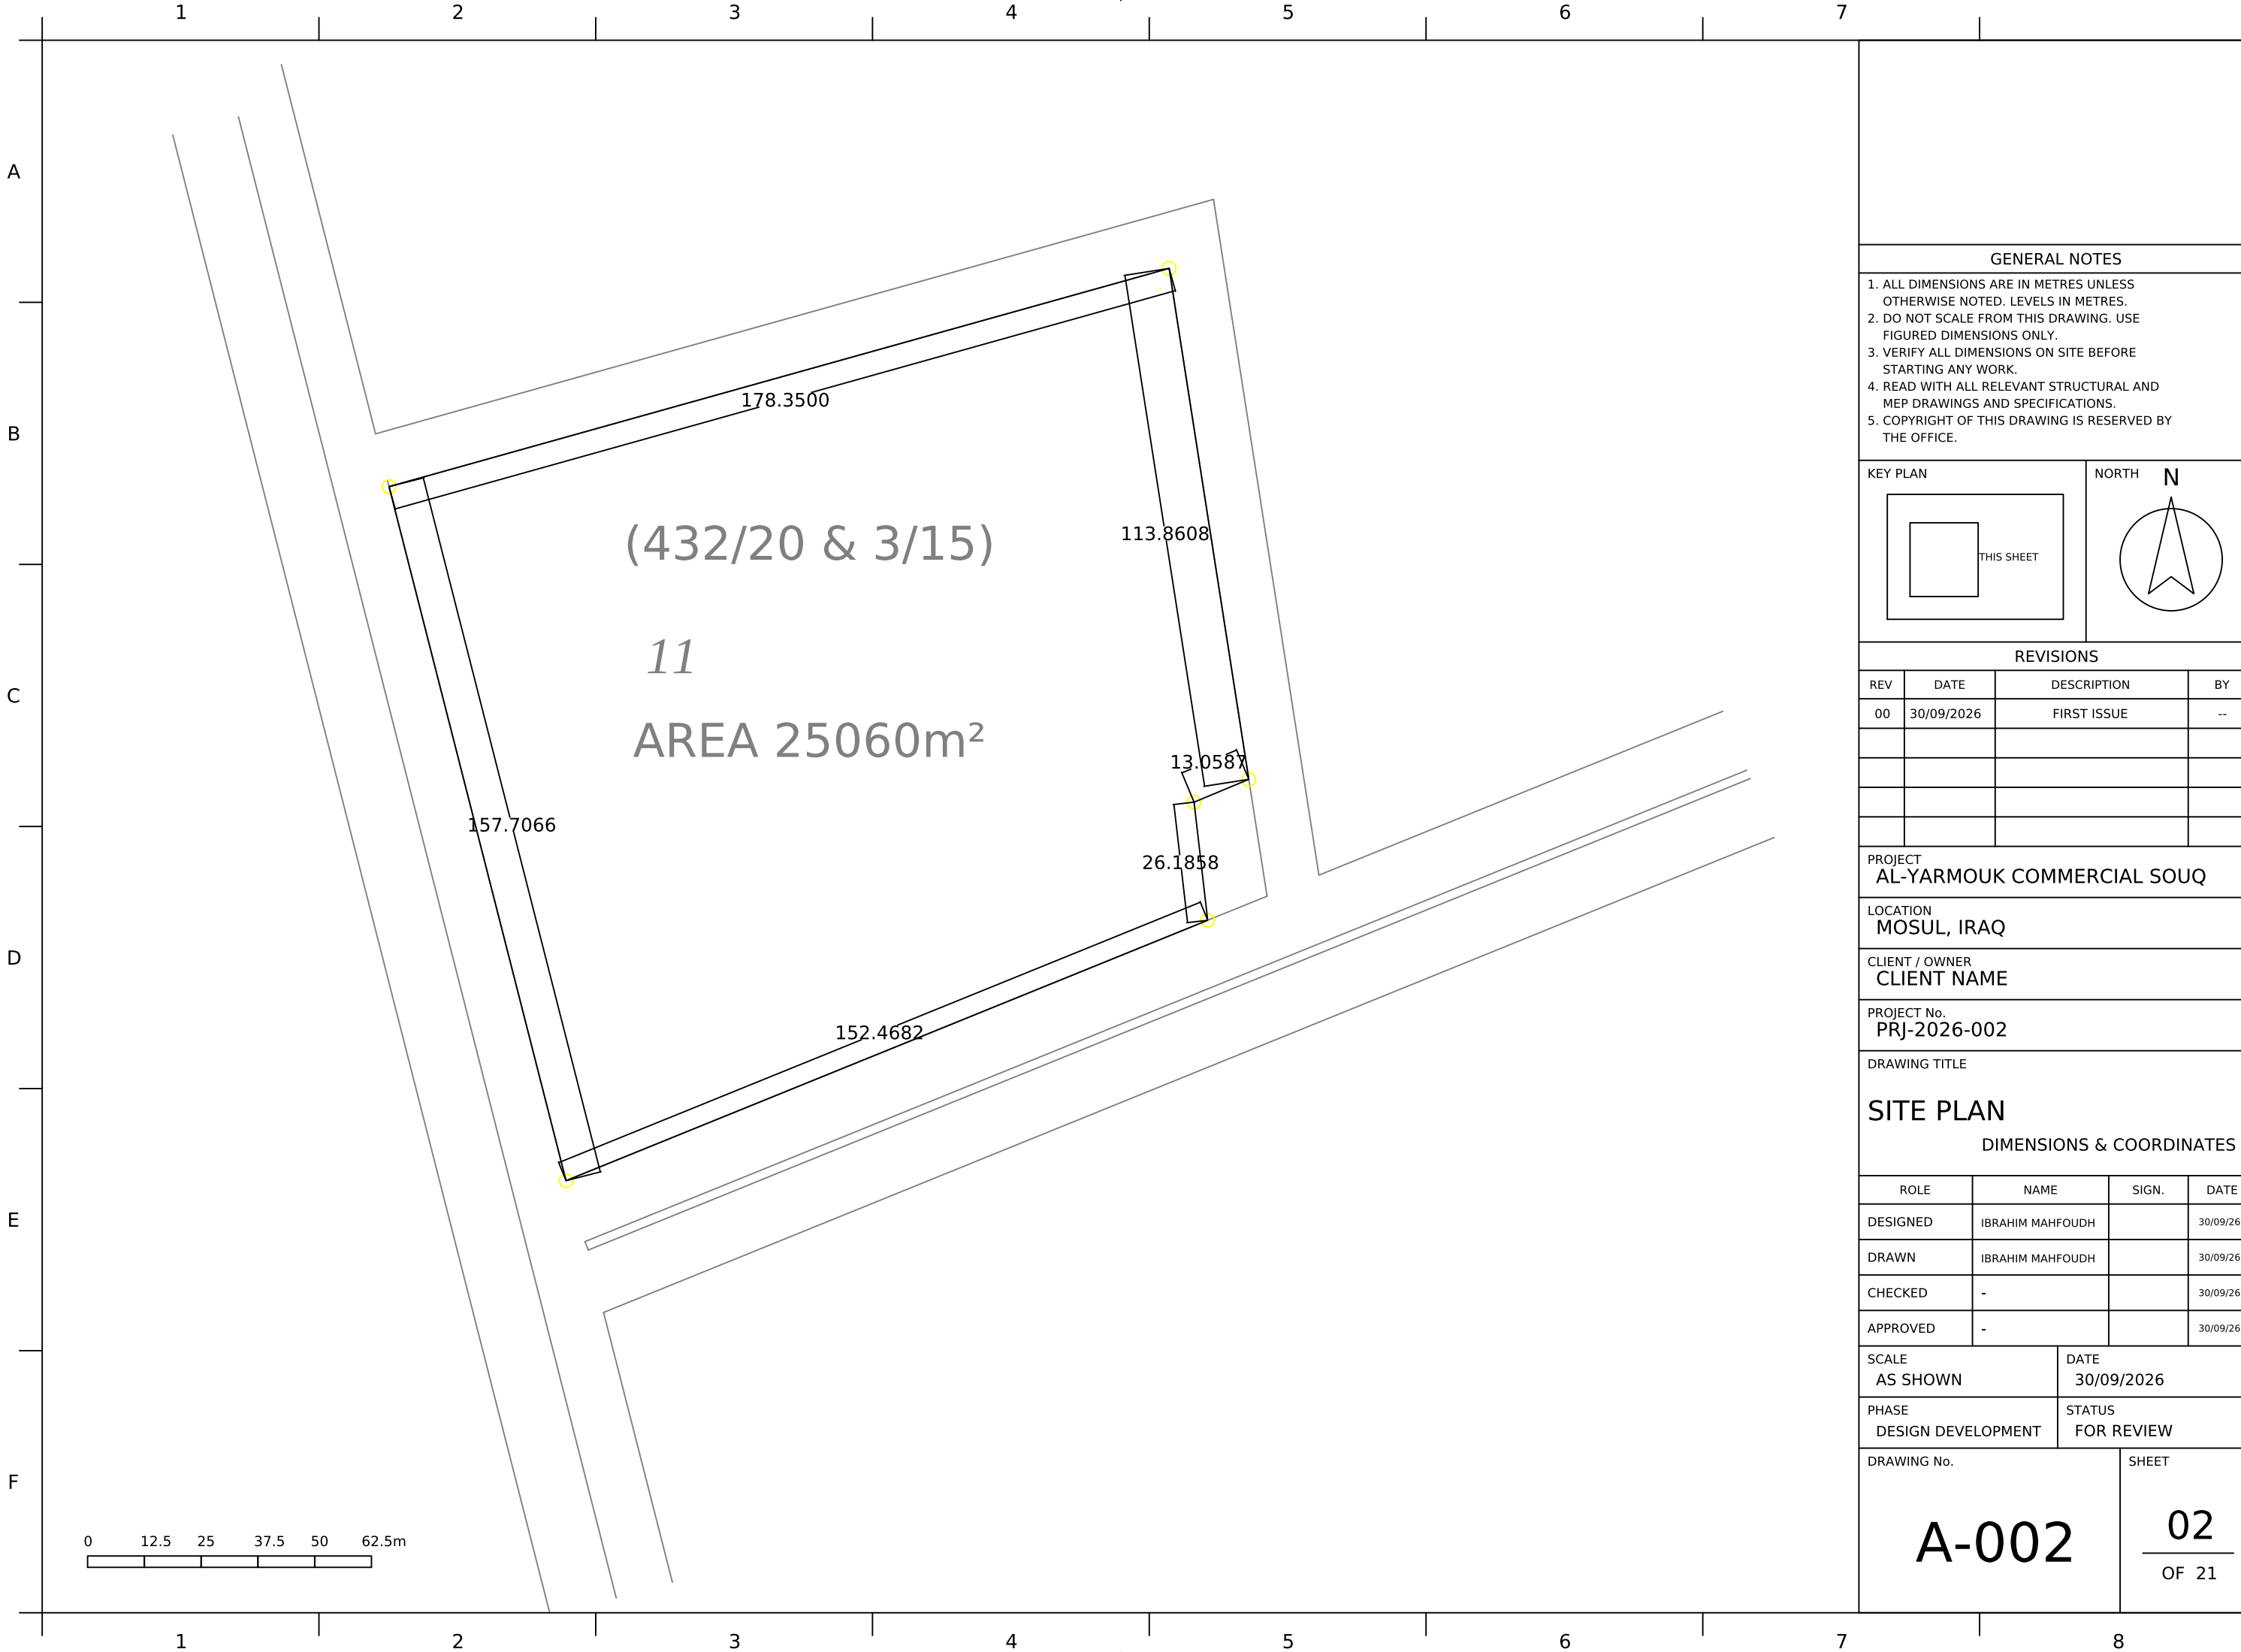

GENERAL NOTES

- 1. ALL DIMENSIONS ARE IN METRES UNLESS OTHERWISE NOTED. LEVELS IN METRES.
- 2. DO NOT SCALE FROM THIS DRAWING. USE FIGURED DIMENSIONS ONLY.
- 3. VERIFY ALL DIMENSIONS ON SITE BEFORE STARTING ANY WORK.
- 4. READ WITH ALL RELEVANT STRUCTURAL AND MEP DRAWINGS AND SPECIFICATIONS.
- 5. COPYRIGHT OF THIS DRAWING IS RESERVED BY THE OFFICE.


KEY PLAN

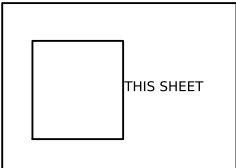

THIS SHEET

NORTH

N

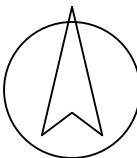

REVISIONS

REV	DATE	DESCRIPTION	BY
00	30/09/2026	FIRST ISSUE	--

PROJECT
AL-YARMOUK COMMERCIAL SOUQ

LOCATION
MOSUL, IRAQ

CLIENT / OWNER
CLIENT NAME

PROJECT No.
PRJ-2026-002

DRAWING TITLE

SITE PLAN
DIMENSIONS & COORDINATES

ROLE	NAME	SIGN.	DATE
DESIGNED	IBRAHIM MAHFOUDH		30/09/26
DRAWN	IBRAHIM MAHFOUDH		30/09/26
CHECKED	-		30/09/26
APPROVED	-		30/09/26

SCALE AS SHOWN	DATE 30/09/2026
-------------------	--------------------

PHASE DESIGN DEVELOPMENT	STATUS FOR REVIEW
-----------------------------	----------------------


DRAWING No.


A-002

SHEET

02

OF 21

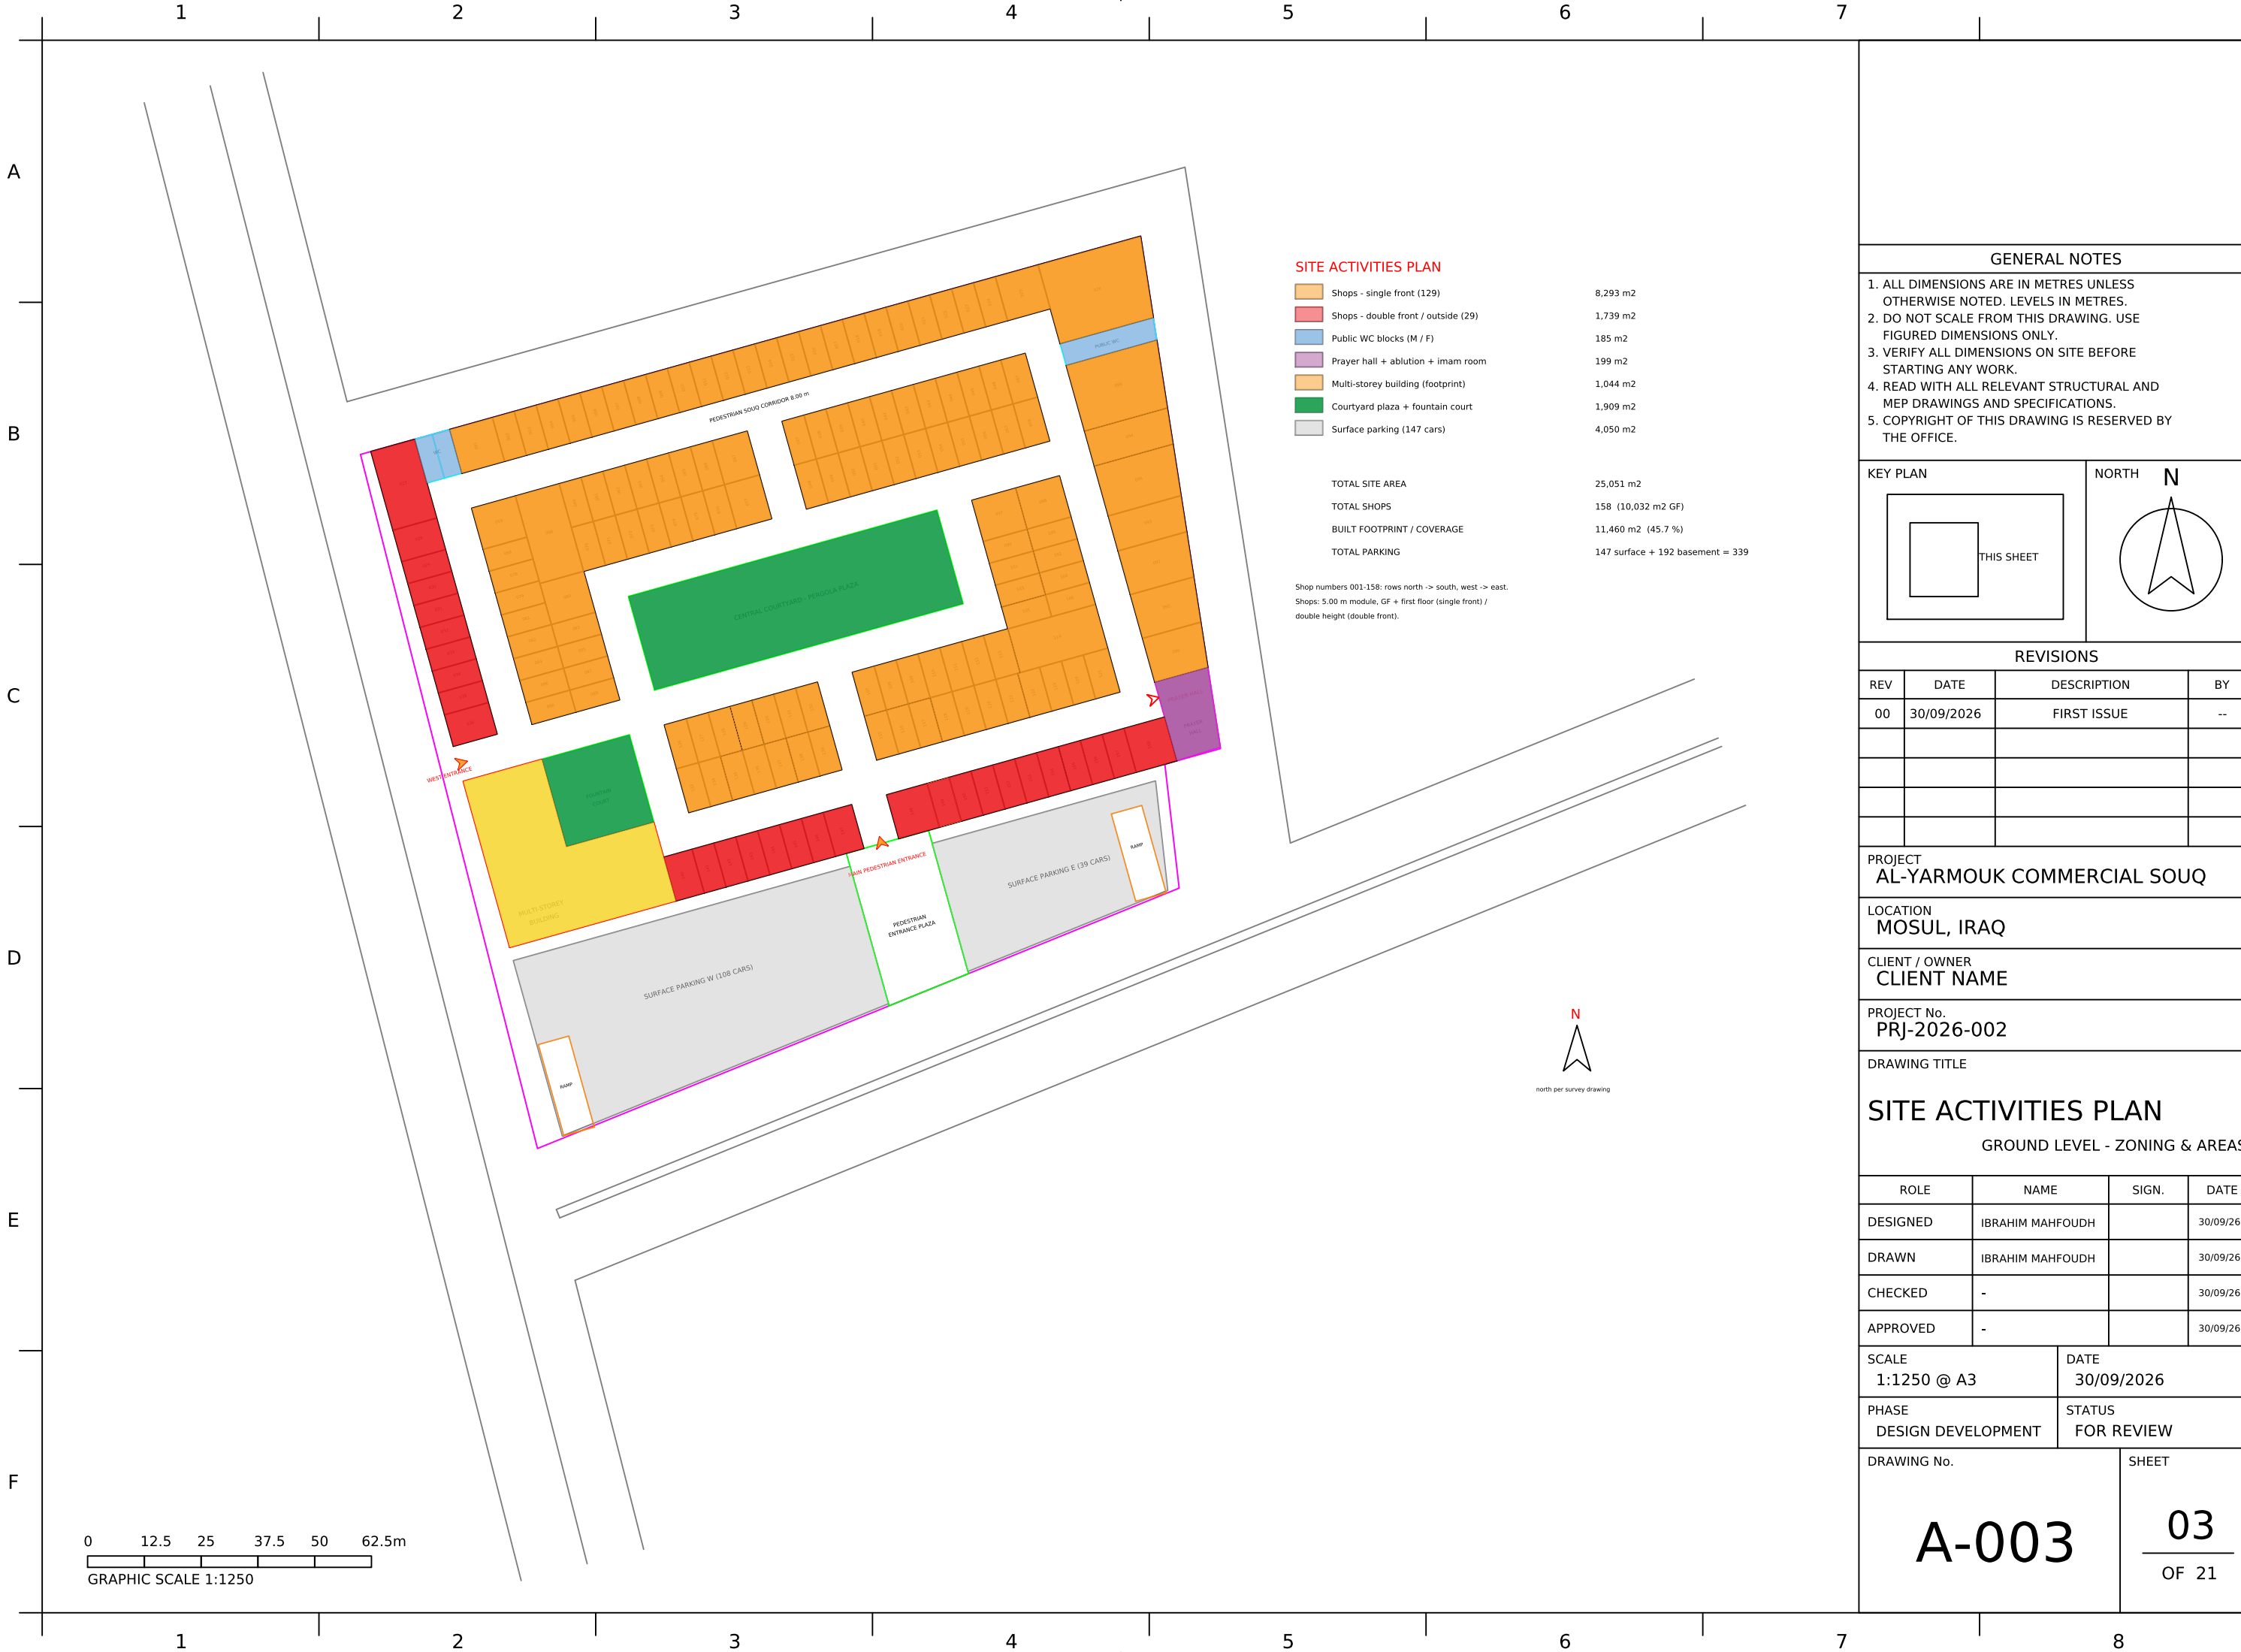

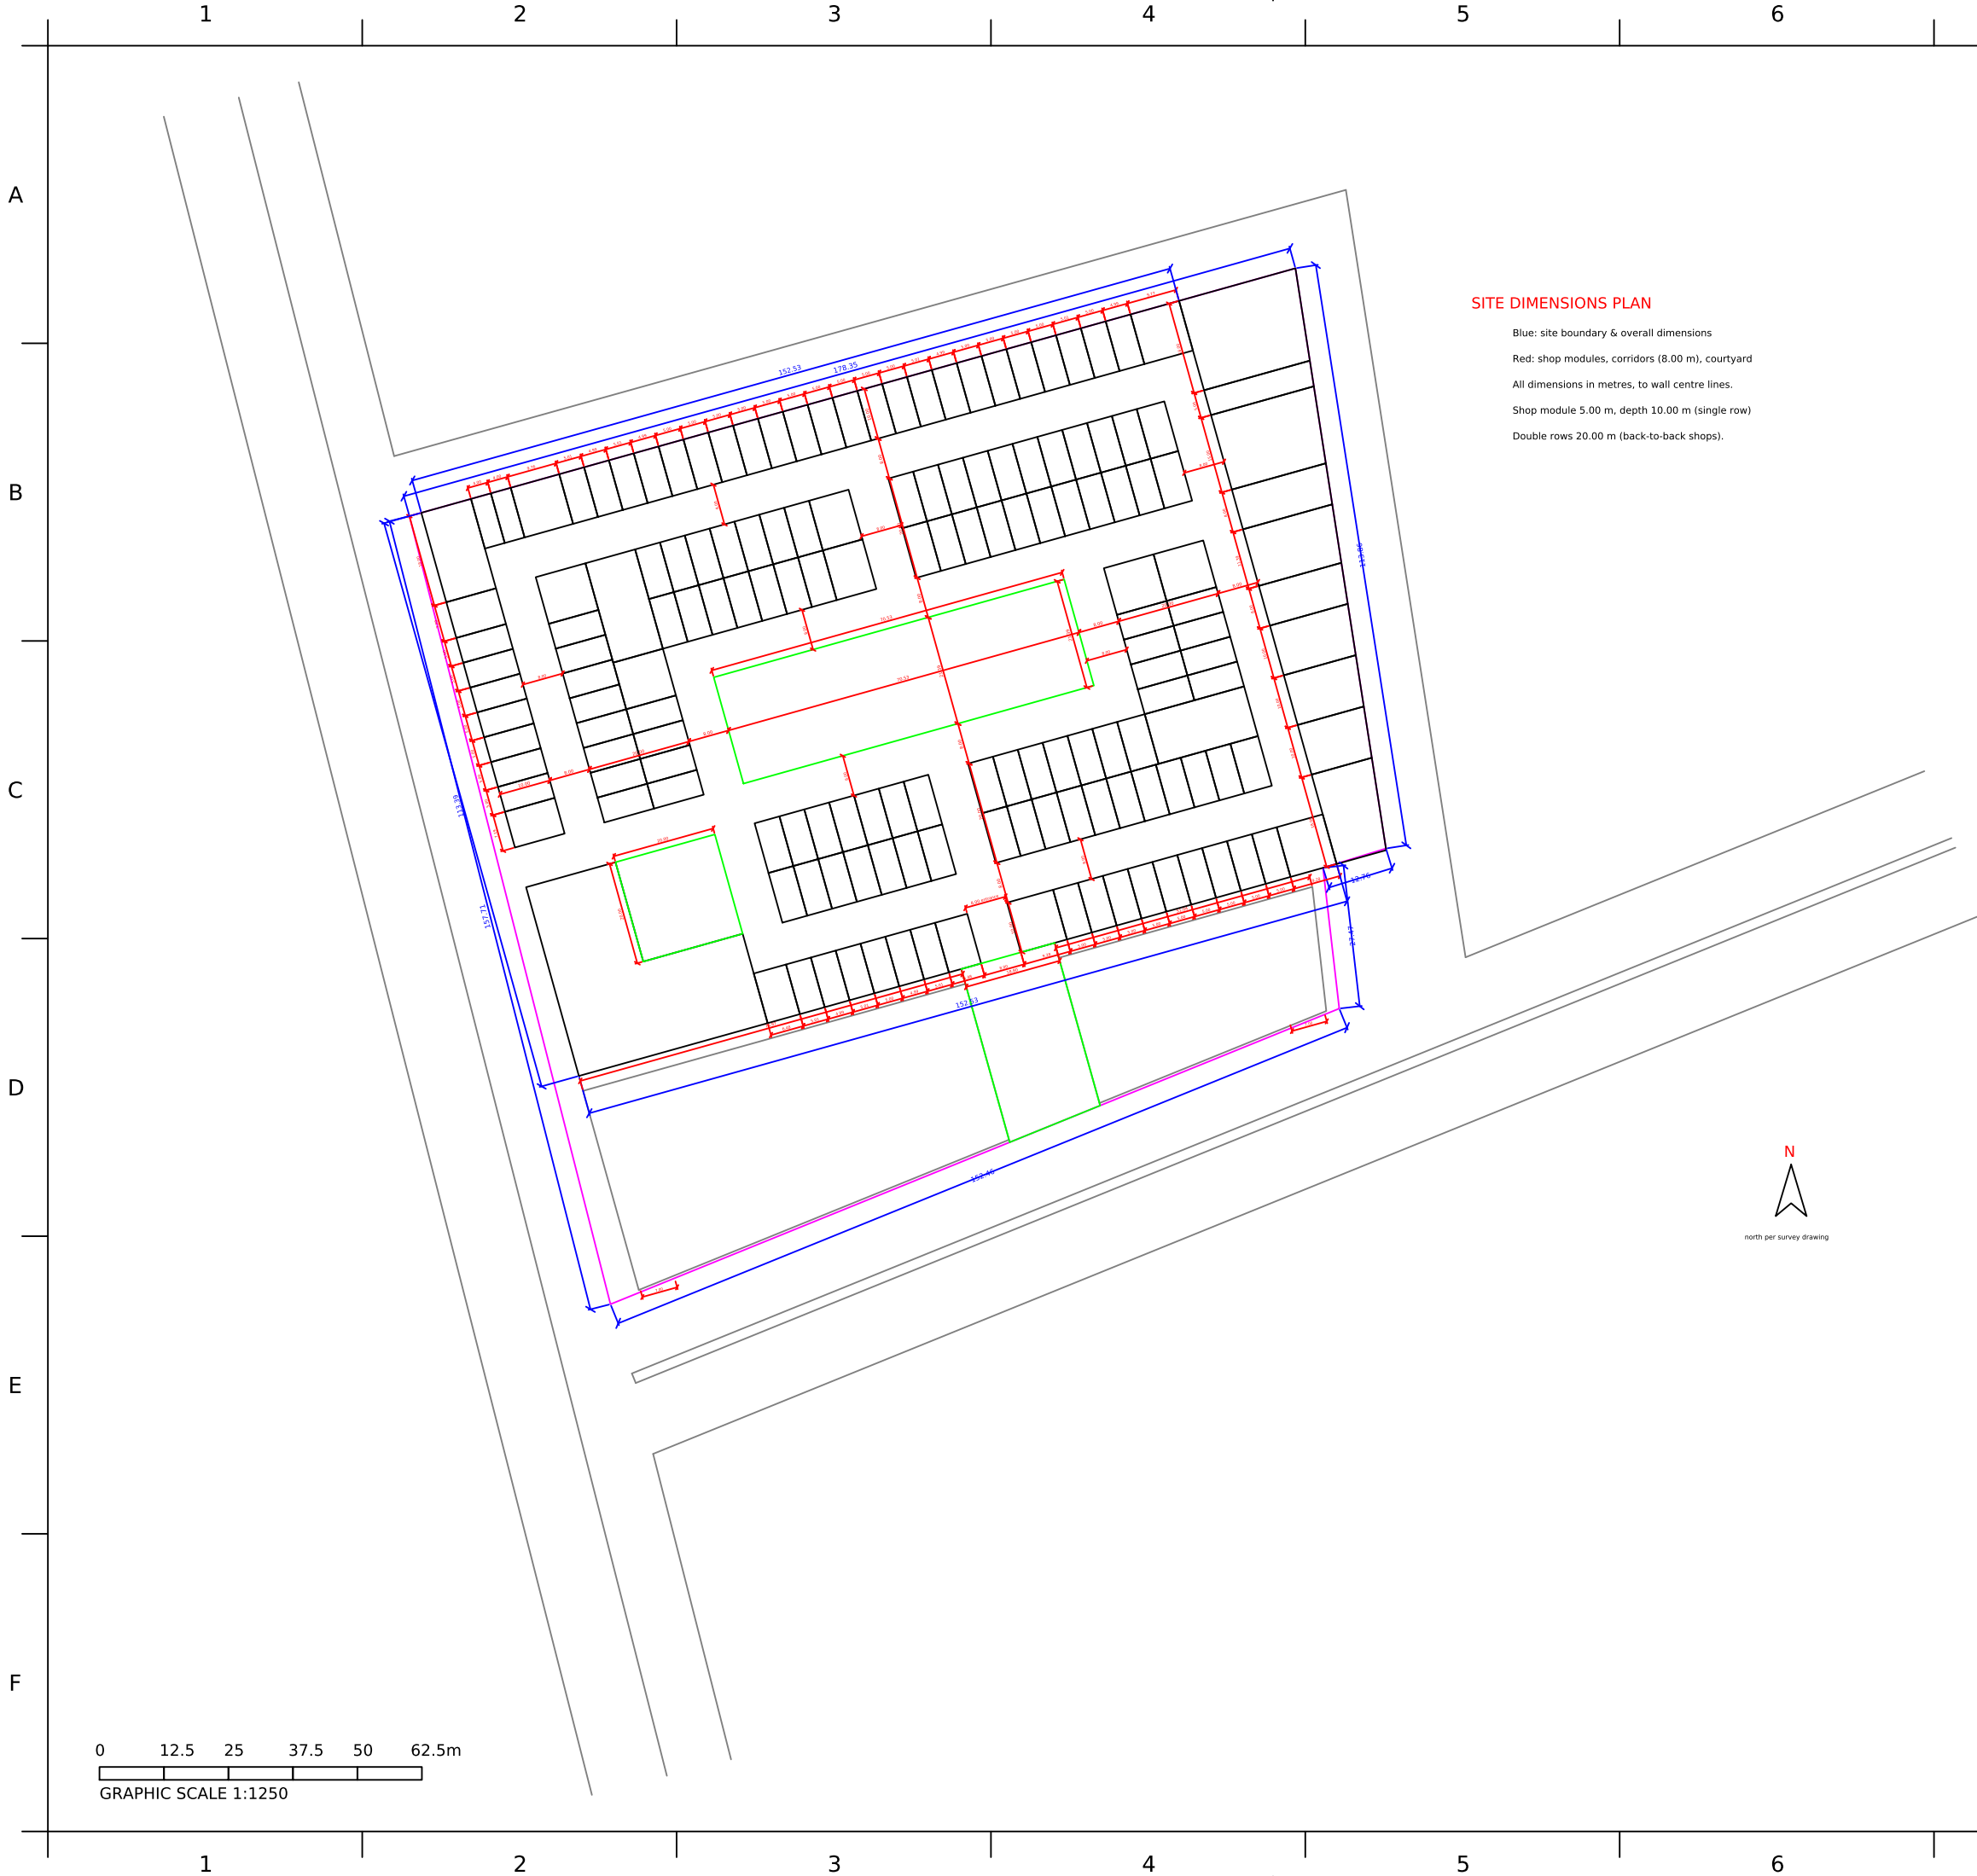


SITE DIMENSIONS PLAN

Blue: site boundary & overall dimensions
Red: shop modules, corridors (8.00 m), courtyard
All dimensions in metres, to wall centre lines.
Shop module 5.00 m, depth 10.00 m (single row)
Double rows 20.00 m (back-to-back shops).


GENERAL NOTES

- ALL DIMENSIONS ARE IN METRES UNLESS OTHERWISE NOTED. LEVELS IN METRES.
- DO NOT SCALE FROM THIS DRAWING. USE FIGURED DIMENSIONS ONLY.
- VERIFY ALL DIMENSIONS ON SITE BEFORE STARTING ANY WORK.
- READ WITH ALL RELEVANT STRUCTURAL AND MEP DRAWINGS AND SPECIFICATIONS.
- COPYRIGHT OF THIS DRAWING IS RESERVED BY THE OFFICE.

KEY PLAN

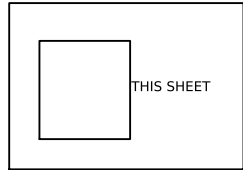

NORTH

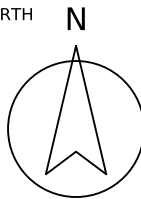

REVISIONS

REV	DATE	DESCRIPTION	BY
00	30/09/2026	FIRST ISSUE	--

PROJECT
AL-YARMOUK COMMERCIAL SOUQ

LOCATION
MOSUL, IRAQ

CLIENT / OWNER
CLIENT NAME

PROJECT No.
PRJ-2026-002

DRAWING TITLE

SITE DIMENSIONS PLAN
GROUND LEVEL

ROLE	NAME	SIGN.	DATE
DESIGNED	IBRAHIM MAHFOUDH		30/09/26
DRAWN	IBRAHIM MAHFOUDH		30/09/26
CHECKED	-		30/09/26
APPROVED	-		30/09/26


SCALE 1:1250 @ A3	DATE 30/09/2026
----------------------	--------------------

PHASE DESIGN DEVELOPMENT	STATUS FOR REVIEW
-----------------------------	----------------------

DRAWING No. A-005	SHEET 04 OF 21
--------------------------	--------------------------

BASEMENT (-1) CAR PARK PLAN | level -3.50


Parking stalls (2.50 x 5.00 m): 192
Gross basement area: 6,525 m2 (34.0 m2 / car)
Aisles 6.00 m two-way (green)
Two ramps 30 x 7 m, two-way, slope <= 15 %
Cores: stairs + lifts to the souq above (blue)
Services: shelter 60 m2, electrical room 20 m2, generator
Sprinklers & jet-fan ventilation to civil-defence requirements

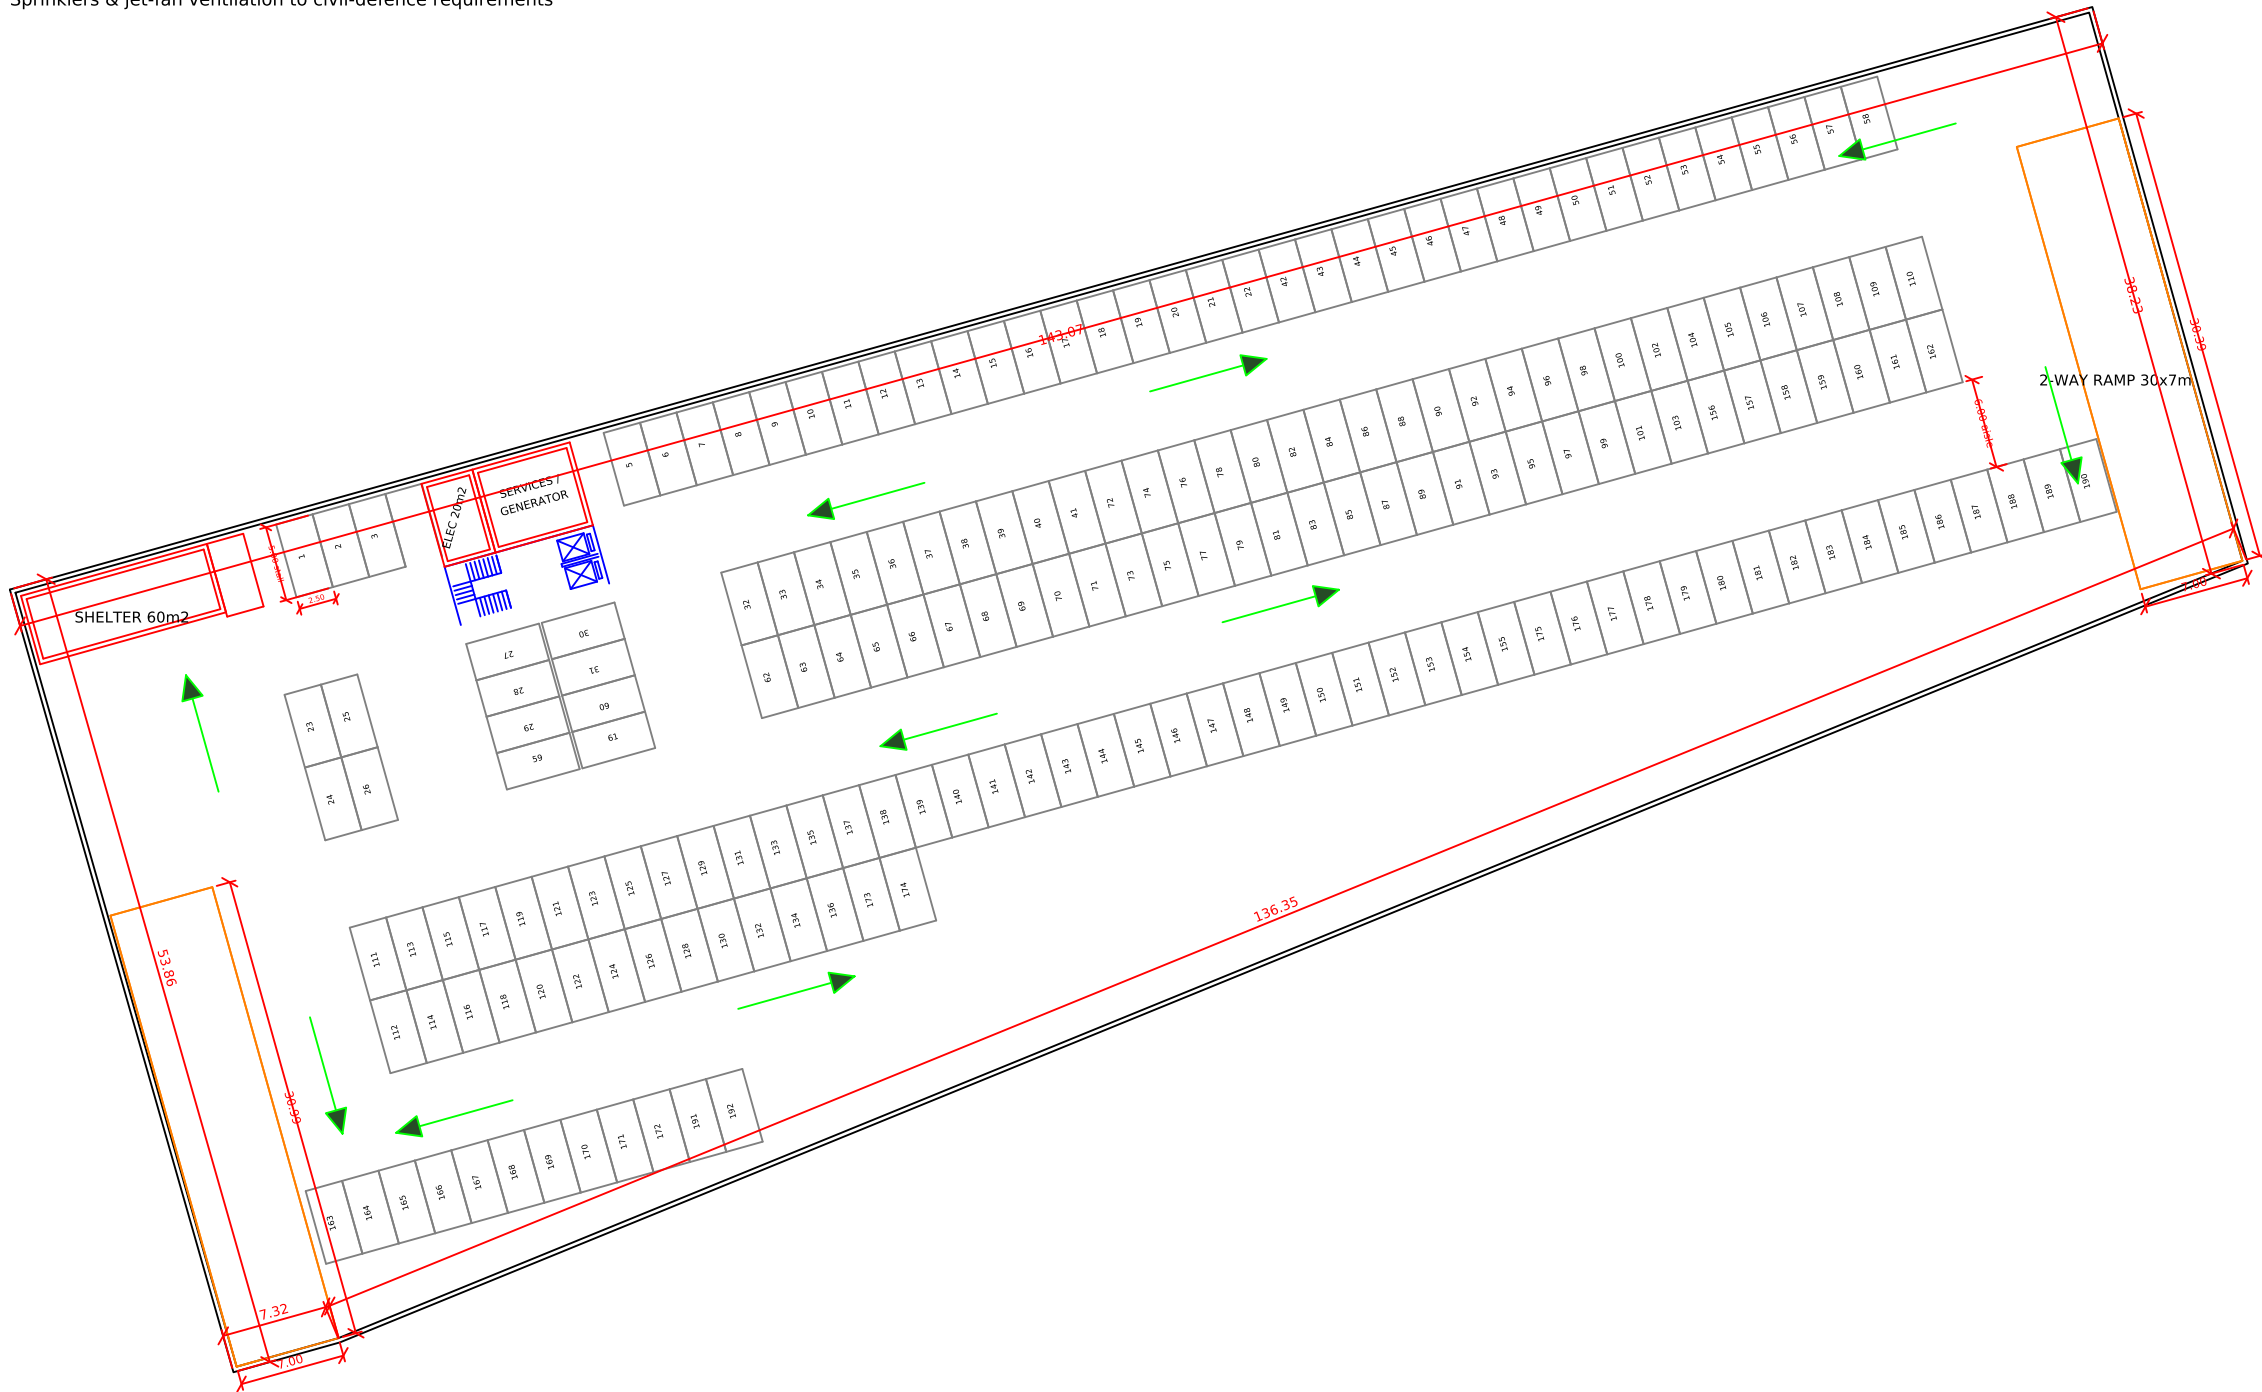


GENERAL NOTES

- ALL DIMENSIONS ARE IN METRES UNLESS OTHERWISE NOTED. LEVELS IN METRES.
- DO NOT SCALE FROM THIS DRAWING. USE FIGURED DIMENSIONS ONLY.
- VERIFY ALL DIMENSIONS ON SITE BEFORE STARTING ANY WORK.
- READ WITH ALL RELEVANT STRUCTURAL AND MEP DRAWINGS AND SPECIFICATIONS.
- COPYRIGHT OF THIS DRAWING IS RESERVED BY THE OFFICE.

KEY PLAN

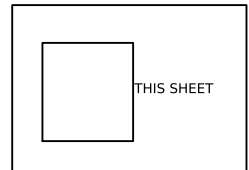

NORTH

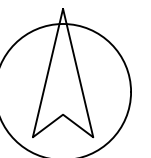

REVISIONS

REV	DATE	DESCRIPTION	BY
00	30/09/2026	FIRST ISSUE	--

PROJECT
AL-YARMOUK COMMERCIAL SOUQ

LOCATION
MOSUL, IRAQ

CLIENT / OWNER
CLIENT NAME

PROJECT No.
PRJ-2026-002

DRAWING TITLE
BASEMENT CAR PARK
LEVEL -3.50 (192 CARS)

ROLE	NAME	SIGN.	DATE
DESIGNED	IBRAHIM MAHFOUDH		30/09/26
DRAWN	IBRAHIM MAHFOUDH		30/09/26
CHECKED	-		30/09/26
APPROVED	-		30/09/26

SCALE
1:500 @ A3


DATE
30/09/2026

PHASE
DESIGN DEVELOPMENT

STATUS
FOR REVIEW

DRAWING No.
A-004


SHEET
05
OF 21

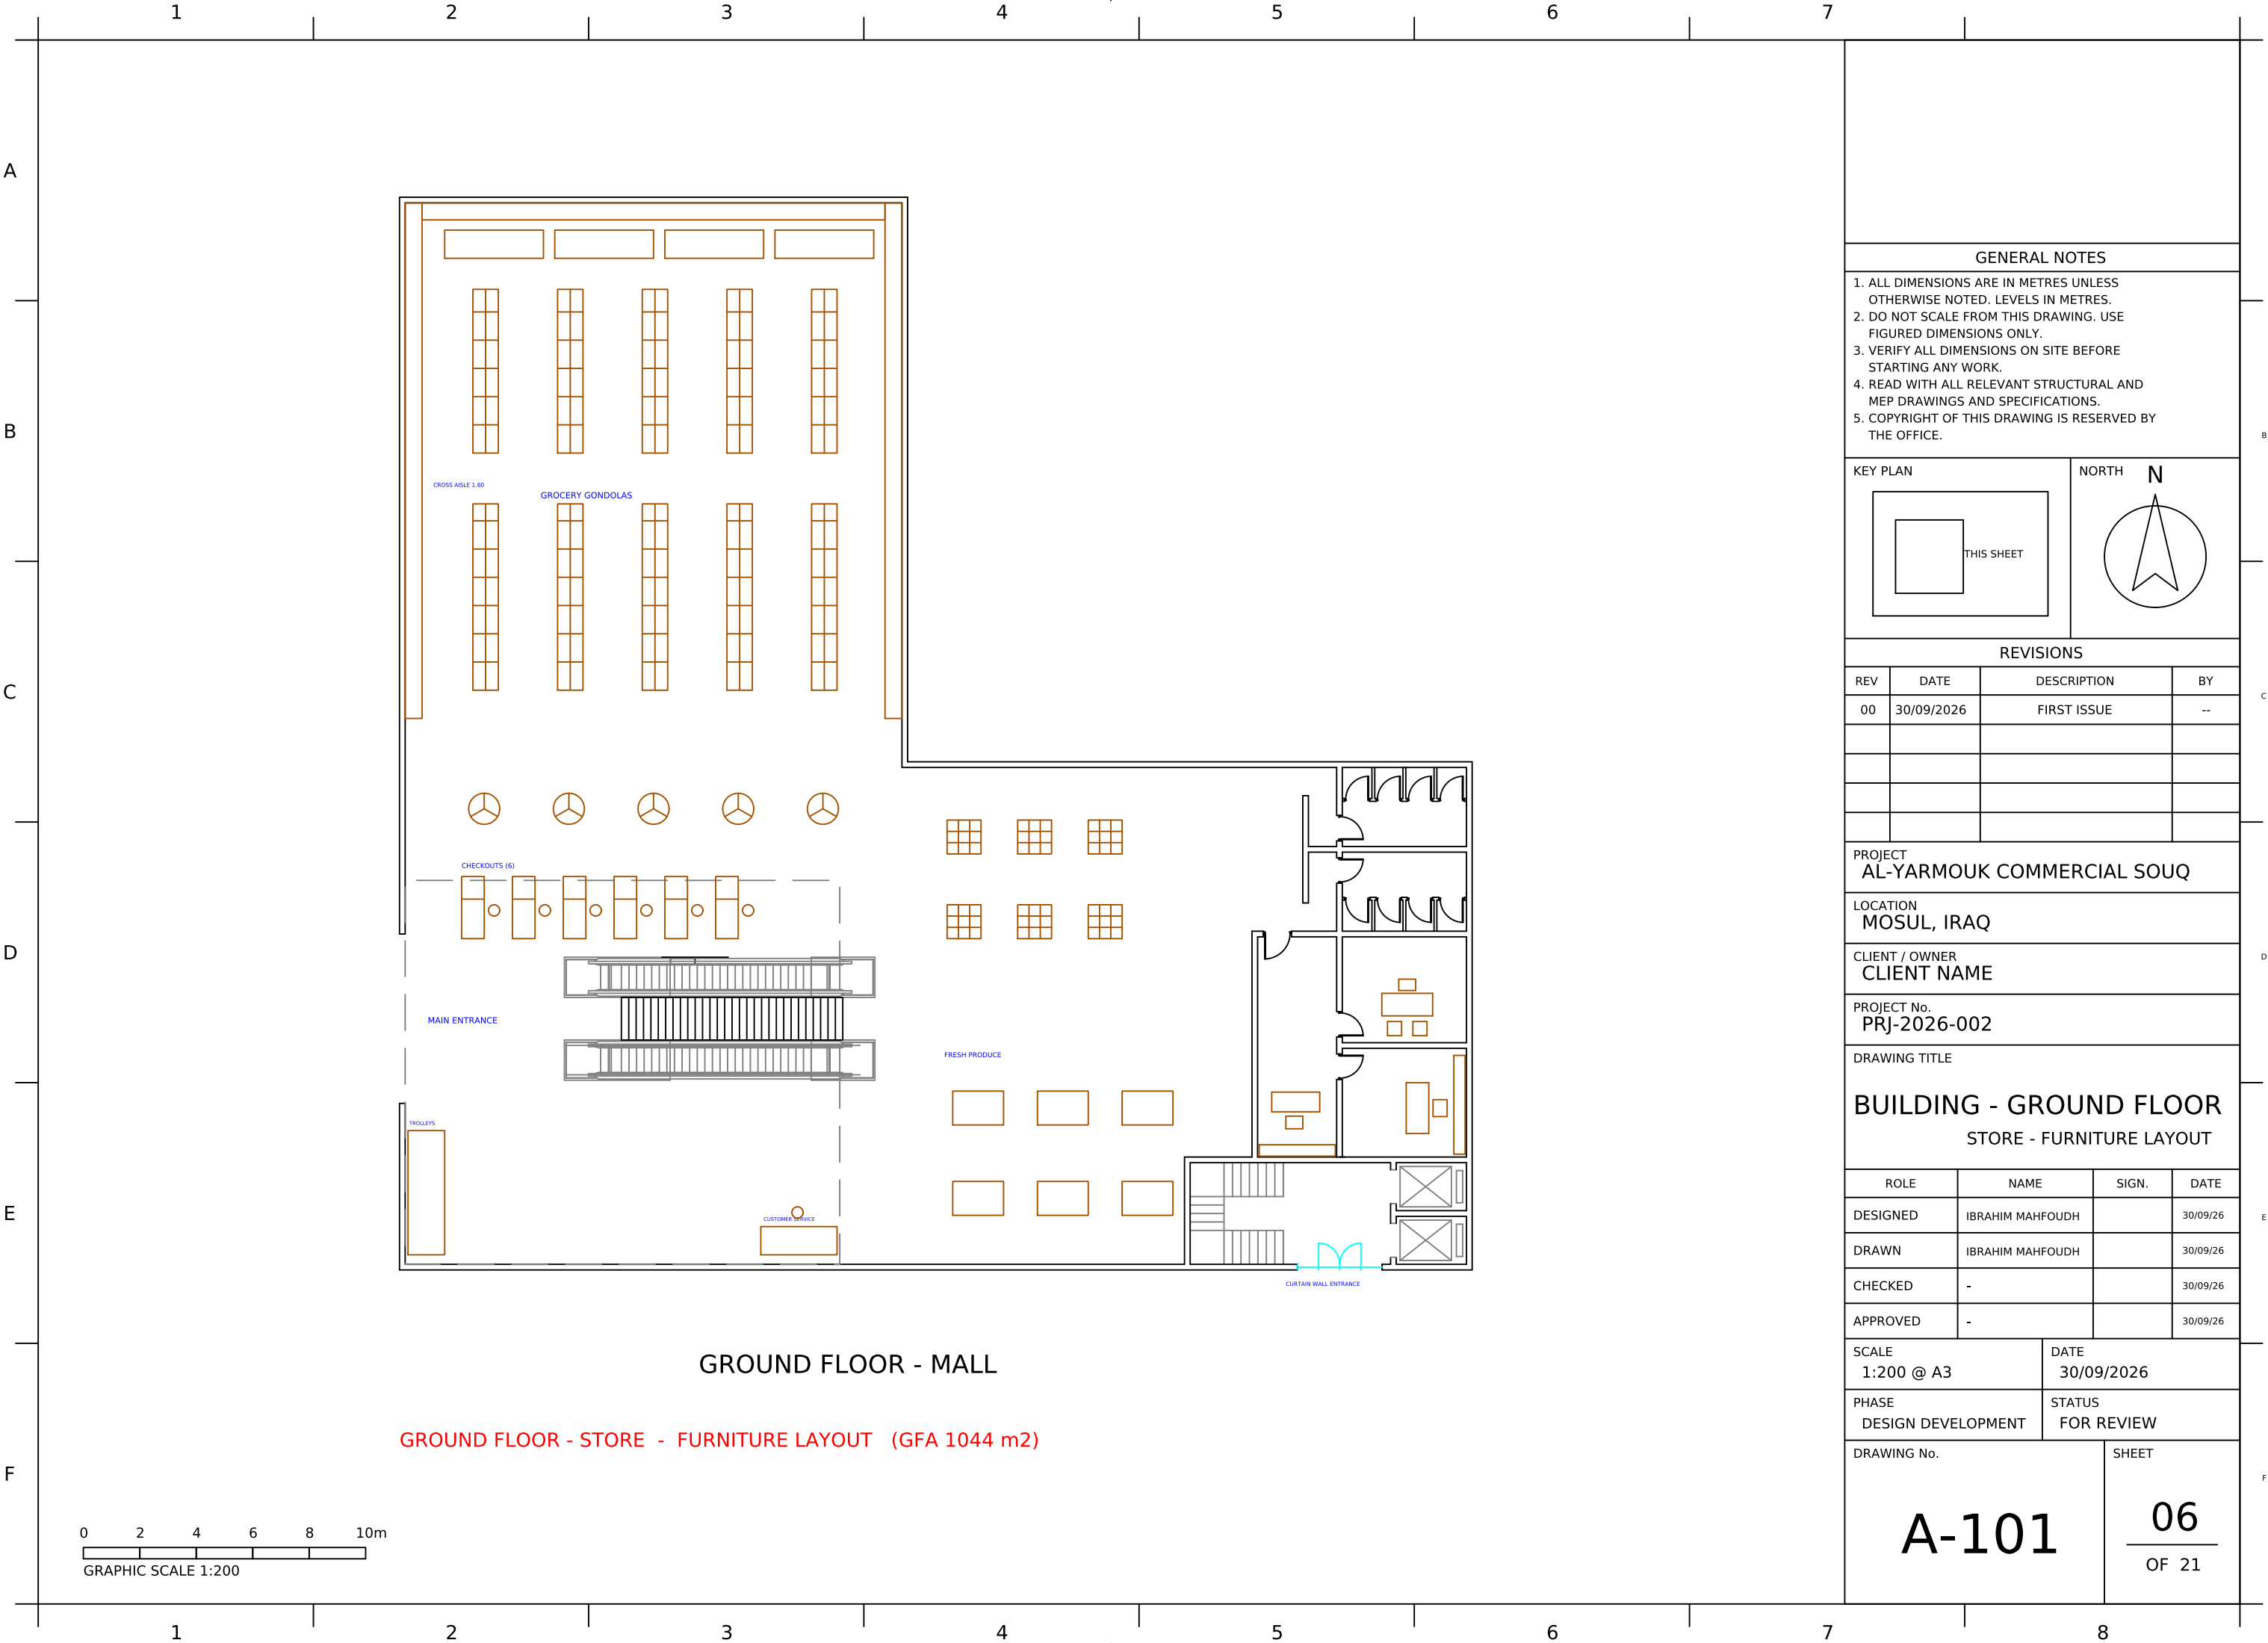

GENERAL NOTES

- 1. ALL DIMENSIONS ARE IN METRES UNLESS OTHERWISE NOTED. LEVELS IN METRES.
- 2. DO NOT SCALE FROM THIS DRAWING. USE FIGURED DIMENSIONS ONLY.
- 3. VERIFY ALL DIMENSIONS ON SITE BEFORE STARTING ANY WORK.
- 4. READ WITH ALL RELEVANT STRUCTURAL AND MEP DRAWINGS AND SPECIFICATIONS.
- 5. COPYRIGHT OF THIS DRAWING IS RESERVED BY THE OFFICE.

KEY PLAN

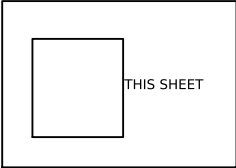

NORTH



REVISIONS

REV	DATE	DESCRIPTION	BY
00	30/09/2026	FIRST ISSUE	--

PROJECT
AL-YARMOUK COMMERCIAL SOUQ

LOCATION
MOSUL, IRAQ

CLIENT / OWNER
CLIENT NAME

PROJECT No.
PRJ-2026-002


DRAWING TITLE
BUILDING - GROUND FLOOR
STORE - FURNITURE LAYOUT

ROLE	NAME	SIGN.	DATE
DESIGNED	IBRAHIM MAHFOUDH		30/09/26
DRAWN	IBRAHIM MAHFOUDH		30/09/26
CHECKED	-		30/09/26
APPROVED	-		30/09/26

SCALE 1:200 @ A3	DATE 30/09/2026
---------------------	--------------------

PHASE DESIGN DEVELOPMENT	STATUS FOR REVIEW
-----------------------------	----------------------


DRAWING No. A-101	SHEET 06 OF 21
-----------------------------	-----------------------------

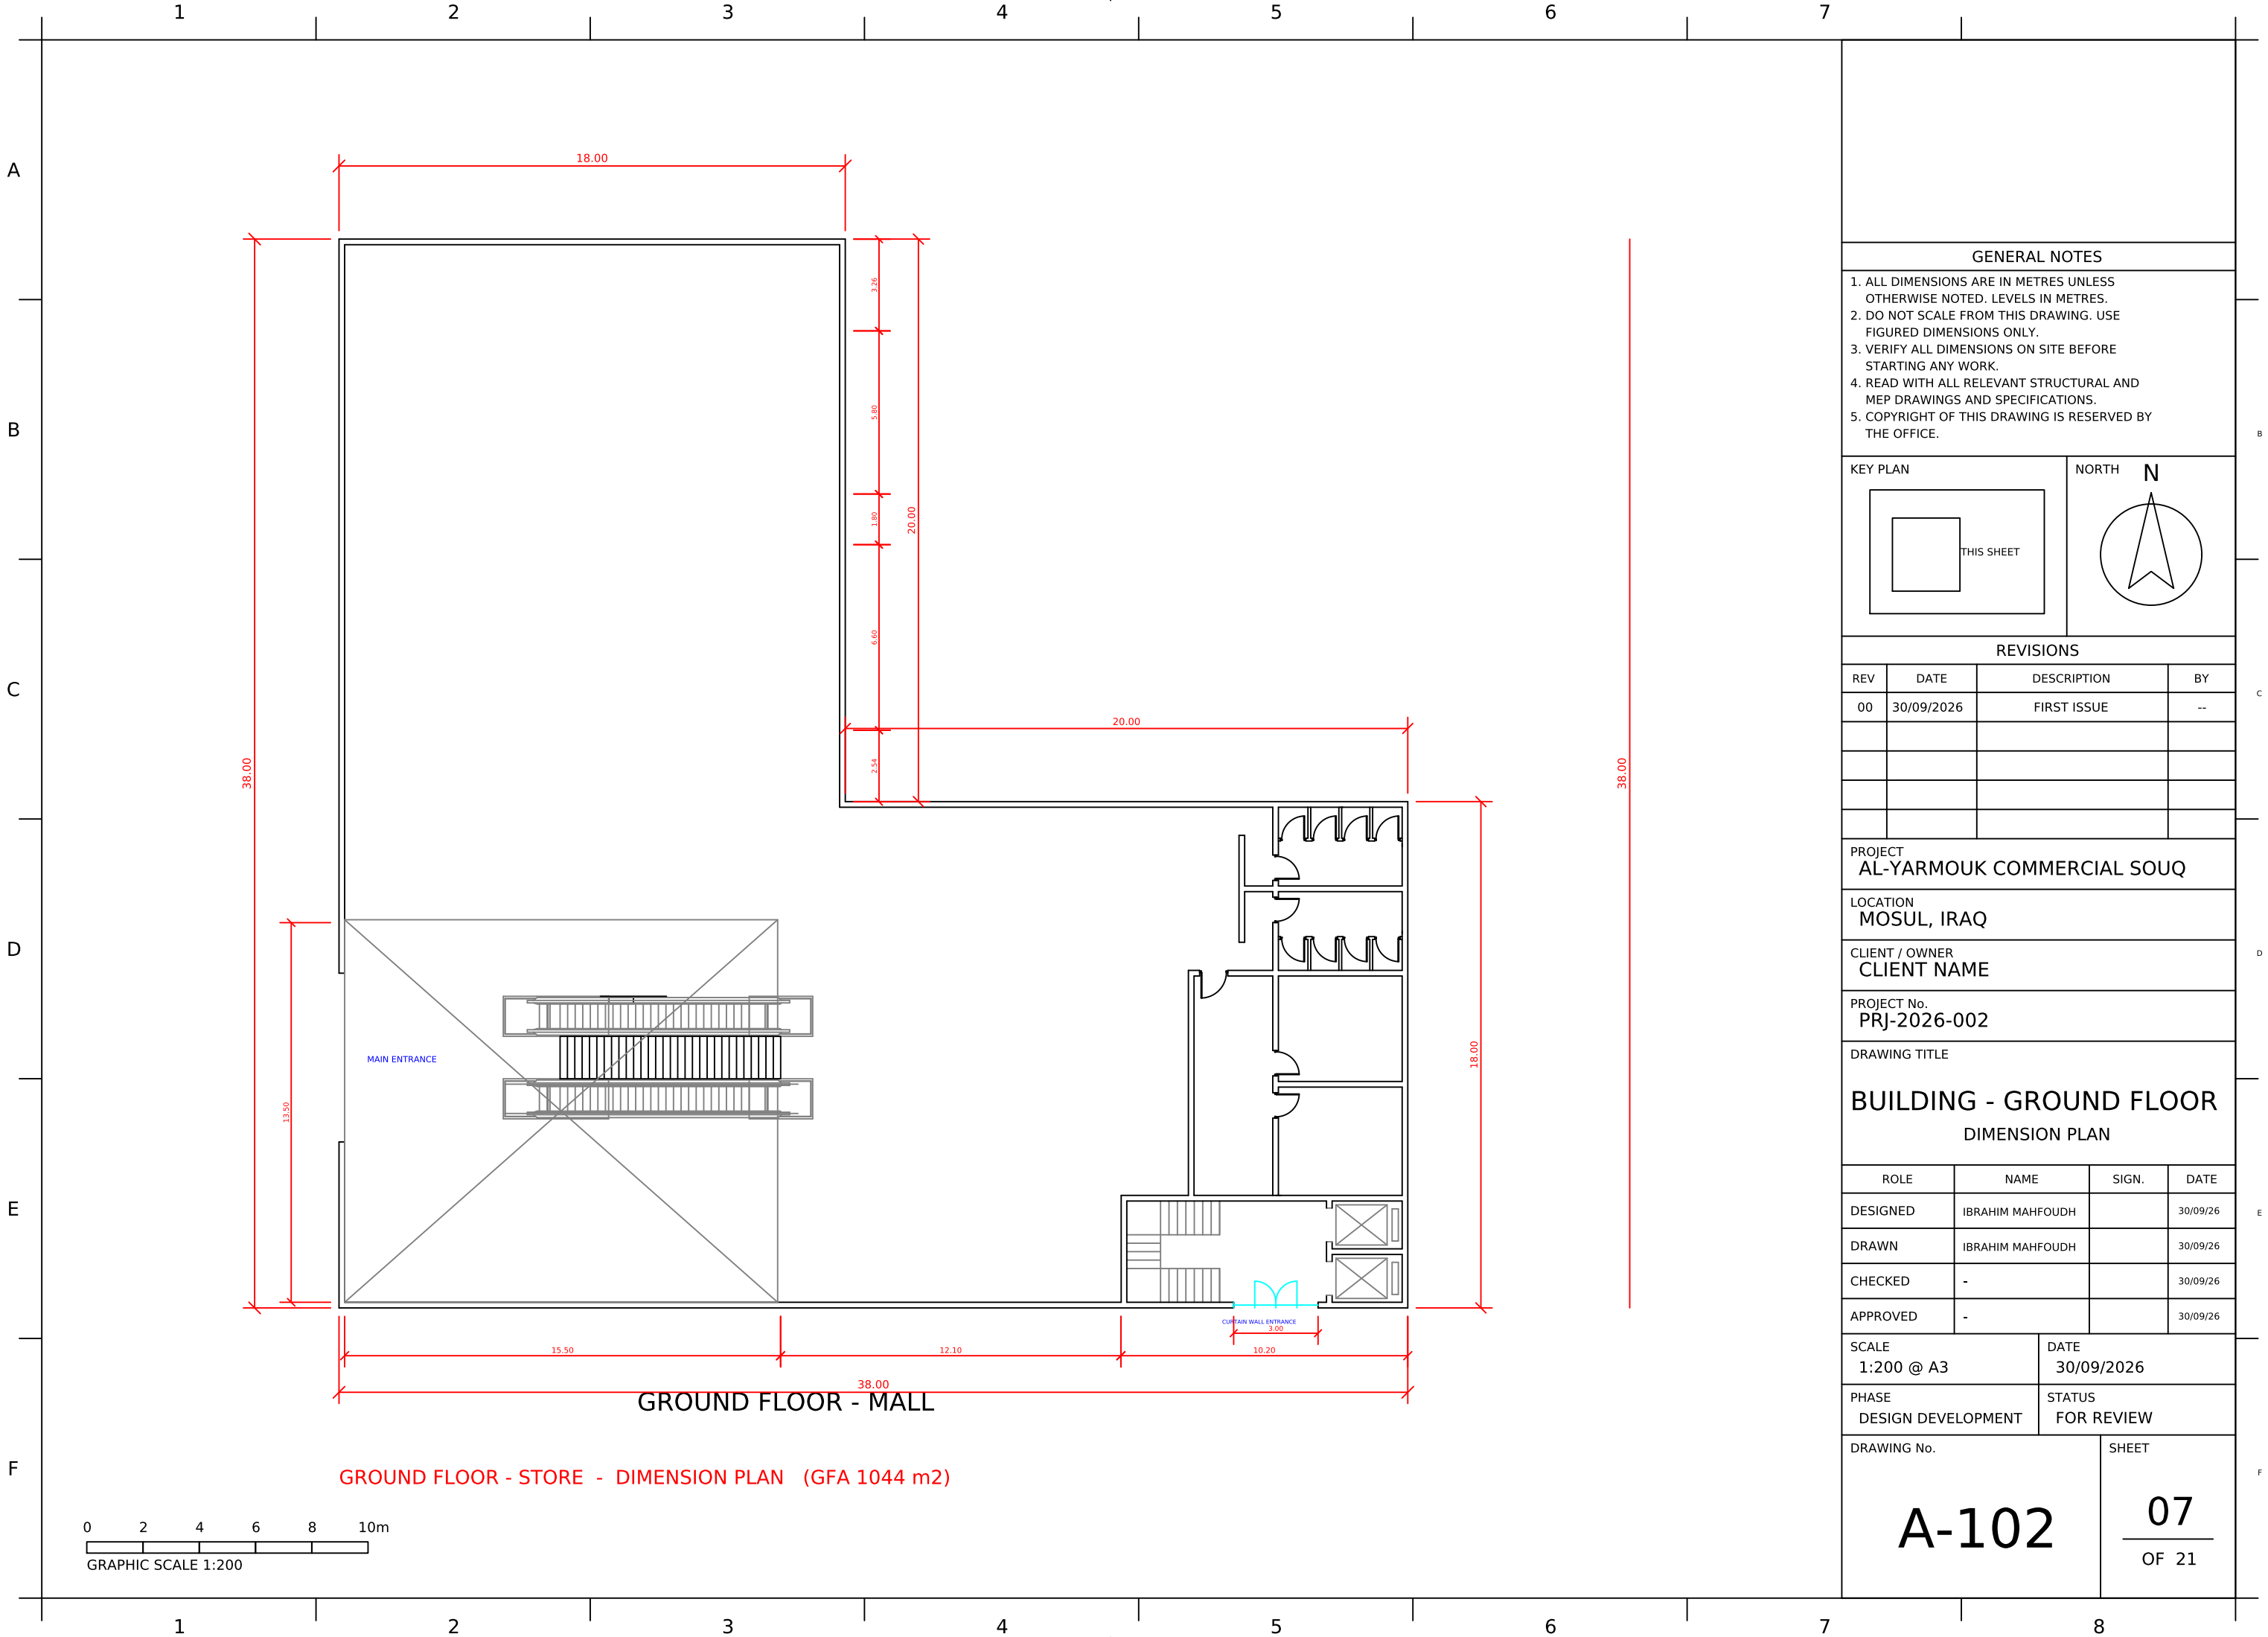

GENERAL NOTES

1. ALL DIMENSIONS ARE IN METRES UNLESS OTHERWISE NOTED. LEVELS IN METRES.
2. DO NOT SCALE FROM THIS DRAWING. USE FIGURED DIMENSIONS ONLY.
3. VERIFY ALL DIMENSIONS ON SITE BEFORE STARTING ANY WORK.
4. READ WITH ALL RELEVANT STRUCTURAL AND MEP DRAWINGS AND SPECIFICATIONS.
5. COPYRIGHT OF THIS DRAWING IS RESERVED BY THE OFFICE.

KEY PLAN

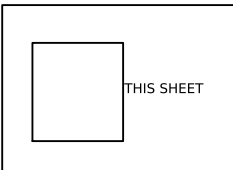

NORTH



REVISIONS

REV	DATE	DESCRIPTION	BY
00	30/09/2026	FIRST ISSUE	--

PROJECT
AL-YARMOUK COMMERCIAL SOUQ

LOCATION
MOSUL, IRAQ

CLIENT / OWNER
CLIENT NAME

PROJECT No.
PRJ-2026-002

DRAWING TITLE
BUILDING - GROUND FLOOR
DIMENSION PLAN

ROLE	NAME	SIGN.	DATE
DESIGNED	IBRAHIM MAHFOUDH		30/09/26
DRAWN	IBRAHIM MAHFOUDH		30/09/26
CHECKED	-		30/09/26
APPROVED	-		30/09/26

SCALE
1:200 @ A3

DATE
30/09/2026

PHASE
DESIGN DEVELOPMENT


STATUS
FOR REVIEW

DRAWING No.

A-102

SHEET


07
OF 21

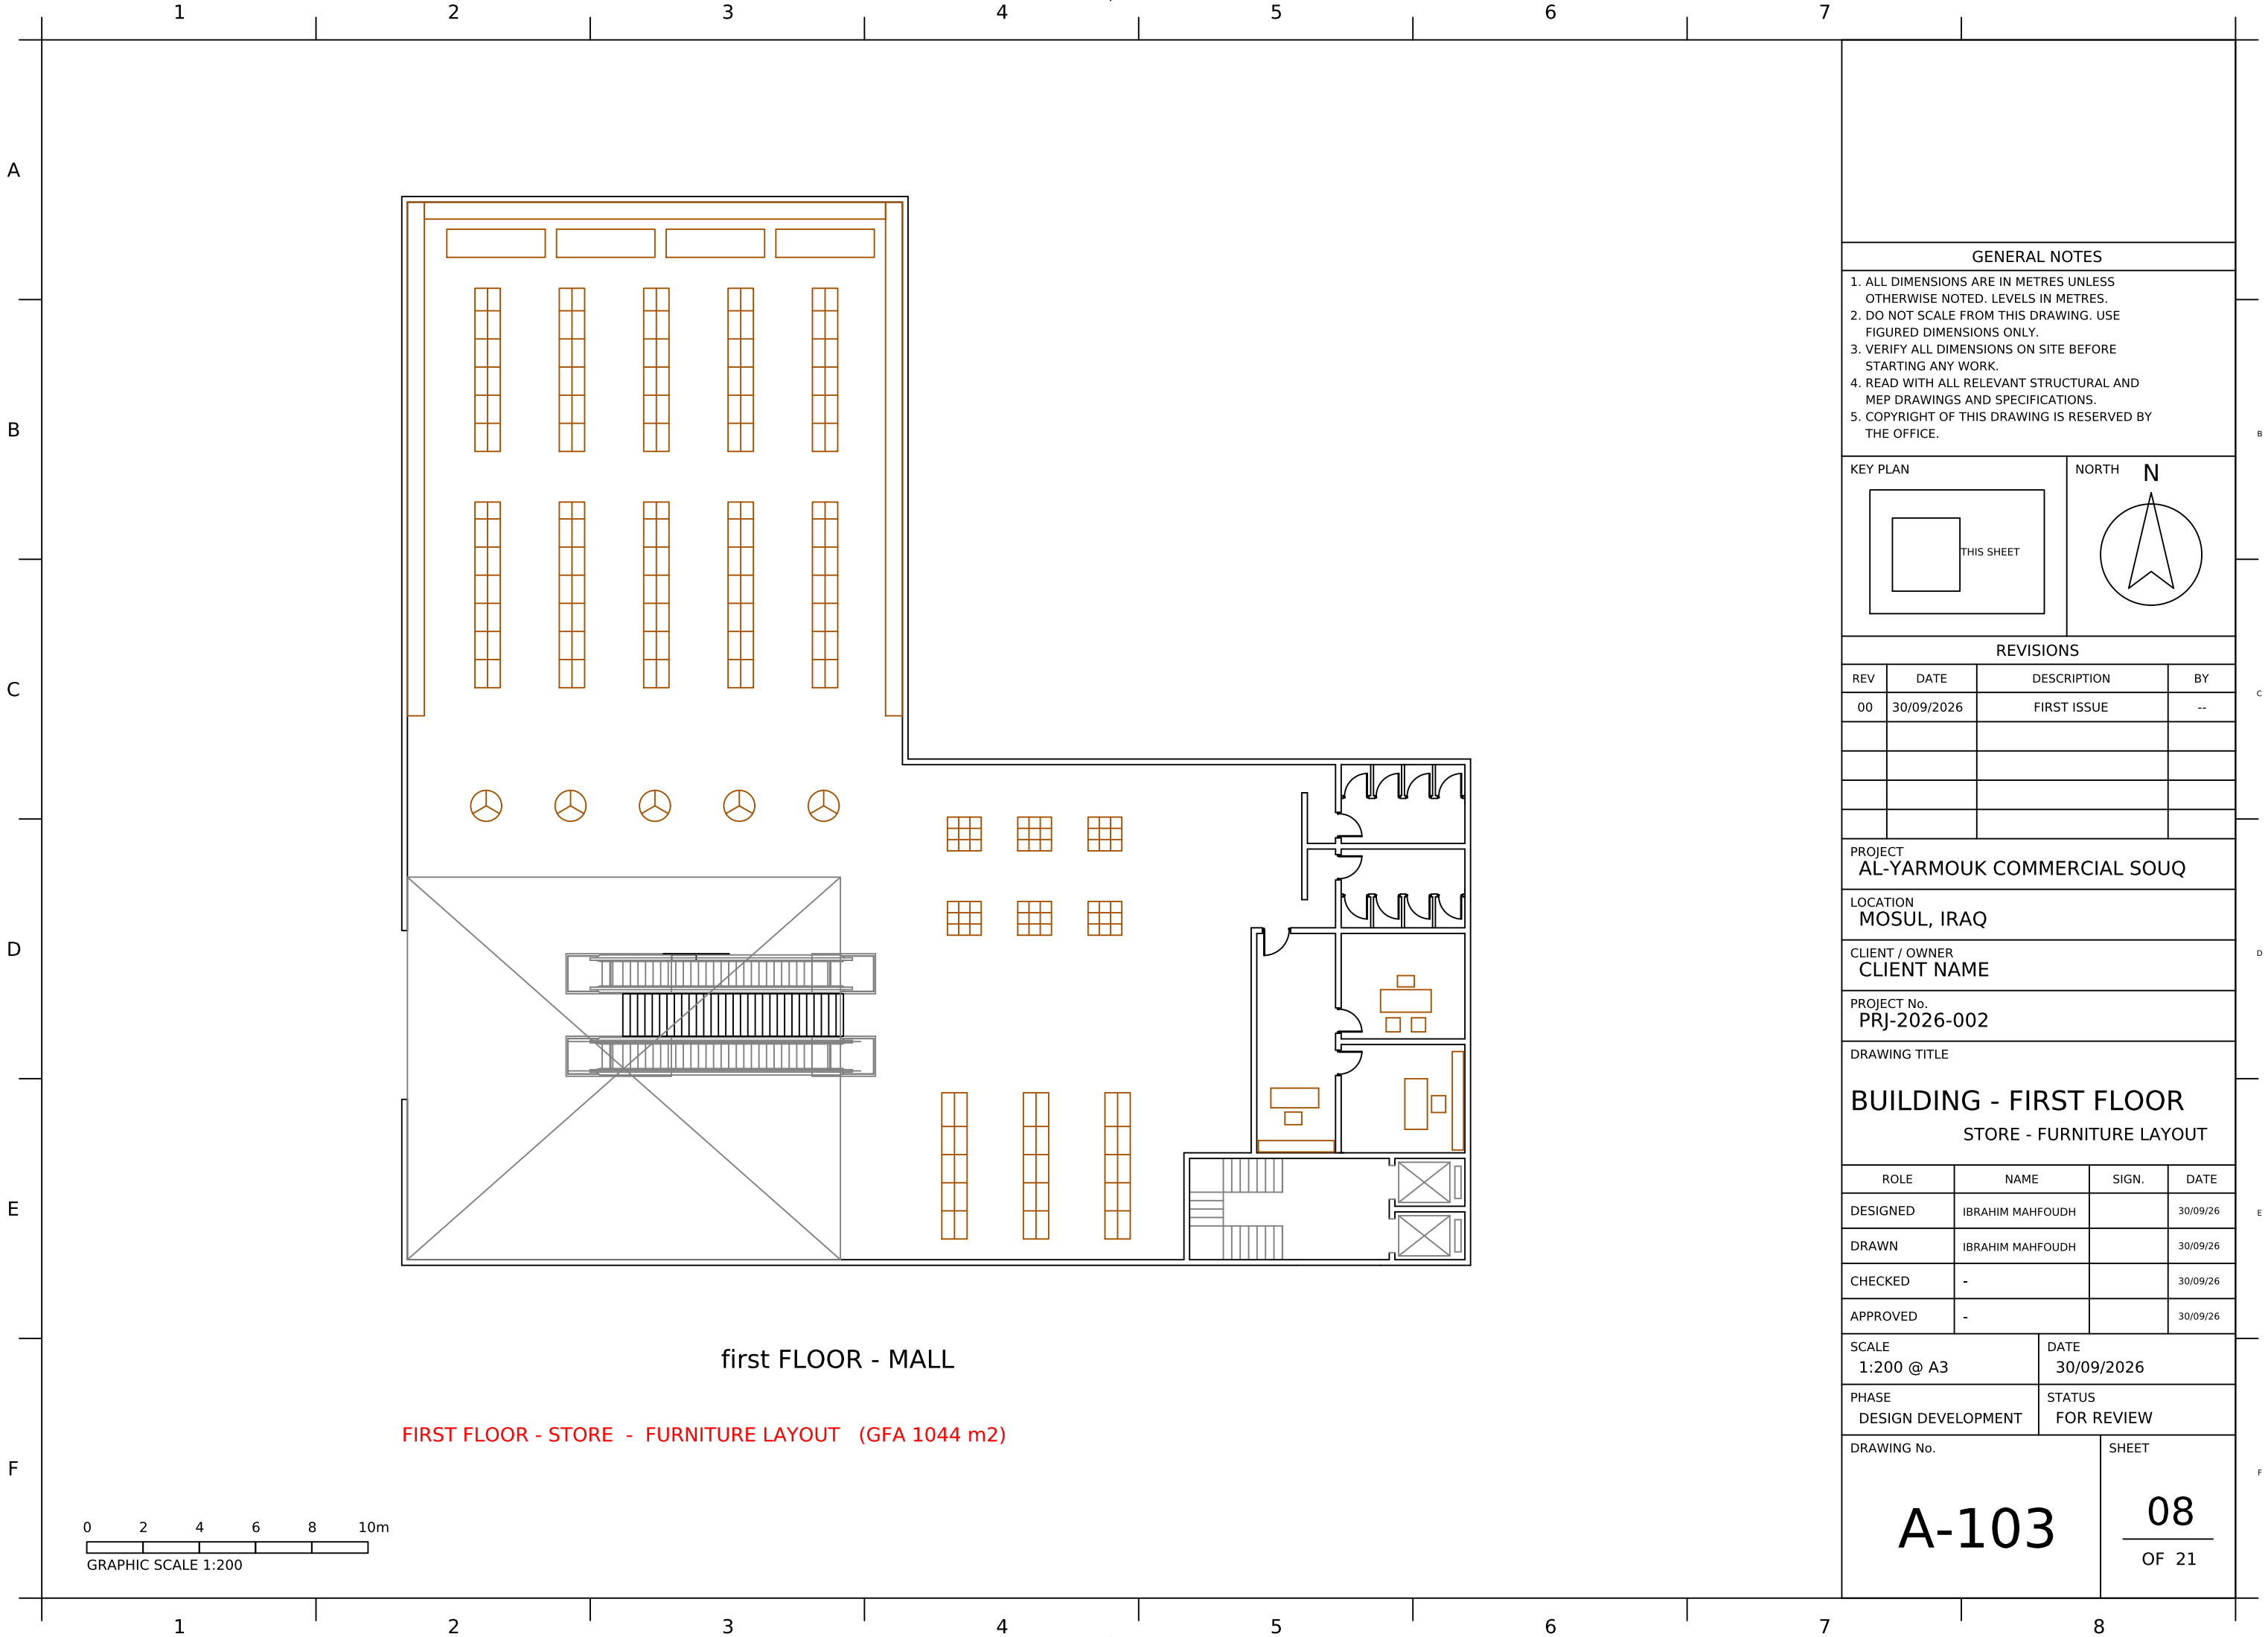

GENERAL NOTES


1. ALL DIMENSIONS ARE IN METRES UNLESS OTHERWISE NOTED. LEVELS IN METRES.
2. DO NOT SCALE FROM THIS DRAWING. USE FIGURED DIMENSIONS ONLY.
3. VERIFY ALL DIMENSIONS ON SITE BEFORE STARTING ANY WORK.
4. READ WITH ALL RELEVANT STRUCTURAL AND MEP DRAWINGS AND SPECIFICATIONS.
5. COPYRIGHT OF THIS DRAWING IS RESERVED BY THE OFFICE.

KEY PLAN

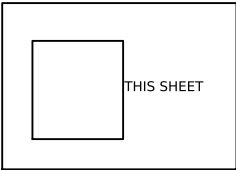

NORTH

N

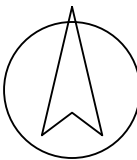

REVISIONS

REV	DATE	DESCRIPTION	BY
00	30/09/2026	FIRST ISSUE	--

PROJECT
AL-YARMOUK COMMERCIAL SOUQ

LOCATION
MOSUL, IRAQ

CLIENT / OWNER
CLIENT NAME

PROJECT No.
PRJ-2026-002

DRAWING TITLE
BUILDING - FIRST FLOOR
STORE - FURNITURE LAYOUT

ROLE	NAME	SIGN.	DATE
DESIGNED	IBRAHIM MAHFOUDH		30/09/26
DRAWN	IBRAHIM MAHFOUDH		30/09/26
CHECKED	-		30/09/26
APPROVED	-		30/09/26

SCALE
1:200 @ A3

DATE
30/09/2026

PHASE
DESIGN DEVELOPMENT

STATUS
FOR REVIEW


DRAWING No.

A-103

SHEET

08


OF 21

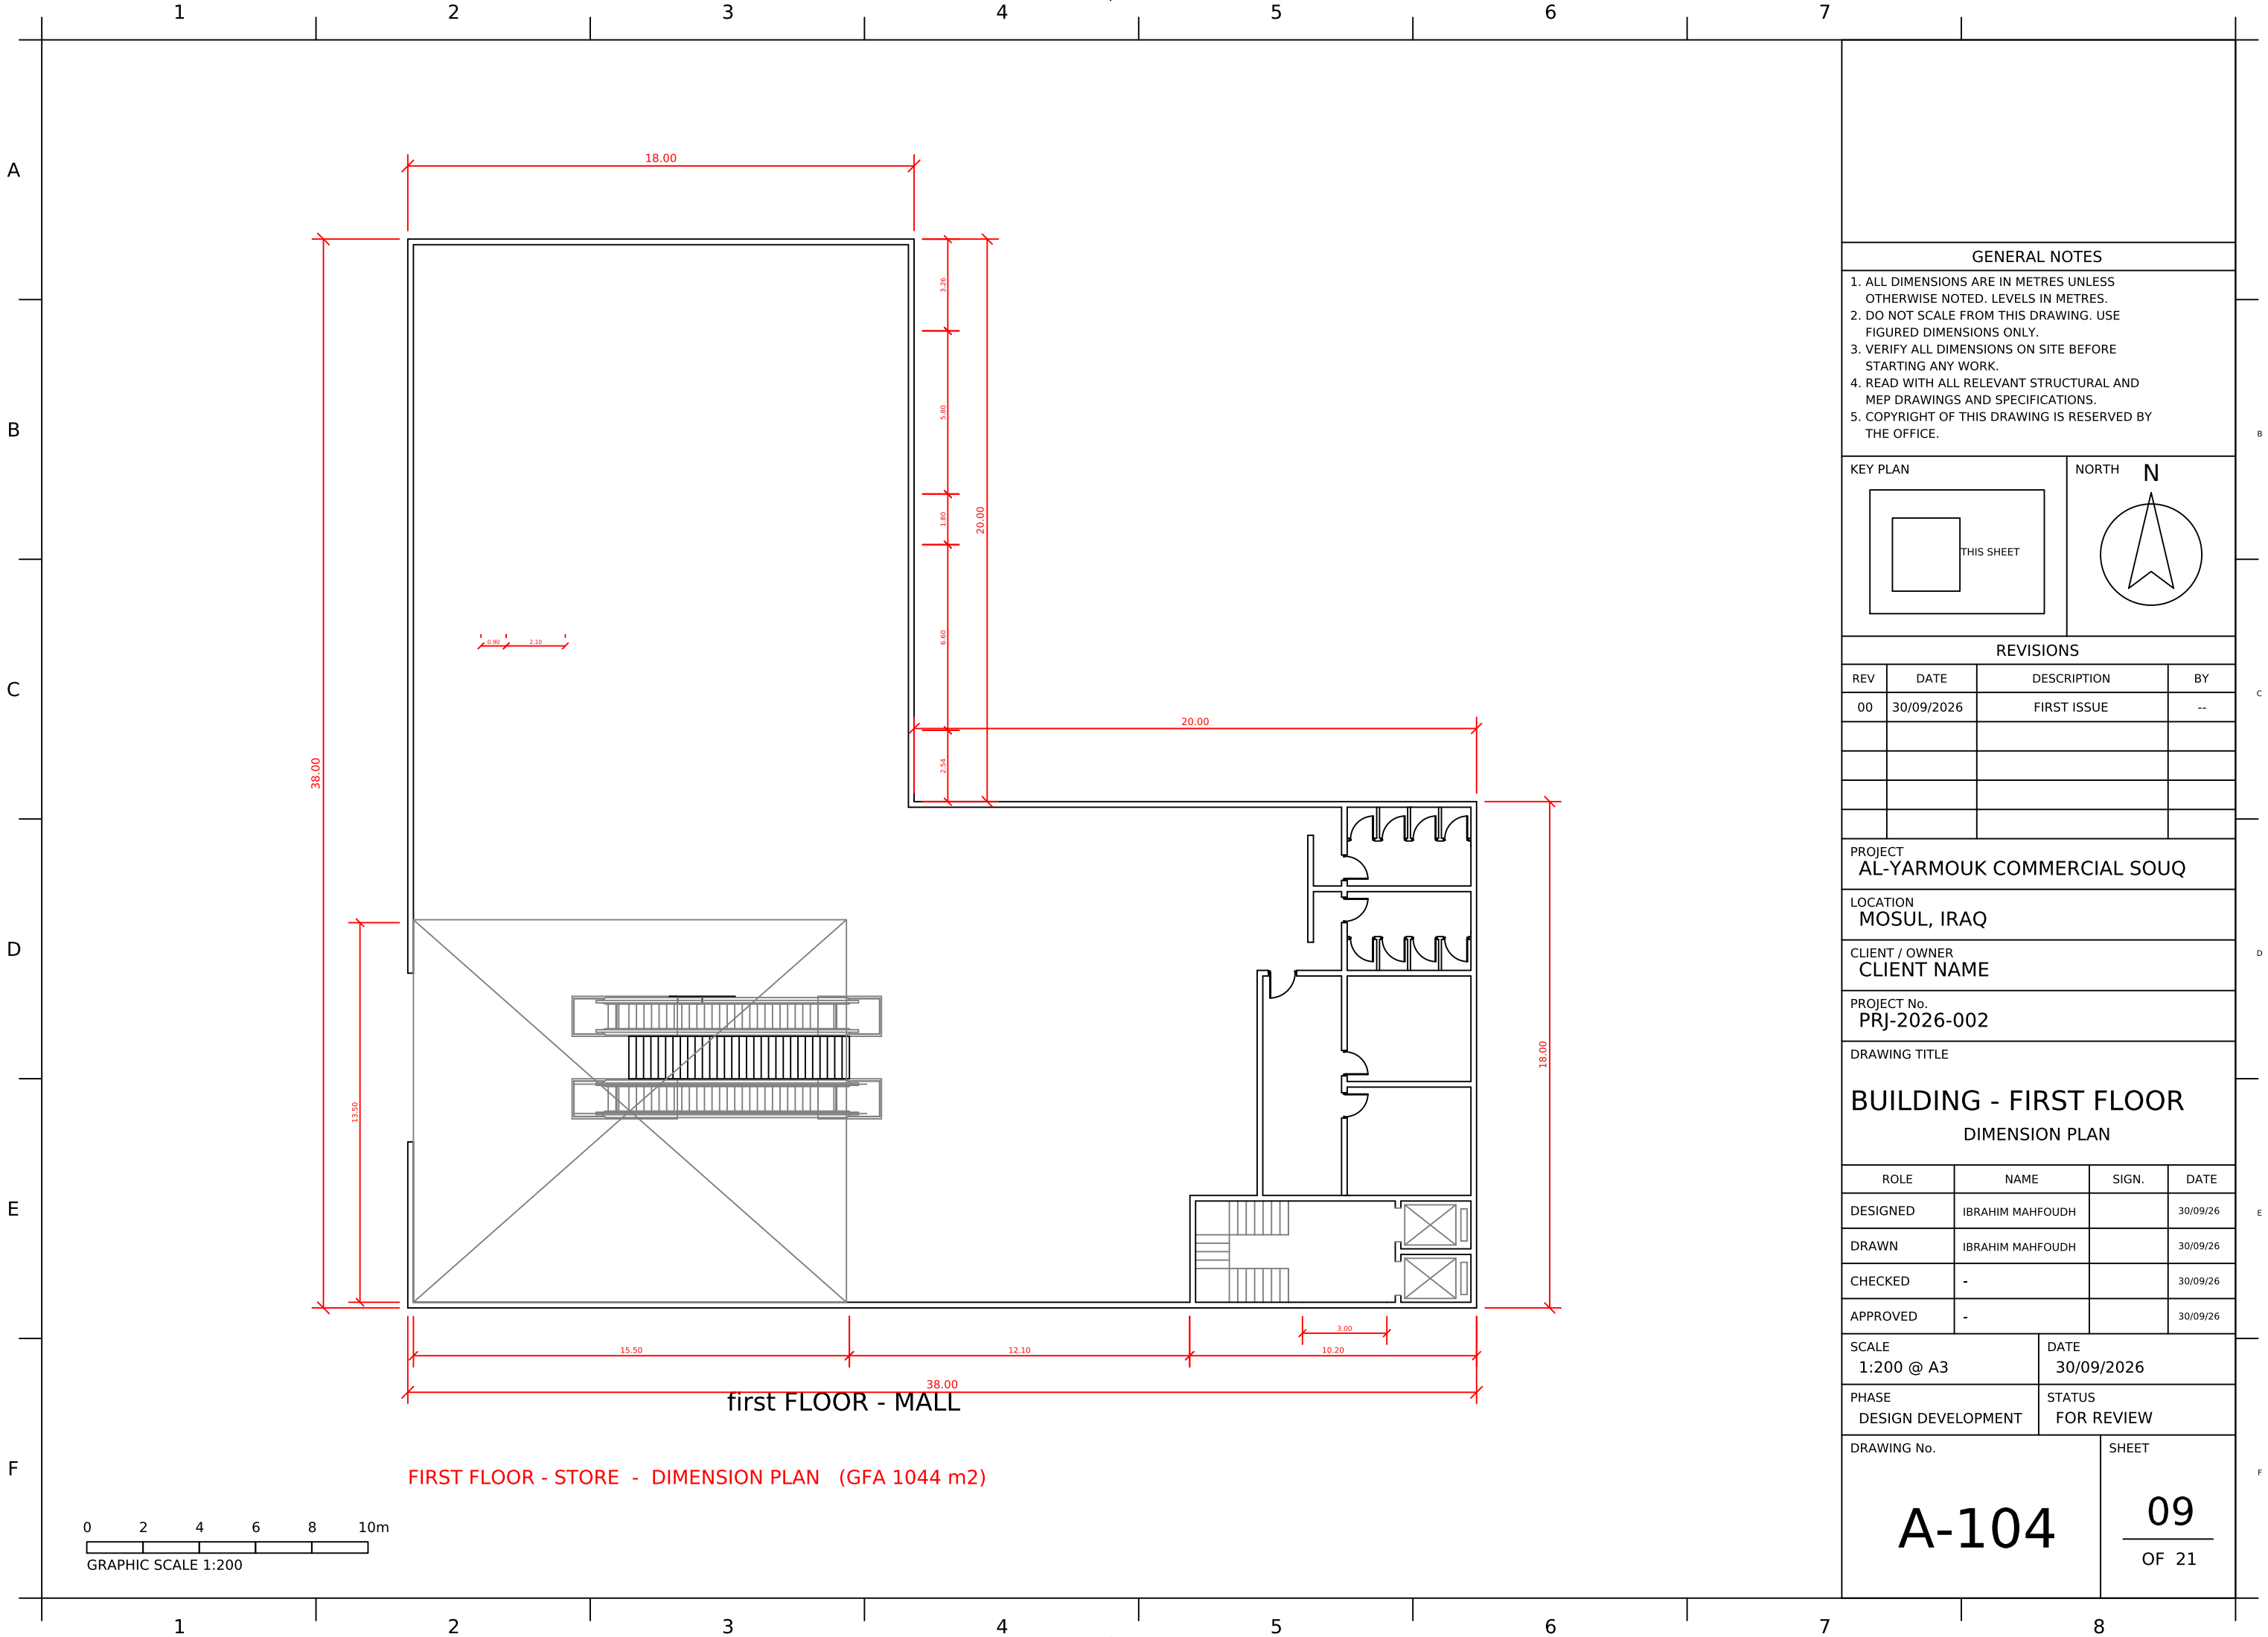

GENERAL NOTES

1. ALL DIMENSIONS ARE IN METRES UNLESS OTHERWISE NOTED. LEVELS IN METRES.
2. DO NOT SCALE FROM THIS DRAWING. USE FIGURED DIMENSIONS ONLY.
3. VERIFY ALL DIMENSIONS ON SITE BEFORE STARTING ANY WORK.
4. READ WITH ALL RELEVANT STRUCTURAL AND MEP DRAWINGS AND SPECIFICATIONS.
5. COPYRIGHT OF THIS DRAWING IS RESERVED BY THE OFFICE.

KEY PLAN

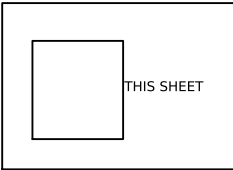

THIS SHEET

NORTH

N



REVISIONS

REV	DATE	DESCRIPTION	BY
00	30/09/2026	FIRST ISSUE	--

PROJECT
AL-YARMOUK COMMERCIAL SOUQ

LOCATION
MOSUL, IRAQ

CLIENT / OWNER
CLIENT NAME

PROJECT No.
PRJ-2026-002

DRAWING TITLE

BUILDING - FIRST FLOOR
DIMENSION PLAN

ROLE	NAME	SIGN.	DATE
DESIGNED	IBRAHIM MAHFOUDH		30/09/26
DRAWN	IBRAHIM MAHFOUDH		30/09/26
CHECKED	-		30/09/26
APPROVED	-		30/09/26

SCALE
1:200 @ A3

DATE
30/09/2026

PHASE
DESIGN DEVELOPMENT

STATUS
FOR REVIEW

DRAWING No.

A-104

SHEET

09


OF 21



GENERAL NOTES


- 1. ALL DIMENSIONS ARE IN METRES UNLESS OTHERWISE NOTED. LEVELS IN METRES.
- 2. DO NOT SCALE FROM THIS DRAWING. USE FIGURED DIMENSIONS ONLY.
- 3. VERIFY ALL DIMENSIONS ON SITE BEFORE STARTING ANY WORK.
- 4. READ WITH ALL RELEVANT STRUCTURAL AND MEP DRAWINGS AND SPECIFICATIONS.
- 5. COPYRIGHT OF THIS DRAWING IS RESERVED BY THE OFFICE.

KEY PLAN

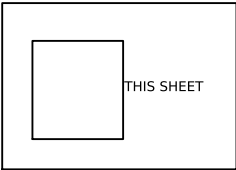

NORTH

N

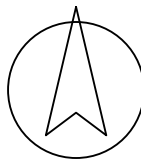

REVISIONS

REV	DATE	DESCRIPTION	BY
00	30/09/2026	FIRST ISSUE	--

PROJECT
AL-YARMOUK COMMERCIAL SOUQ

LOCATION
MOSUL, IRAQ

CLIENT / OWNER
CLIENT NAME

PROJECT No.
PRJ-2026-002

DRAWING TITLE


BUILDING - TYPICAL FLOOR
OFFICE APARTMENTS - FURNITURE

ROLE	NAME	SIGN.	DATE
DESIGNED	IBRAHIM MAHFOUDH		30/09/26
DRAWN	IBRAHIM MAHFOUDH		30/09/26
CHECKED	-		30/09/26
APPROVED	-		30/09/26

SCALE 1:200 @ A3	DATE 30/09/2026
---------------------	--------------------

PHASE DESIGN DEVELOPMENT	STATUS FOR REVIEW
-----------------------------	----------------------

DRAWING No. A-105	SHEET 10 OF 21
---------------------------------	---------------------------------

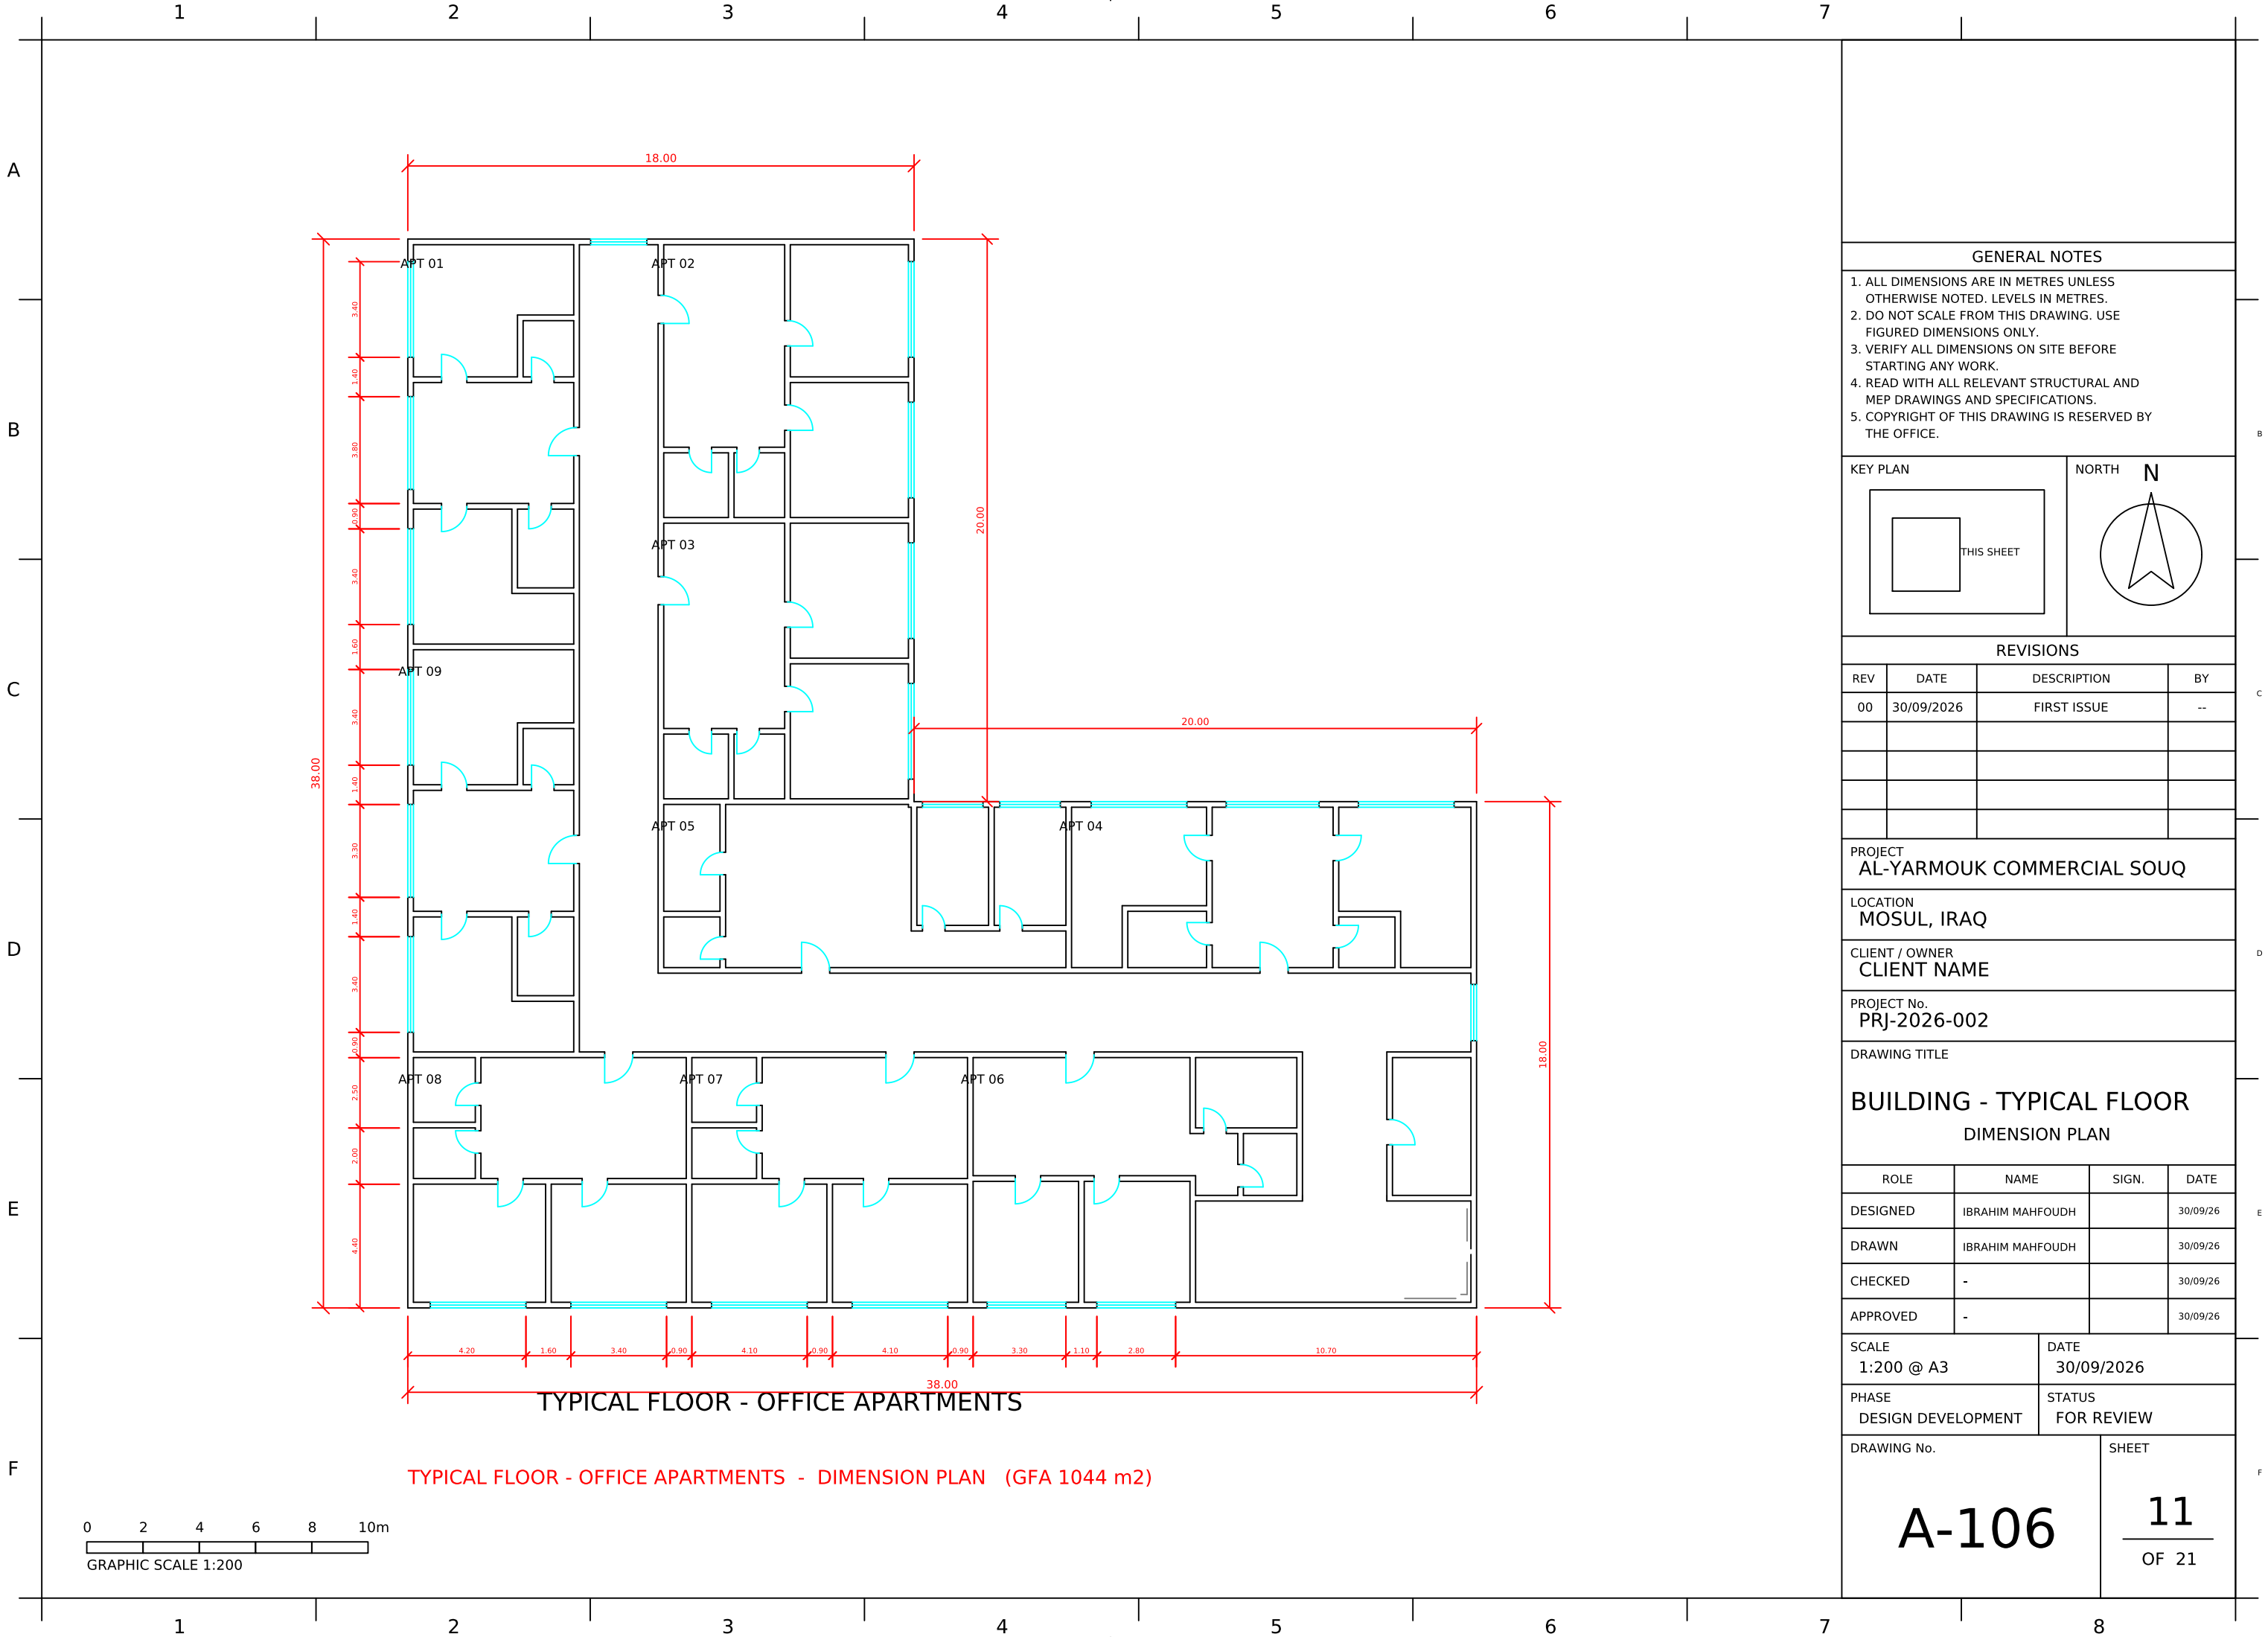

- GENERAL NOTES
1. ALL DIMENSIONS ARE IN METRES UNLESS OTHERWISE NOTED. LEVELS IN METRES.
 2. DO NOT SCALE FROM THIS DRAWING. USE FIGURED DIMENSIONS ONLY.
 3. VERIFY ALL DIMENSIONS ON SITE BEFORE STARTING ANY WORK.
 4. READ WITH ALL RELEVANT STRUCTURAL AND MEP DRAWINGS AND SPECIFICATIONS.
 5. COPYRIGHT OF THIS DRAWING IS RESERVED BY THE OFFICE.

KEY PLAN

NORTH

REVISIONS			
REV	DATE	DESCRIPTION	BY
00	30/09/2026	FIRST ISSUE	--

PROJECT
AL-YARMOUK COMMERCIAL SOUQ

LOCATION
MOSUL, IRAQ

CLIENT / OWNER
CLIENT NAME

PROJECT No.
PRJ-2026-002

DRAWING TITLE

BUILDING - TYPICAL FLOOR
DIMENSION PLAN

ROLE	NAME	SIGN.	DATE
DESIGNED	IBRAHIM MAHFOUDH		30/09/26
DRAWN	IBRAHIM MAHFOUDH		30/09/26
CHECKED	-		30/09/26
APPROVED	-		30/09/26

SCALE 1:200 @ A3	DATE 30/09/2026
---------------------	--------------------

PHASE DESIGN DEVELOPMENT	STATUS FOR REVIEW
-----------------------------	----------------------

DRAWING No.


A-106

SHEET


11

OF 21


SHOP MODEL 2 - EXTERIOR SHOP - PLANS (GF / UPPER / ROOF)

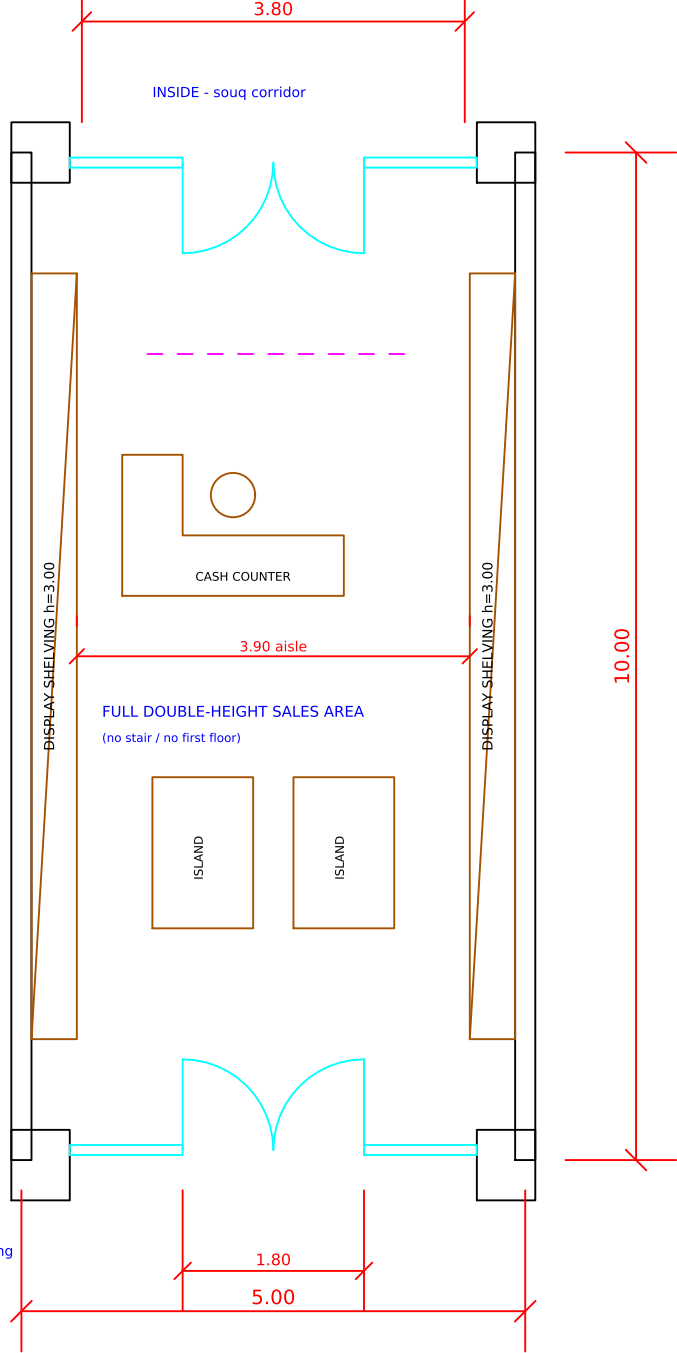

GROUND FLOOR PLAN (48 m2)

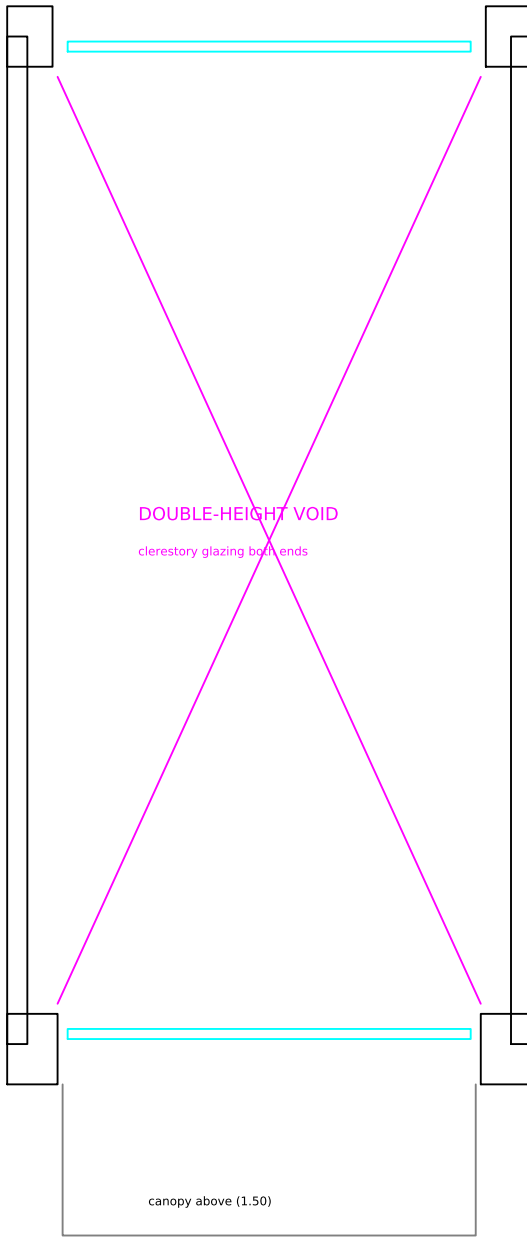

UPPER LEVEL (cut +4.50)

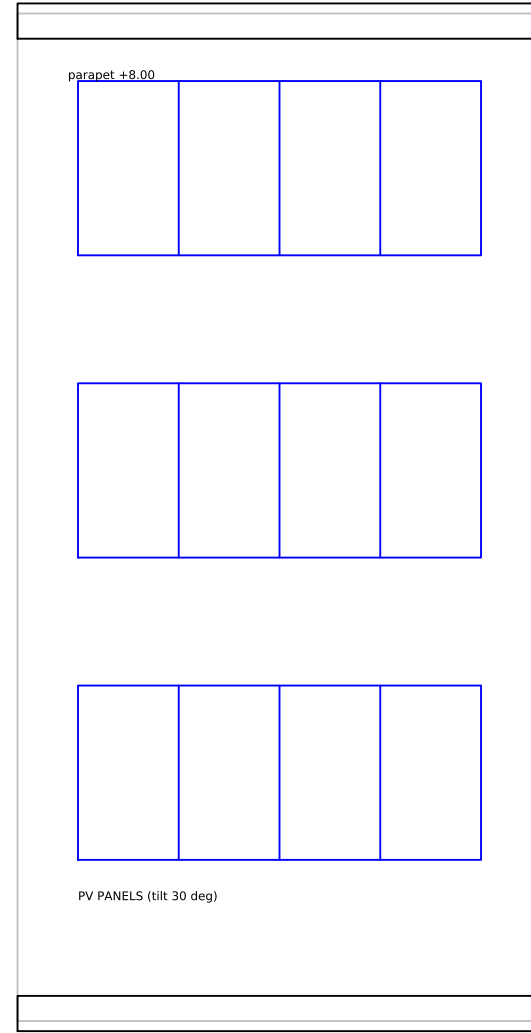


ROOF PLAN (+6.40)

GENERAL NOTES


1. ALL DIMENSIONS ARE IN METRES UNLESS OTHERWISE NOTED. LEVELS IN METRES.
2. DO NOT SCALE FROM THIS DRAWING. USE FIGURED DIMENSIONS ONLY.
3. VERIFY ALL DIMENSIONS ON SITE BEFORE STARTING ANY WORK.
4. READ WITH ALL RELEVANT STRUCTURAL AND MEP DRAWINGS AND SPECIFICATIONS.
5. COPYRIGHT OF THIS DRAWING IS RESERVED BY THE OFFICE.

KEY PLAN

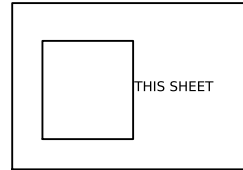

NORTH

N

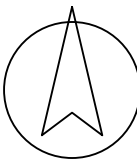

REVISIONS

REV	DATE	DESCRIPTION	BY
00	30/09/2026	FIRST ISSUE	--

PROJECT
AL-YARMOUK COMMERCIAL SOUQ

LOCATION
MOSUL, IRAQ

CLIENT / OWNER
CLIENT NAME

PROJECT No.
PRJ-2026-002

DRAWING TITLE
SHOP MODEL - EXTERIOR
PLANS

ROLE	NAME	SIGN.	DATE
DESIGNED	IBRAHIM MAHFOUDH		30/09/26
DRAWN	IBRAHIM MAHFOUDH		30/09/26
CHECKED	-		30/09/26
APPROVED	-		30/09/26

SCALE
1:75 @ A3

DATE
30/09/2026

PHASE
DESIGN DEVELOPMENT


STATUS
FOR REVIEW

DRAWING No.

A-201

SHEET

12
OF 21

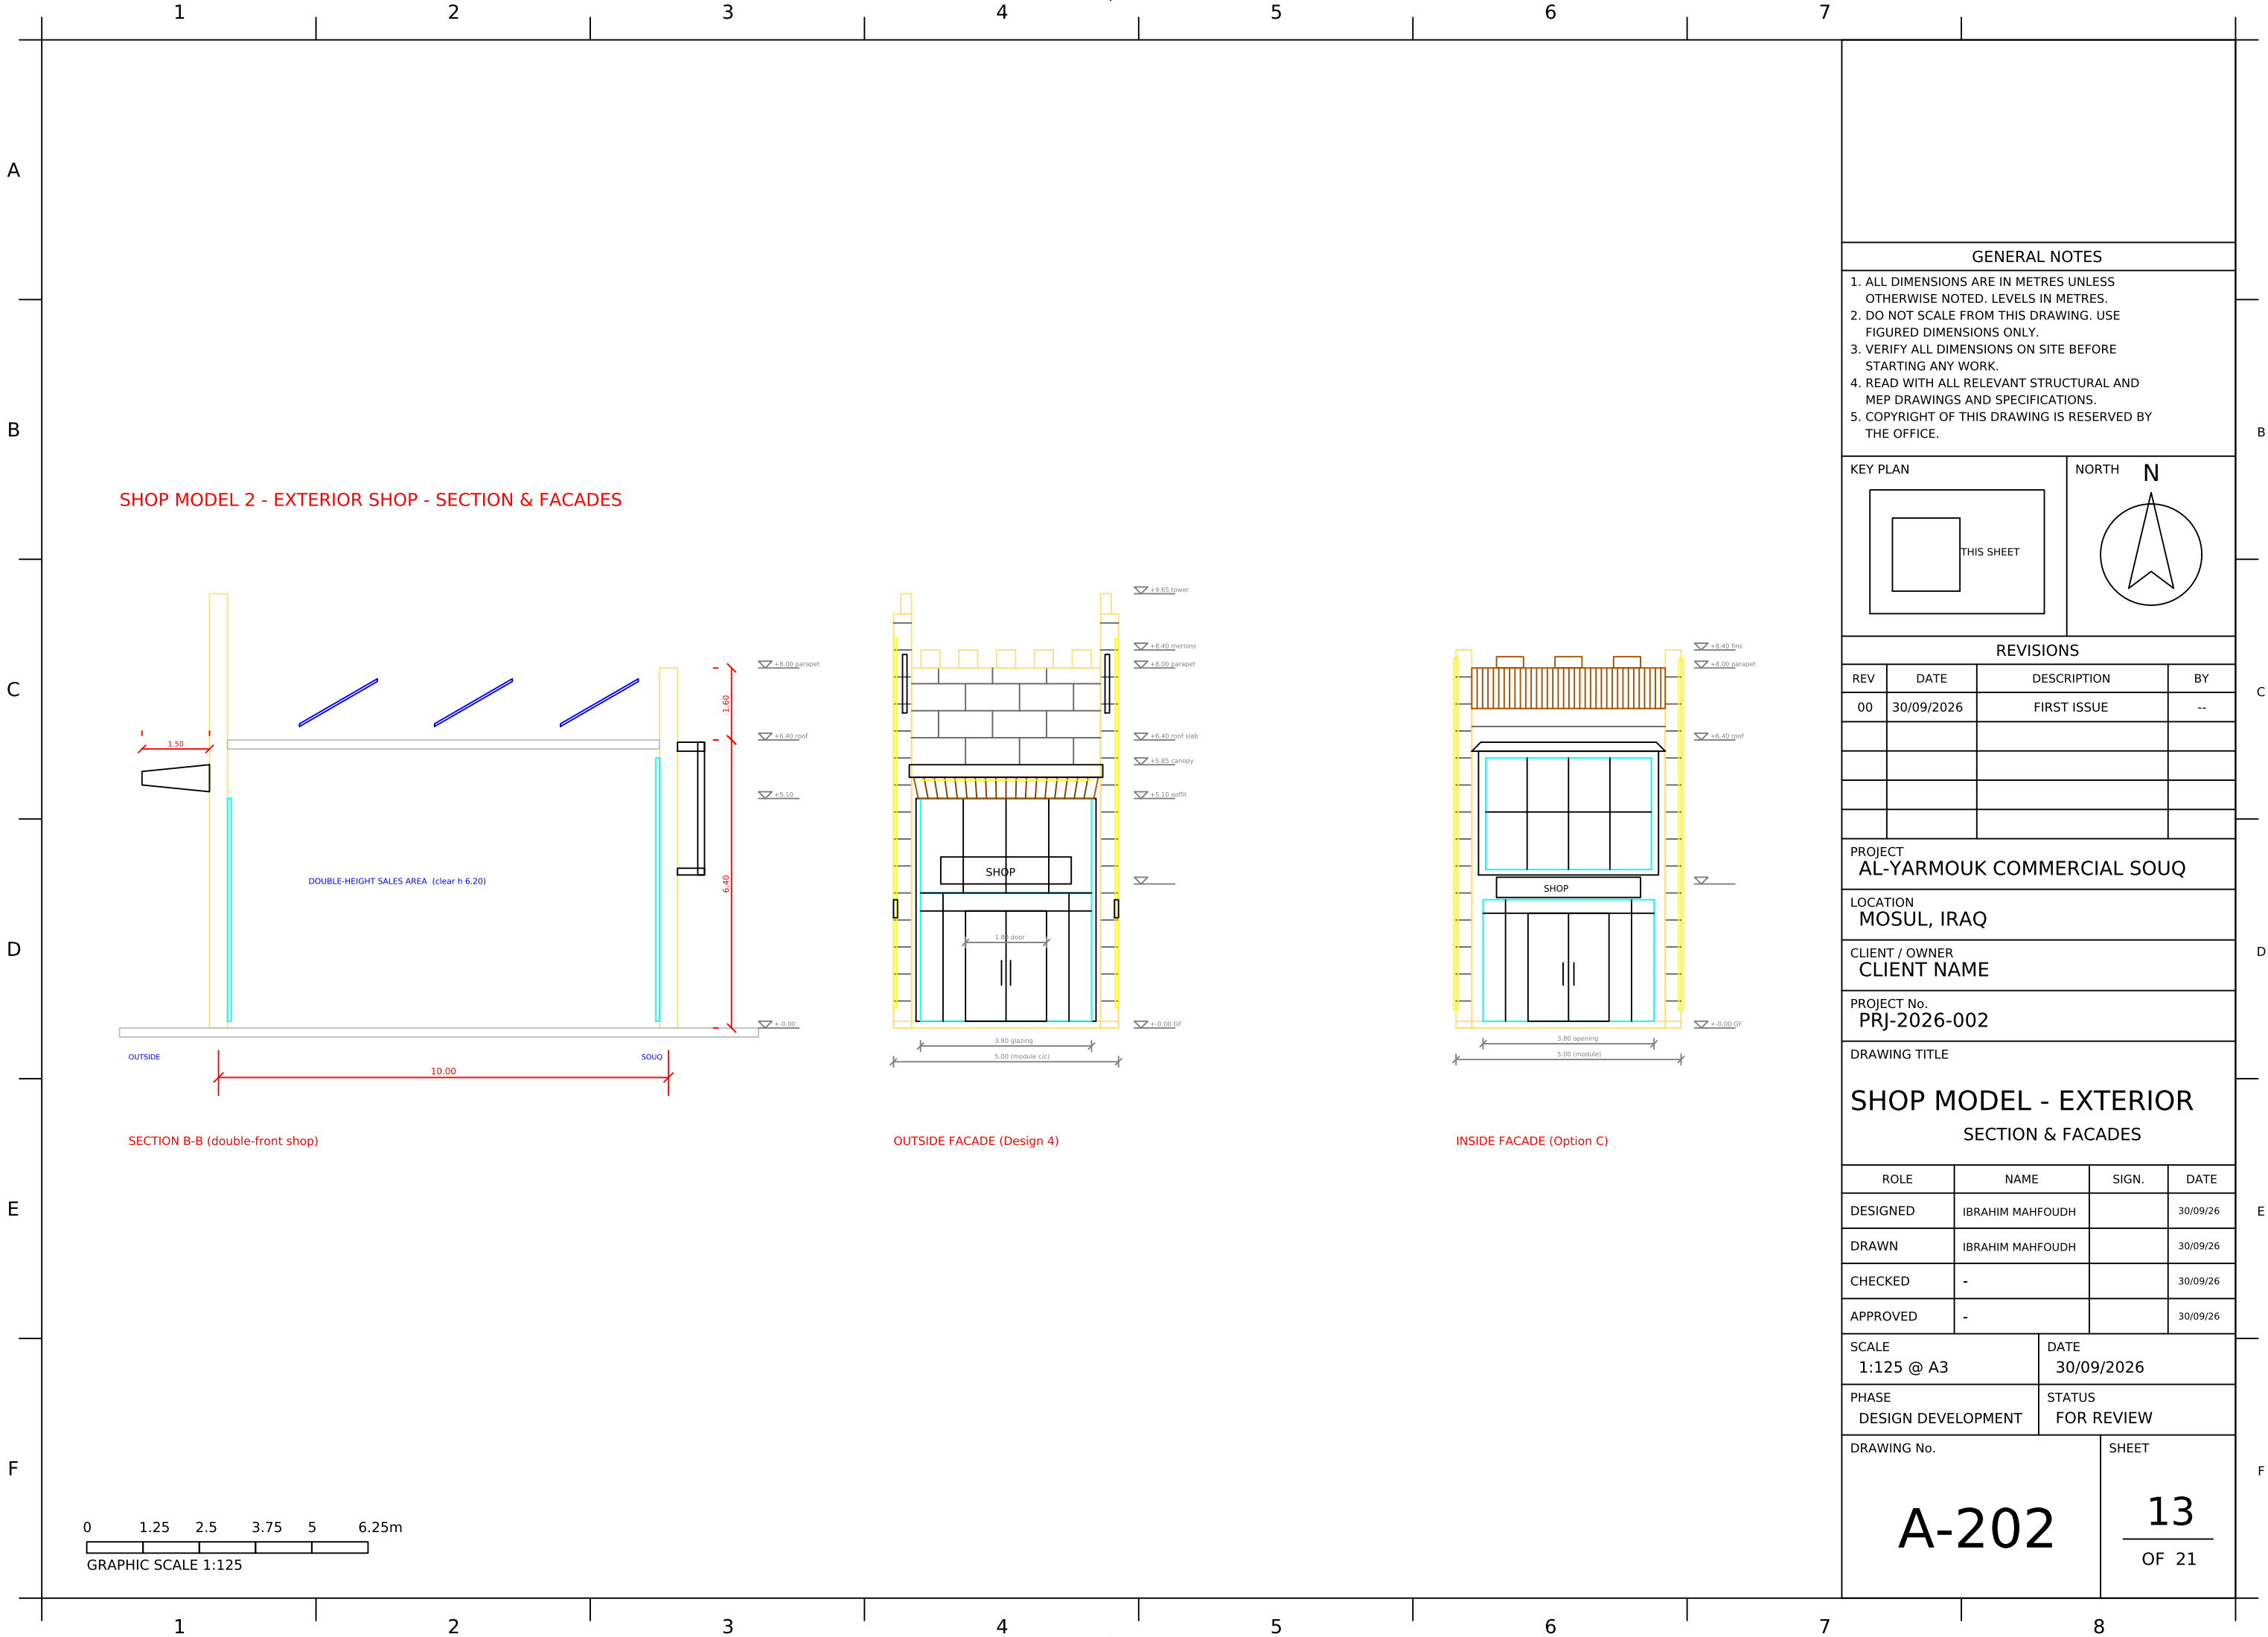

- GENERAL NOTES
1. ALL DIMENSIONS ARE IN METRES UNLESS OTHERWISE NOTED. LEVELS IN METRES.
 2. DO NOT SCALE FROM THIS DRAWING. USE FIGURED DIMENSIONS ONLY.
 3. VERIFY ALL DIMENSIONS ON SITE BEFORE STARTING ANY WORK.
 4. READ WITH ALL RELEVANT STRUCTURAL AND MEP DRAWINGS AND SPECIFICATIONS.
 5. COPYRIGHT OF THIS DRAWING IS RESERVED BY THE OFFICE.

KEY PLAN

NORTH

REVISIONS			
REV	DATE	DESCRIPTION	BY
00	30/09/2026	FIRST ISSUE	--

PROJECT
AL-YARMOUK COMMERCIAL SOUQ

LOCATION
MOSUL, IRAQ

CLIENT / OWNER
CLIENT NAME

PROJECT No.
PRJ-2026-002

DRAWING TITLE

SHOP MODEL - EXTERIOR
SECTION & FACADES

ROLE	NAME	SIGN.	DATE
DESIGNED	IBRAHIM MAHFOUDH		30/09/26
DRAWN	IBRAHIM MAHFOUDH		30/09/26
CHECKED	-		30/09/26
APPROVED	-		30/09/26

SCALE 1:125 @ A3	DATE 30/09/2026
PHASE DESIGN DEVELOPMENT	STATUS FOR REVIEW


DRAWING No.

A-202


SHEET

13
OF 21


SHOP MODEL 1 - INTERIOR SHOP - PLANS (GF + FF)

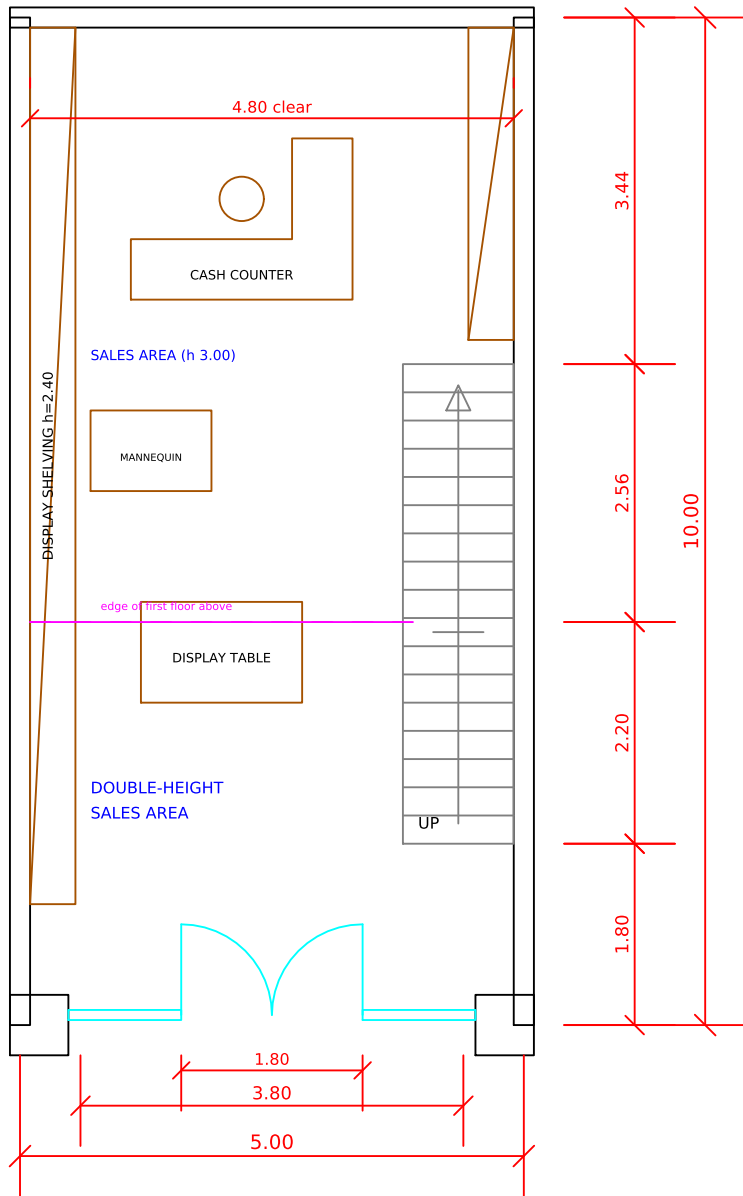

GROUND FLOOR PLAN (+0.00, 48 m2)

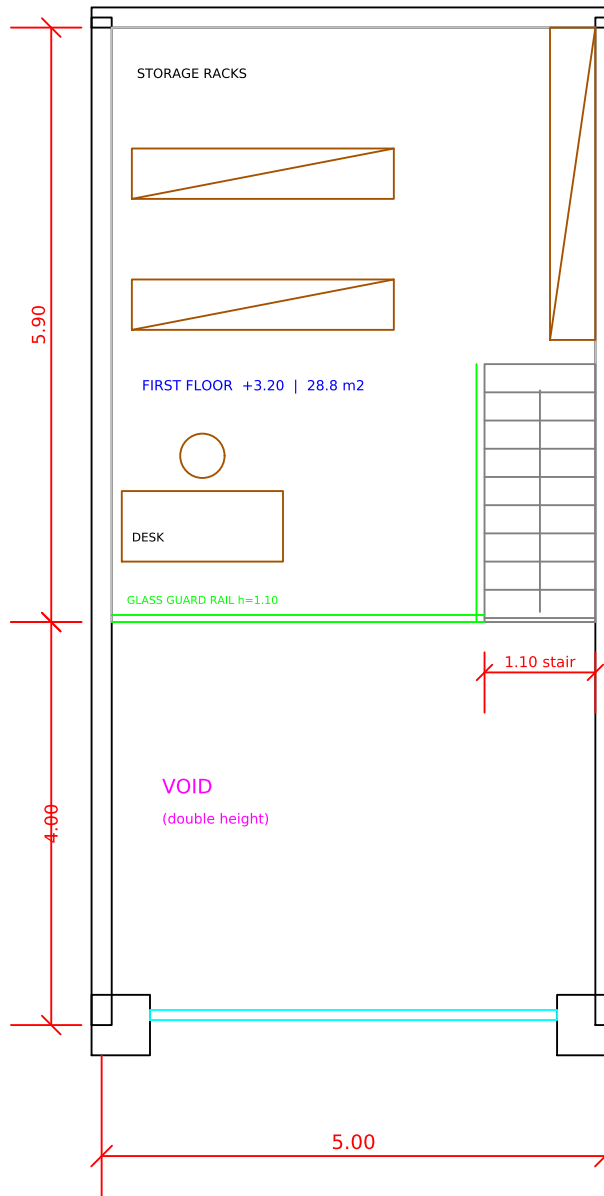


FIRST FLOOR PLAN (+3.20, 28.8 m2)

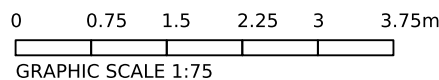

GENERAL NOTES

- ALL DIMENSIONS ARE IN METRES UNLESS OTHERWISE NOTED. LEVELS IN METRES.
- DO NOT SCALE FROM THIS DRAWING. USE FIGURED DIMENSIONS ONLY.
- VERIFY ALL DIMENSIONS ON SITE BEFORE STARTING ANY WORK.
- READ WITH ALL RELEVANT STRUCTURAL AND MEP DRAWINGS AND SPECIFICATIONS.
- COPYRIGHT OF THIS DRAWING IS RESERVED BY THE OFFICE.

KEY PLAN

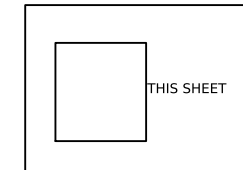

THIS SHEET

NORTH



REVISIONS

REV	DATE	DESCRIPTION	BY
00	30/09/2026	FIRST ISSUE	--

PROJECT
AL-YARMOUK COMMERCIAL SOUQ

LOCATION
MOSUL, IRAQ

CLIENT / OWNER
CLIENT NAME

PROJECT No.
PRJ-2026-002

DRAWING TITLE
SHOP MODEL - INTERIOR
PLANS

ROLE	NAME	SIGN.	DATE
DESIGNED	IBRAHIM MAHFOUDH		30/09/26
DRAWN	IBRAHIM MAHFOUDH		30/09/26
CHECKED	-		30/09/26
APPROVED	-		30/09/26

SCALE
1:75 @ A3

DATE
30/09/2026

PHASE
DESIGN DEVELOPMENT

STATUS
FOR REVIEW


DRAWING No.

A-203


SHEET

14
OF 21


SHOP MODEL 1 - INTERIOR SHOP - SECTION & FACADE

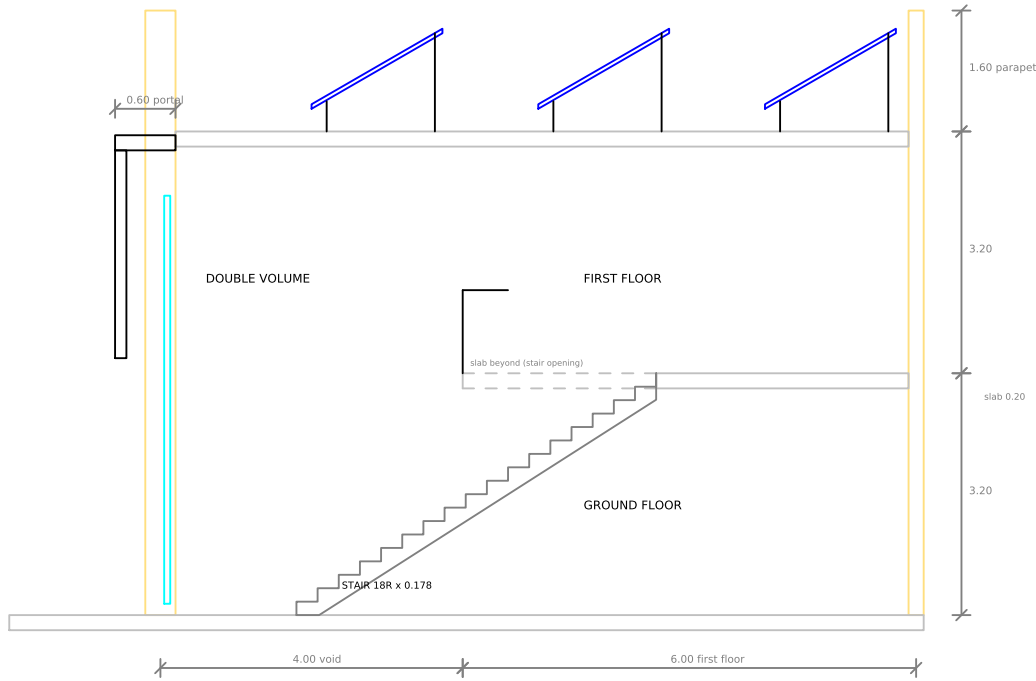

SECTION A-A (through stair)

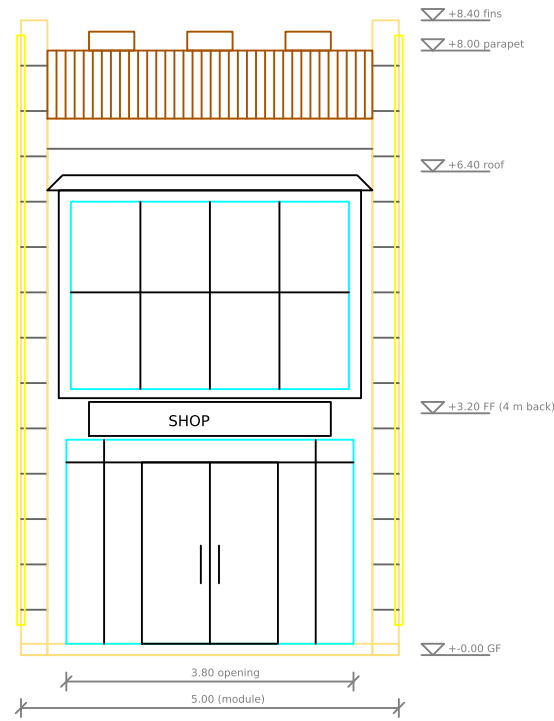


SHOP FRONT - INTERIOR FACADE (Option C)

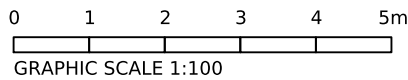


GENERAL NOTES

1. ALL DIMENSIONS ARE IN METRES UNLESS OTHERWISE NOTED. LEVELS IN METRES.
2. DO NOT SCALE FROM THIS DRAWING. USE FIGURED DIMENSIONS ONLY.
3. VERIFY ALL DIMENSIONS ON SITE BEFORE STARTING ANY WORK.
4. READ WITH ALL RELEVANT STRUCTURAL AND MEP DRAWINGS AND SPECIFICATIONS.
5. COPYRIGHT OF THIS DRAWING IS RESERVED BY THE OFFICE.

KEY PLAN

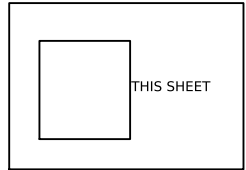

NORTH

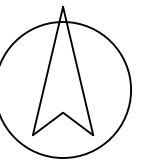

REVISIONS

REV	DATE	DESCRIPTION	BY
00	30/09/2026	FIRST ISSUE	--

PROJECT
AL-YARMOUK COMMERCIAL SOUQ

LOCATION
MOSUL, IRAQ

CLIENT / OWNER
CLIENT NAME

PROJECT No.
PRJ-2026-002


DRAWING TITLE
SHOP MODEL - INTERIOR
SECTION & FACADE


ROLE	NAME	SIGN.	DATE
DESIGNED	IBRAHIM MAHFOUDH		30/09/26
DRAWN	IBRAHIM MAHFOUDH		30/09/26
CHECKED	-		30/09/26
APPROVED	-		30/09/26

SCALE 1:100 @ A3	DATE 30/09/2026
---------------------	--------------------

PHASE DESIGN DEVELOPMENT	STATUS FOR REVIEW
-----------------------------	----------------------

DRAWING No. A-204	SHEET 15 OF 21
-----------------------------	-----------------------------

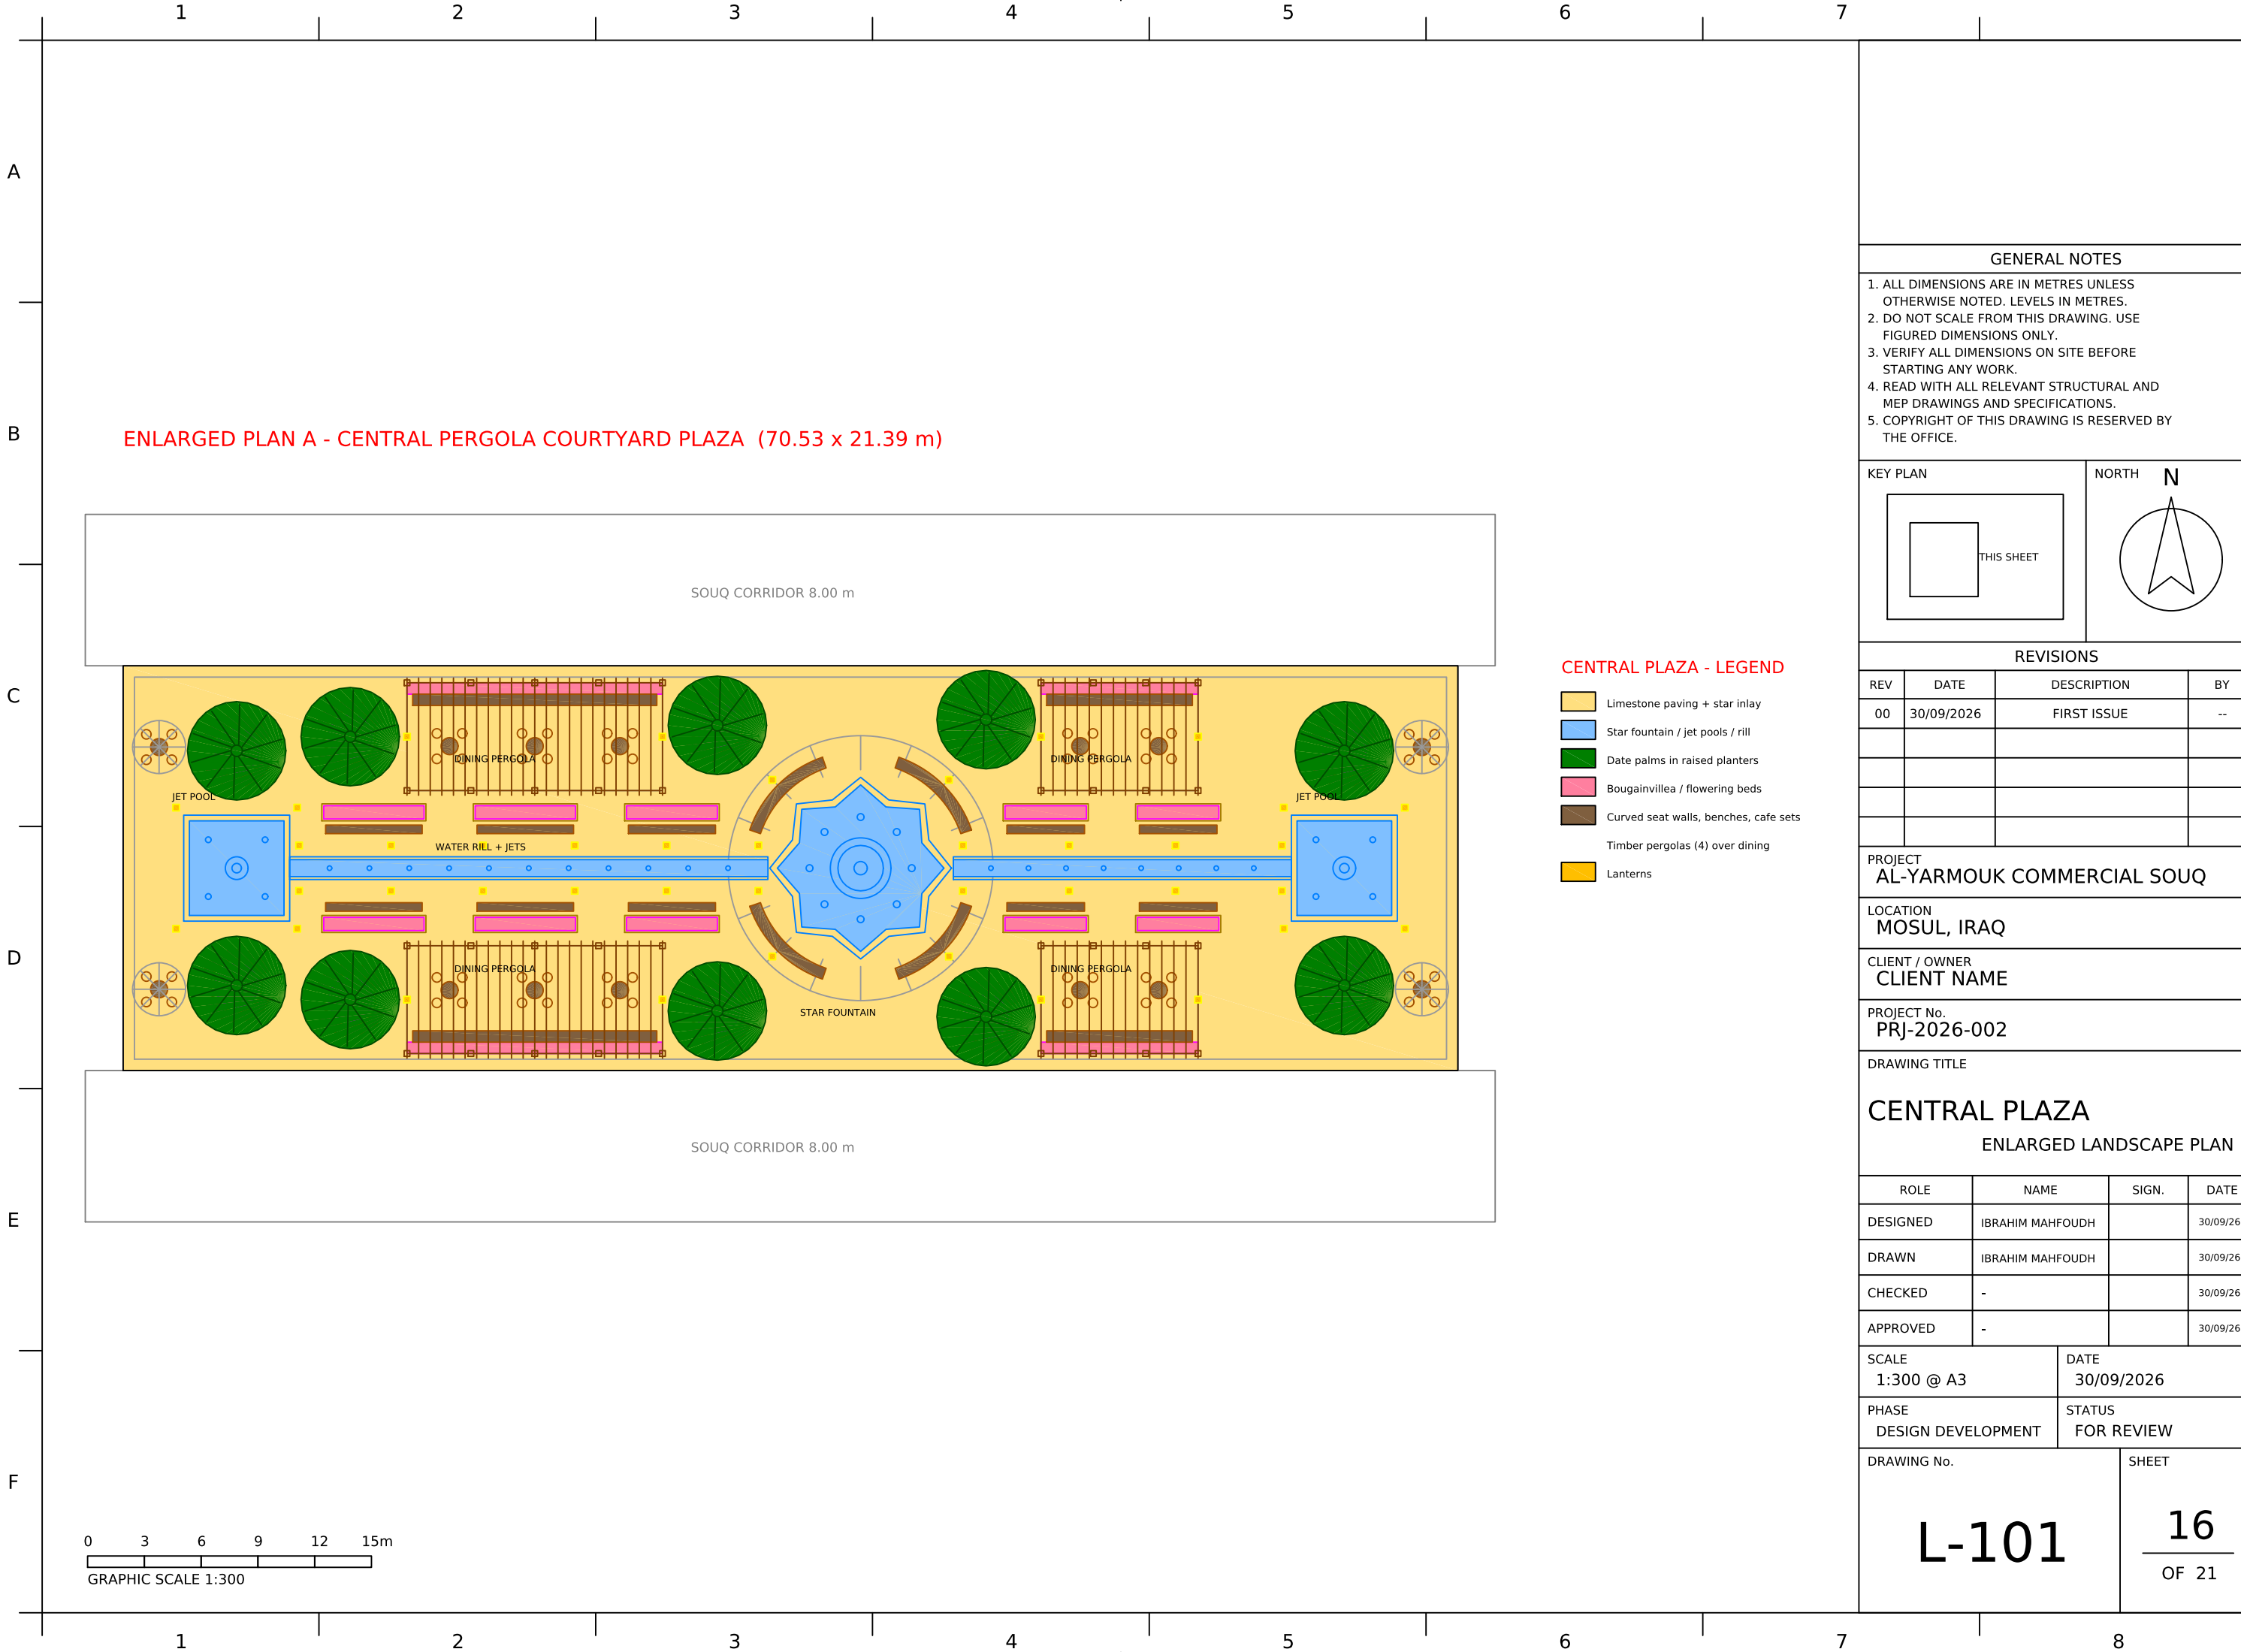

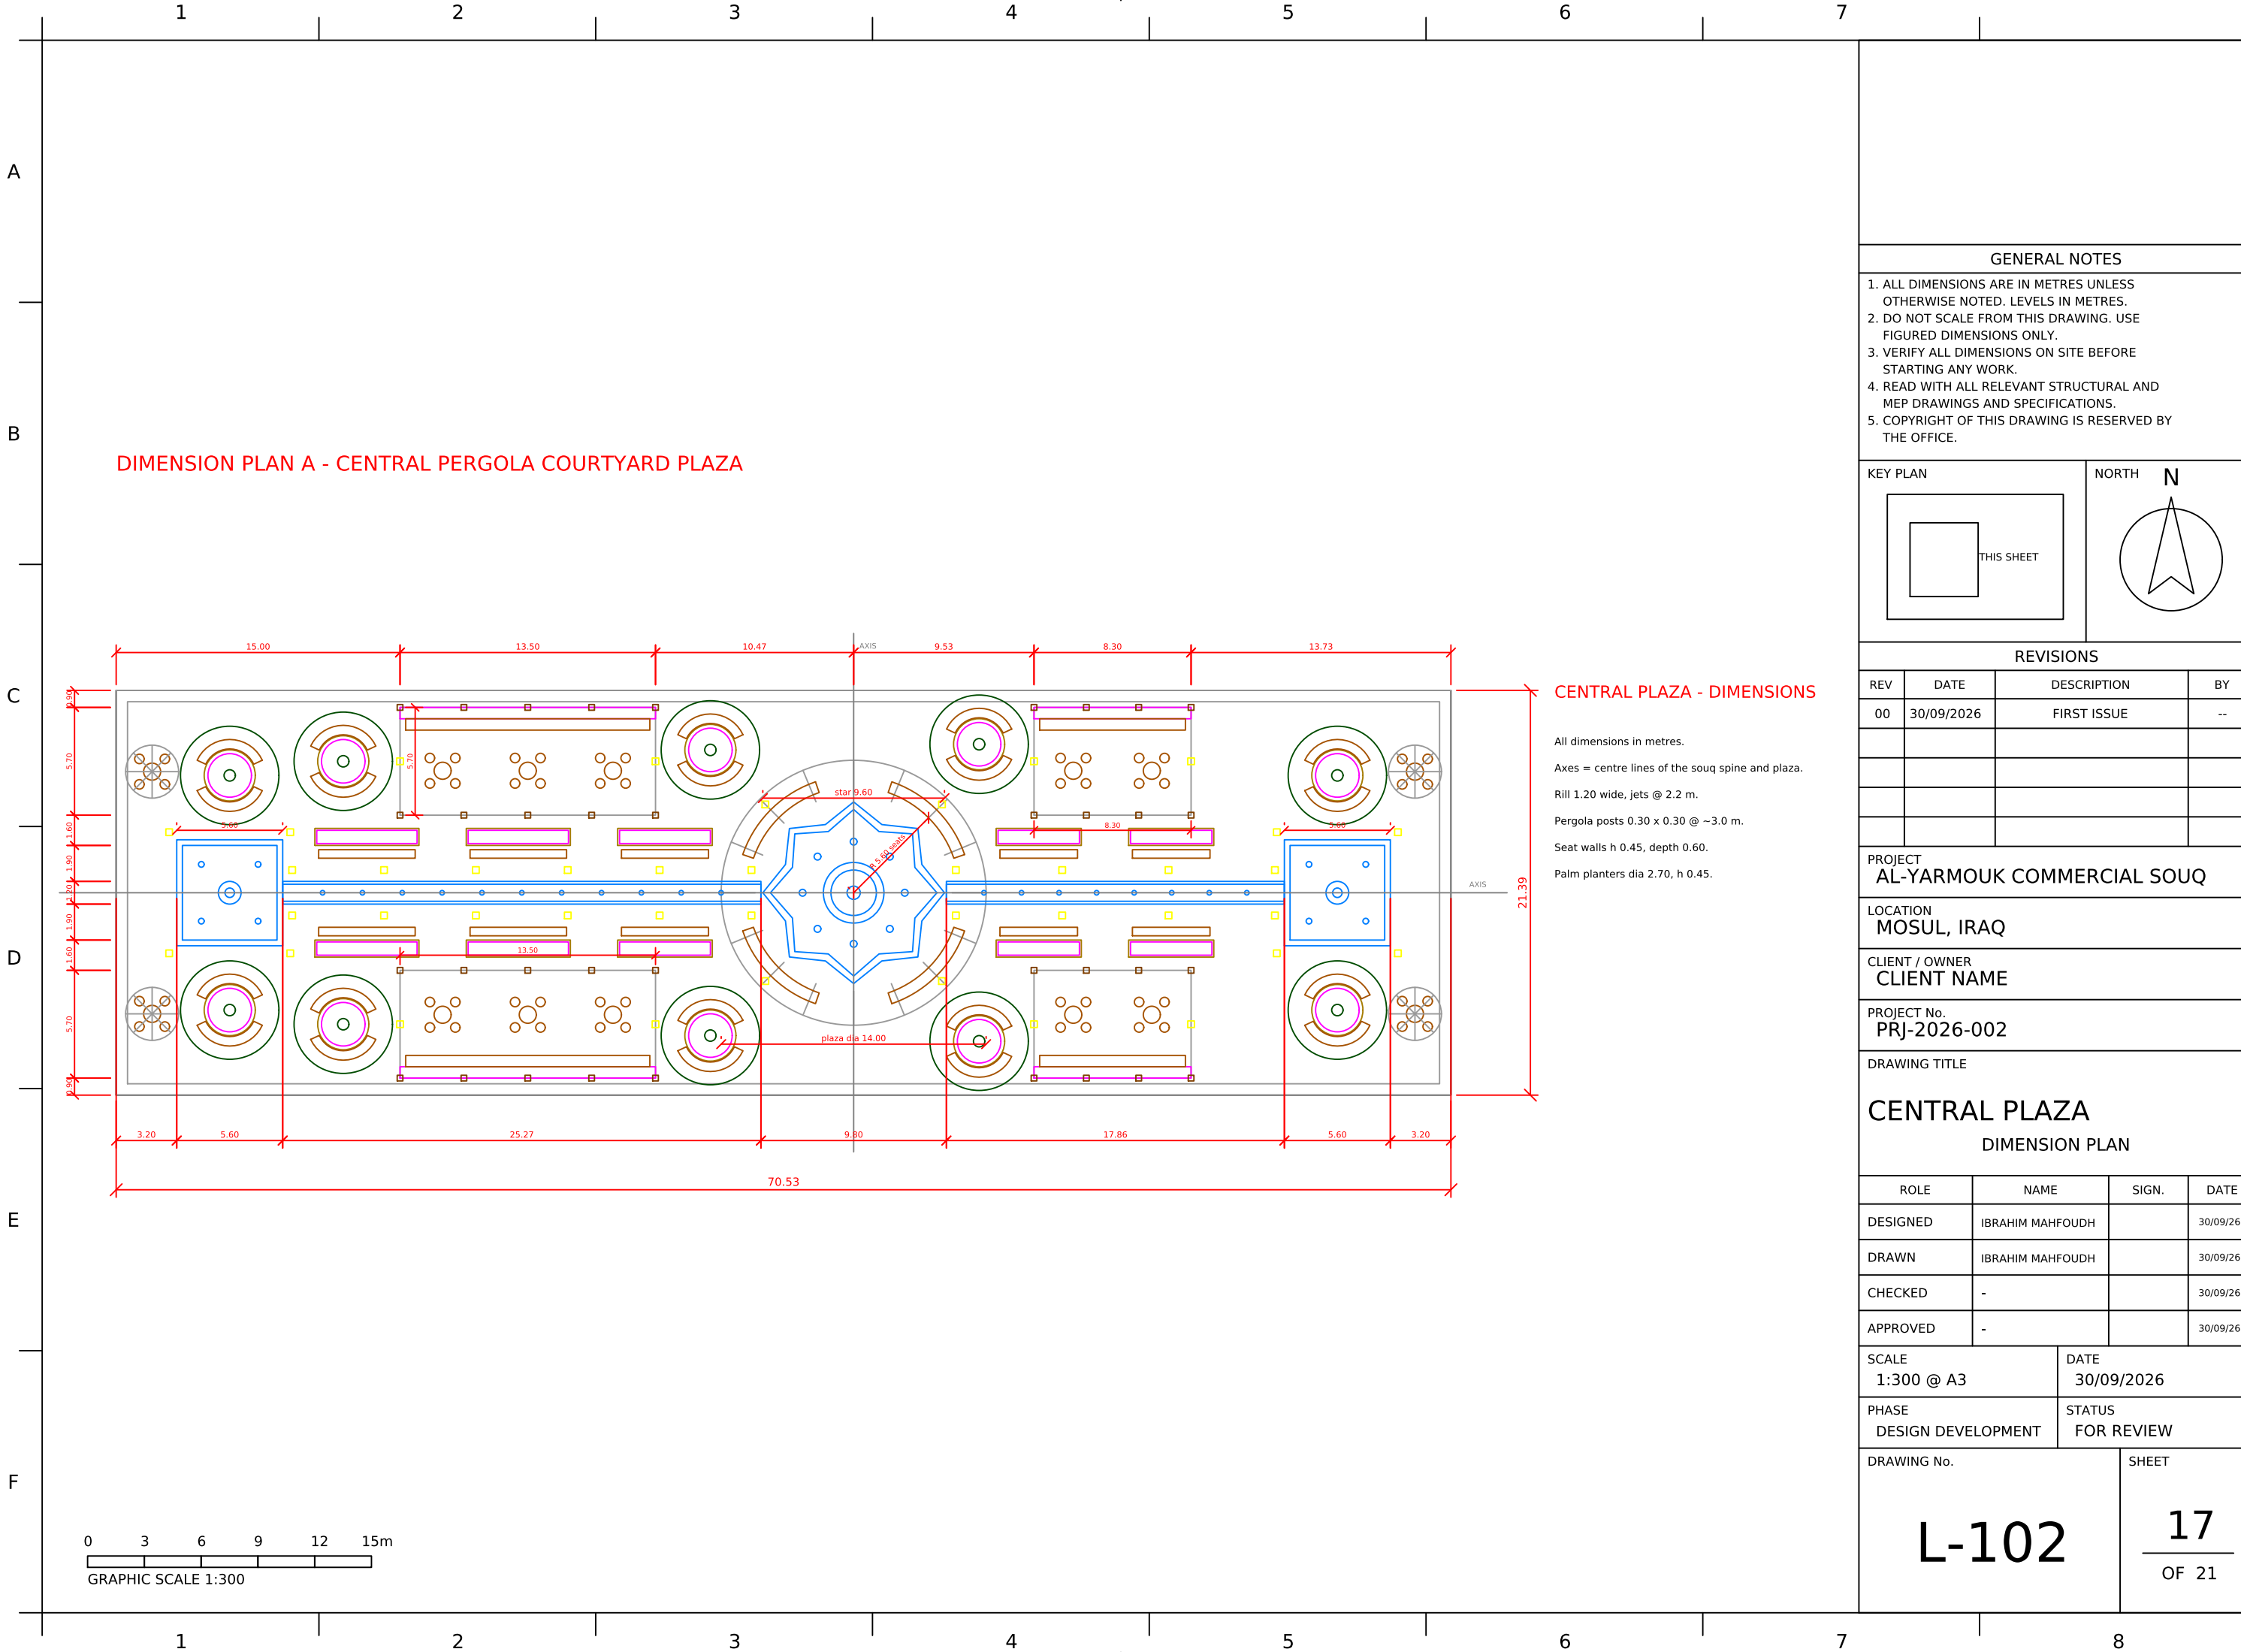

DIMENSION PLAN A - CENTRAL PERGOLA COURTYARD PLAZA


CENTRAL PLAZA - DIMENSIONS

All dimensions in metres.
Axes = centre lines of the souq spine and plaza.
Rill 1.20 wide, jets @ 2.2 m.
Pergola posts 0.30 x 0.30 @ ~3.0 m.
Seat walls h 0.45, depth 0.60.
Palm planters dia 2.70, h 0.45.

GENERAL NOTES


1. ALL DIMENSIONS ARE IN METRES UNLESS OTHERWISE NOTED. LEVELS IN METRES.
2. DO NOT SCALE FROM THIS DRAWING. USE FIGURED DIMENSIONS ONLY.
3. VERIFY ALL DIMENSIONS ON SITE BEFORE STARTING ANY WORK.
4. READ WITH ALL RELEVANT STRUCTURAL AND MEP DRAWINGS AND SPECIFICATIONS.
5. COPYRIGHT OF THIS DRAWING IS RESERVED BY THE OFFICE.

KEY PLAN

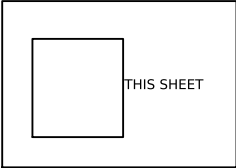

NORTH

N

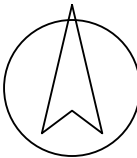

REVISIONS

REV	DATE	DESCRIPTION	BY
00	30/09/2026	FIRST ISSUE	--

PROJECT
AL-YARMOUK COMMERCIAL SOUQ

LOCATION
MOSUL, IRAQ

CLIENT / OWNER
CLIENT NAME

PROJECT No.
PRJ-2026-002


DRAWING TITLE
CENTRAL PLAZA
DIMENSION PLAN

ROLE	NAME	SIGN.	DATE
DESIGNED	IBRAHIM MAHFOUDH		30/09/26
DRAWN	IBRAHIM MAHFOUDH		30/09/26
CHECKED	-		30/09/26
APPROVED	-		30/09/26


SCALE 1:300 @ A3	DATE 30/09/2026
---------------------	--------------------

PHASE DESIGN DEVELOPMENT	STATUS FOR REVIEW
-----------------------------	----------------------

DRAWING No. L-102	SHEET 17 OF 21
-----------------------------	-----------------------------

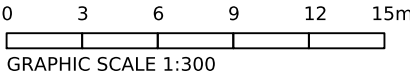

ENLARGED PLAN B - FOUNTAIN COURT (next to the building) 20.00 x 20.00 m

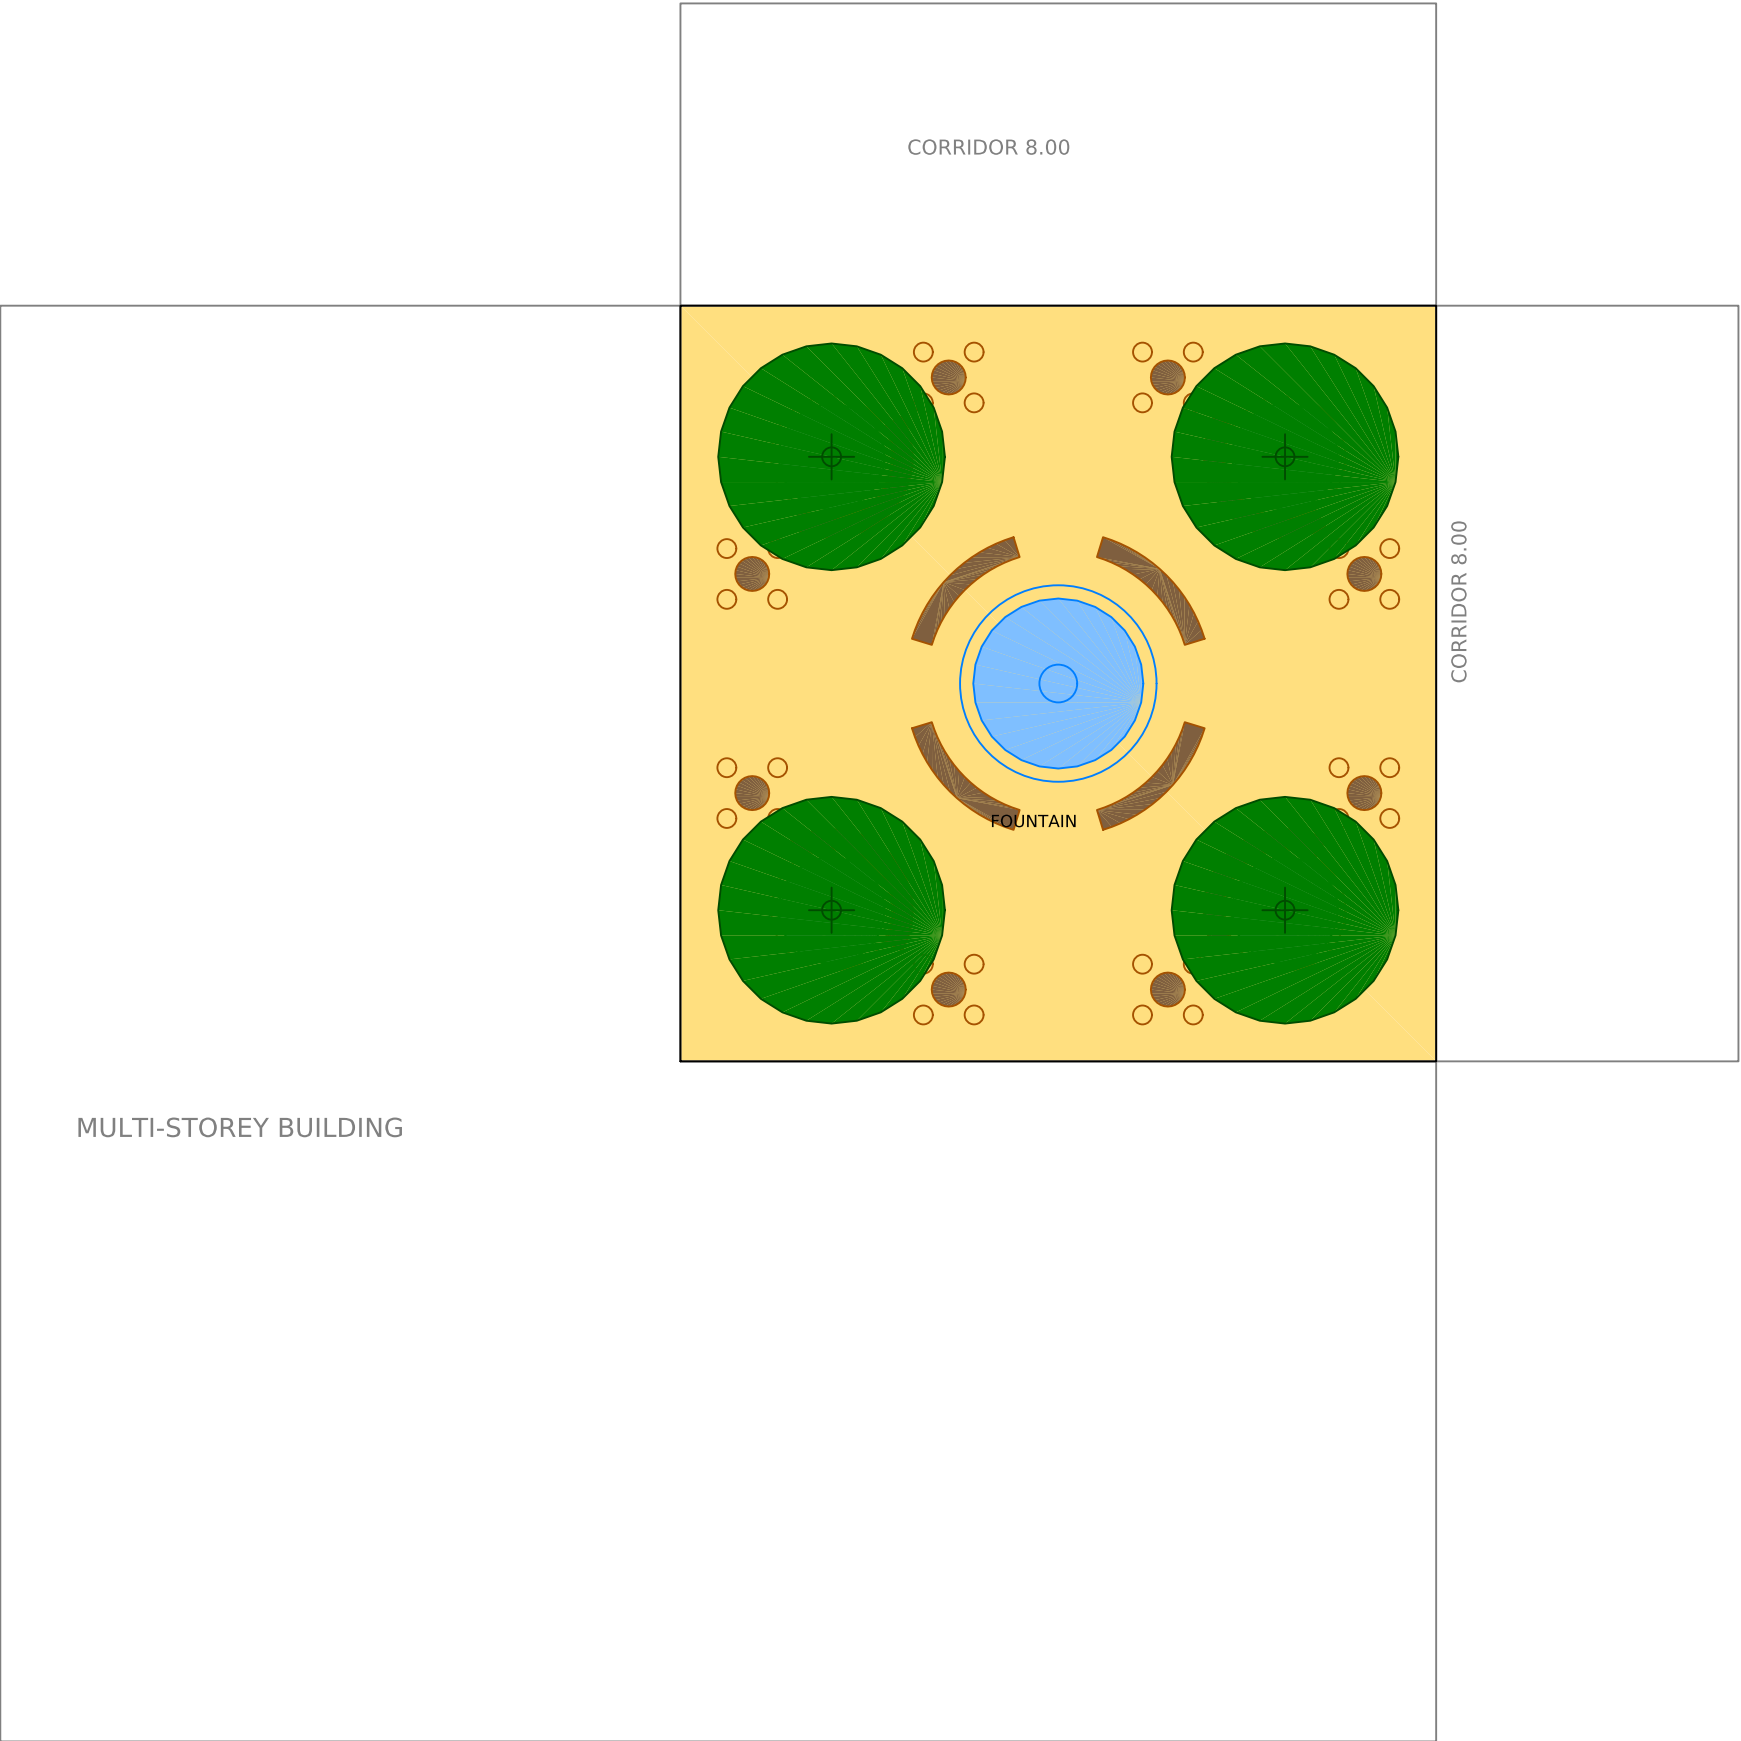

FOUNTAIN COURT - LEGEND

- Limestone paving
- Round fountain dia 5.20
- Shade trees in round planters (4)
- Curved benches + 8 cafe sets
- Planter seat walls

GENERAL NOTES

- ALL DIMENSIONS ARE IN METRES UNLESS OTHERWISE NOTED. LEVELS IN METRES.
- DO NOT SCALE FROM THIS DRAWING. USE FIGURED DIMENSIONS ONLY.
- VERIFY ALL DIMENSIONS ON SITE BEFORE STARTING ANY WORK.
- READ WITH ALL RELEVANT STRUCTURAL AND MEP DRAWINGS AND SPECIFICATIONS.
- COPYRIGHT OF THIS DRAWING IS RESERVED BY THE OFFICE.

KEY PLAN

NORTH

REVISIONS			
REV	DATE	DESCRIPTION	BY
00	30/09/2026	FIRST ISSUE	--

PROJECT
AL-YARMOUK COMMERCIAL SOUQ

LOCATION
MOSUL, IRAQ

CLIENT / OWNER
CLIENT NAME

PROJECT No.
PRJ-2026-002

DRAWING TITLE
FOUNTAIN COURT
ENLARGED LANDSCAPE PLAN

ROLE	NAME	SIGN.	DATE
DESIGNED	IBRAHIM MAHFOUDH		30/09/26
DRAWN	IBRAHIM MAHFOUDH		30/09/26
CHECKED	-		30/09/26
APPROVED	-		30/09/26

SCALE
1:200 @ A3


DATE
30/09/2026

PHASE
DESIGN DEVELOPMENT


STATUS
FOR REVIEW

DRAWING No.
L-103

SHEET
18
OF 21

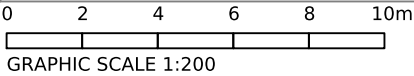

DIMENSION PLAN B - FOUNTAIN COURT

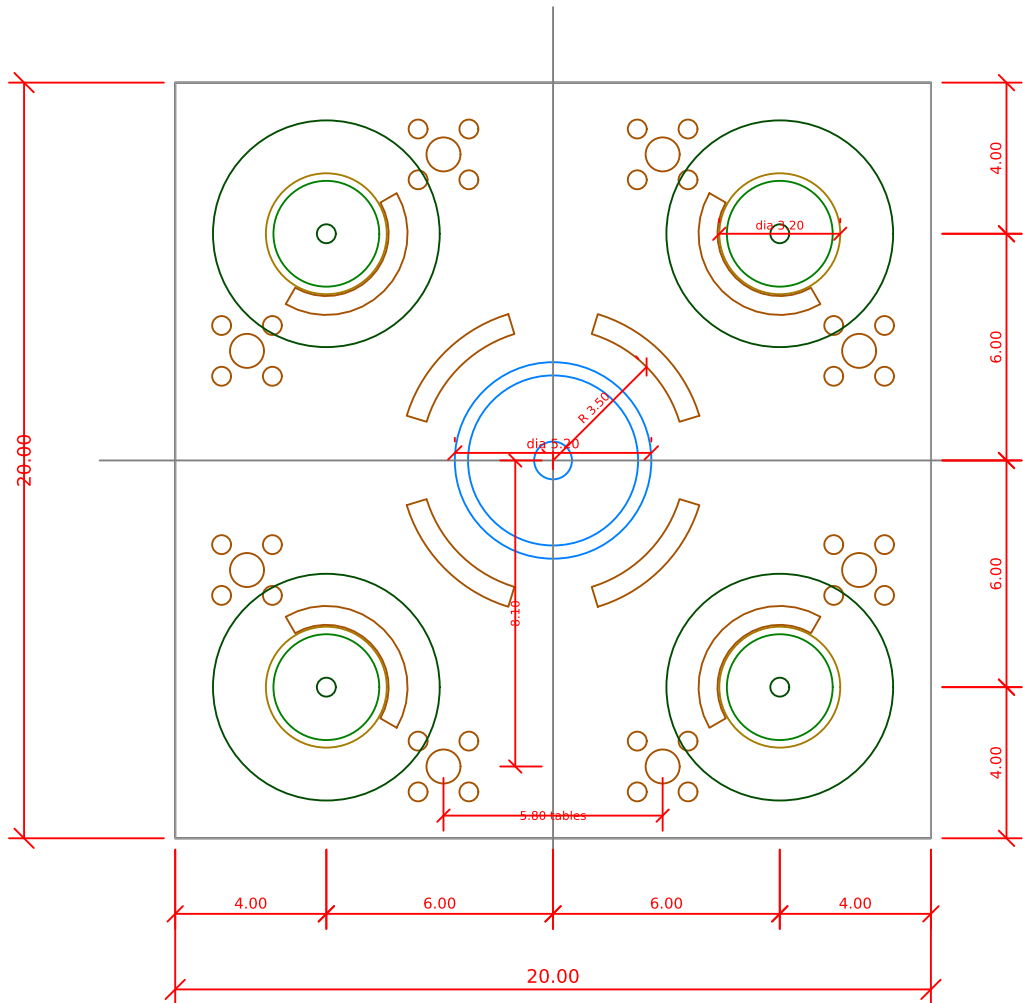

FOUNTAIN COURT - DIMENSIONS

All dimensions in metres.

Axes = centre of the fountain.

Planters on a 12.00 x 12.00 grid (+/-6.00).


Cafe sets 4 per side on +/-2.90 / 8.10.

Curved benches R 3.50, depth 0.55.

GENERAL NOTES


1. ALL DIMENSIONS ARE IN METRES UNLESS OTHERWISE NOTED. LEVELS IN METRES.
2. DO NOT SCALE FROM THIS DRAWING. USE FIGURED DIMENSIONS ONLY.
3. VERIFY ALL DIMENSIONS ON SITE BEFORE STARTING ANY WORK.
4. READ WITH ALL RELEVANT STRUCTURAL AND MEP DRAWINGS AND SPECIFICATIONS.
5. COPYRIGHT OF THIS DRAWING IS RESERVED BY THE OFFICE.

KEY PLAN

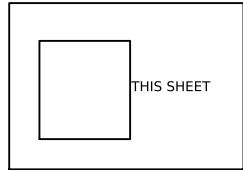

NORTH

N

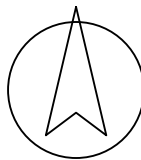

REVISIONS

REV	DATE	DESCRIPTION	BY
00	30/09/2026	FIRST ISSUE	--

PROJECT
AL-YARMOUK COMMERCIAL SOUQ

LOCATION
MOSUL, IRAQ

CLIENT / OWNER
CLIENT NAME

PROJECT No.
PRJ-2026-002

DRAWING TITLE

FOUNTAIN COURT
DIMENSION PLAN

ROLE	NAME	SIGN.	DATE
DESIGNED	IBRAHIM MAHFOUDH		30/09/26
DRAWN	IBRAHIM MAHFOUDH		30/09/26
CHECKED	-		30/09/26
APPROVED	-		30/09/26

SCALE
1:200 @ A3

DATE
30/09/2026

PHASE
DESIGN DEVELOPMENT

STATUS
FOR REVIEW


DRAWING No.

SHEET


L-104

19

OF 21

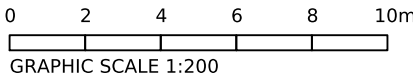

PRAYER HALL & ABLUTION - PLAN WITH DIMENSIONS & FURNITURE

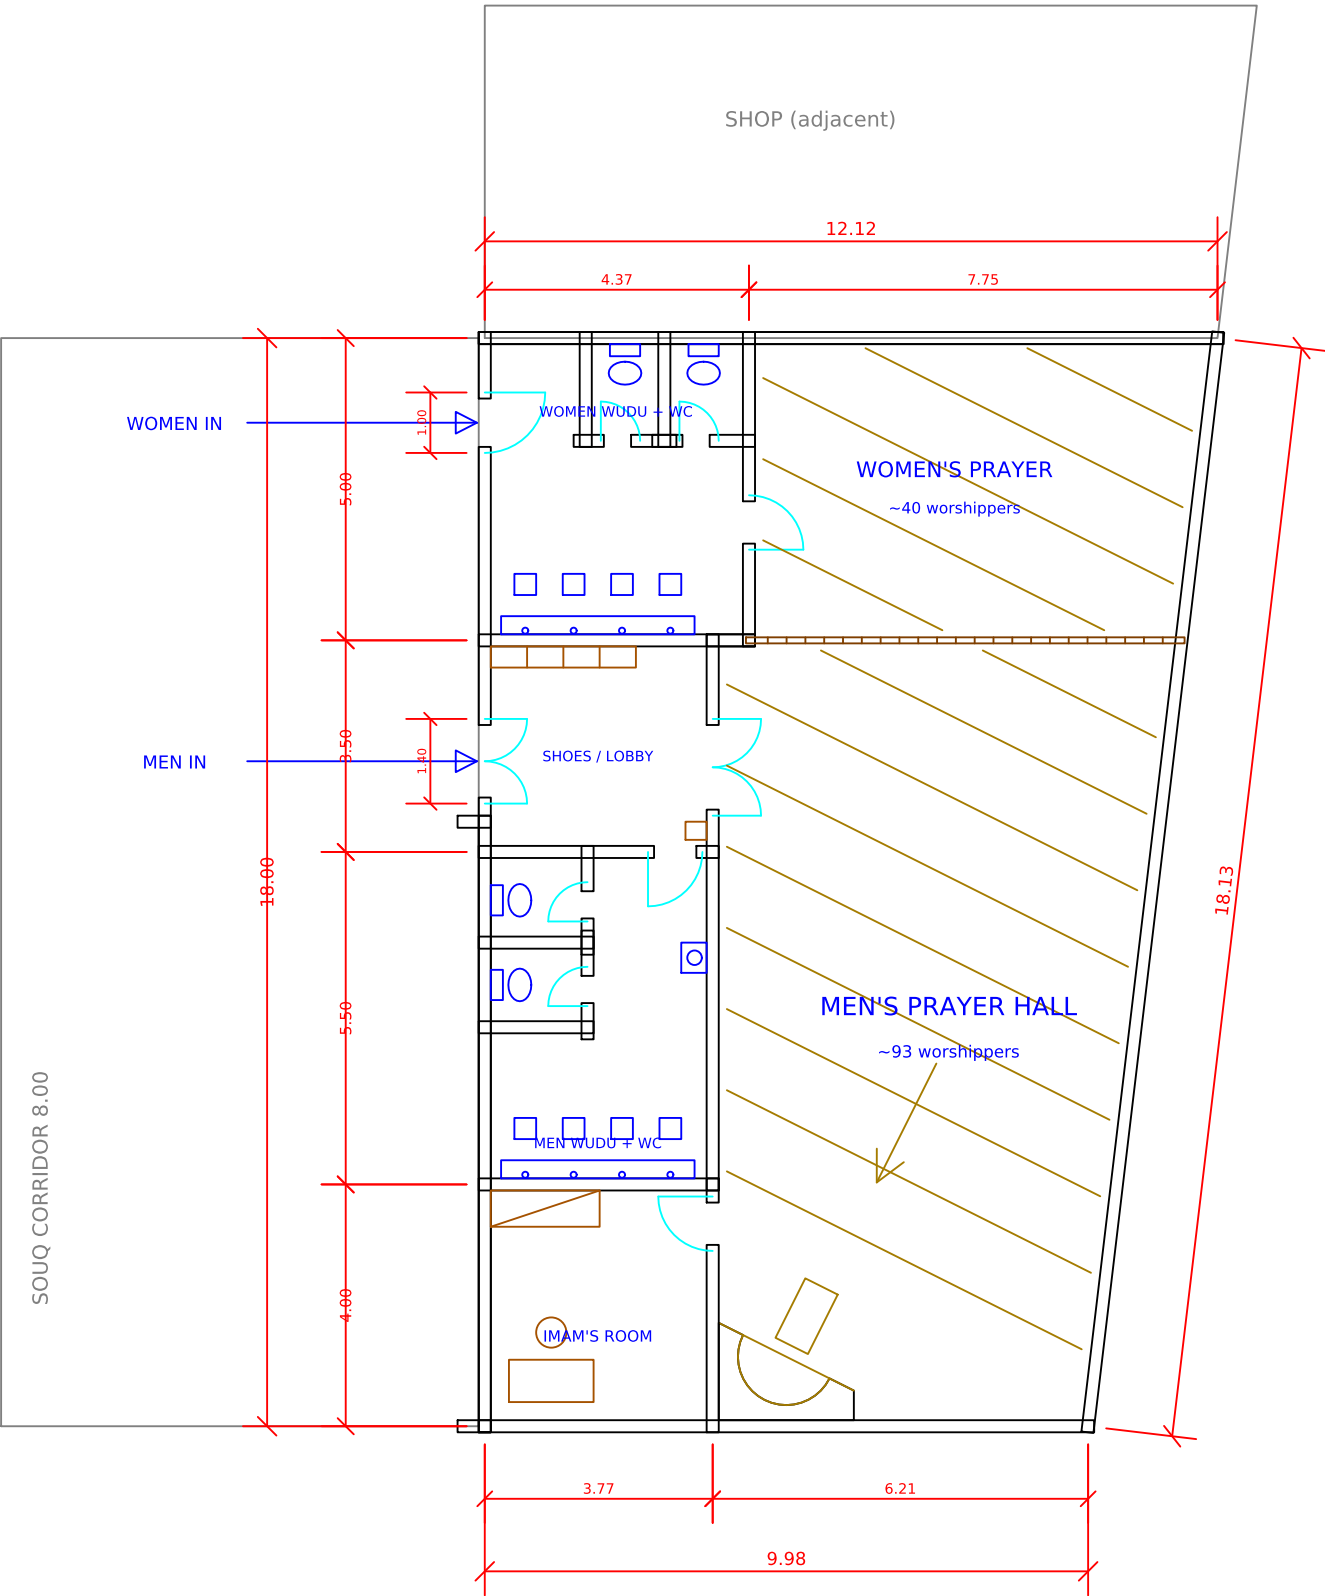

PRAYER HALL - SCHEDULE


Men's prayer hall	91 m2 (~93 persons)
Women's prayer	37 m2 (~40 persons)
Men wudu: 4 taps + 2 WC + basin	21 m2
Women wudu: 4 taps + 2 WC	22 m2
Shoe lobby	13 m2
Imam's room	15 m2
TOTAL	199 m2

Mihrab recessed in the qibla wall, axis 191 deg
(qibla assumes drawing +Y = north - to verify).
Mashrabiya screen between men / women halls.
Separate entrances from the souq corridor.
Prayer rows @ 1.20 m, perpendicular to qibla.

GENERAL NOTES

1. ALL DIMENSIONS ARE IN METRES UNLESS OTHERWISE NOTED. LEVELS IN METRES.
2. DO NOT SCALE FROM THIS DRAWING. USE FIGURED DIMENSIONS ONLY.
3. VERIFY ALL DIMENSIONS ON SITE BEFORE STARTING ANY WORK.
4. READ WITH ALL RELEVANT STRUCTURAL AND MEP DRAWINGS AND SPECIFICATIONS.
5. COPYRIGHT OF THIS DRAWING IS RESERVED BY THE OFFICE.

KEY PLAN

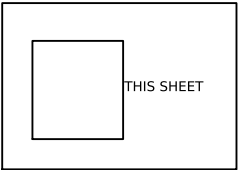

NORTH



REVISIONS

REV	DATE	DESCRIPTION	BY
00	30/09/2026	FIRST ISSUE	--

PROJECT
AL-YARMOUK COMMERCIAL SOUQ

LOCATION
MOSUL, IRAQ

CLIENT / OWNER
CLIENT NAME

PROJECT No.
PRJ-2026-002

DRAWING TITLE
PRAYER HALL & ABLUTION
PLAN - DIMENSIONS & FURNITURE

ROLE	NAME	SIGN.	DATE
DESIGNED	IBRAHIM MAHFOUDH		30/09/26
DRAWN	IBRAHIM MAHFOUDH		30/09/26
CHECKED	-		30/09/26
APPROVED	-		30/09/26

SCALE
1:125 @ A3


DATE
30/09/2026

PHASE
DESIGN DEVELOPMENT

STATUS
FOR REVIEW


DRAWING No.
A-401

SHEET
20
OF 21

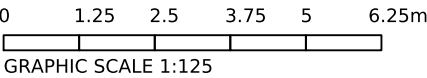



PUBLIC TOILETS - PLANS WITH DIMENSIONS & FIXTURES

PUBLIC WC 1 (north-west) - 5 + 5 cubicles

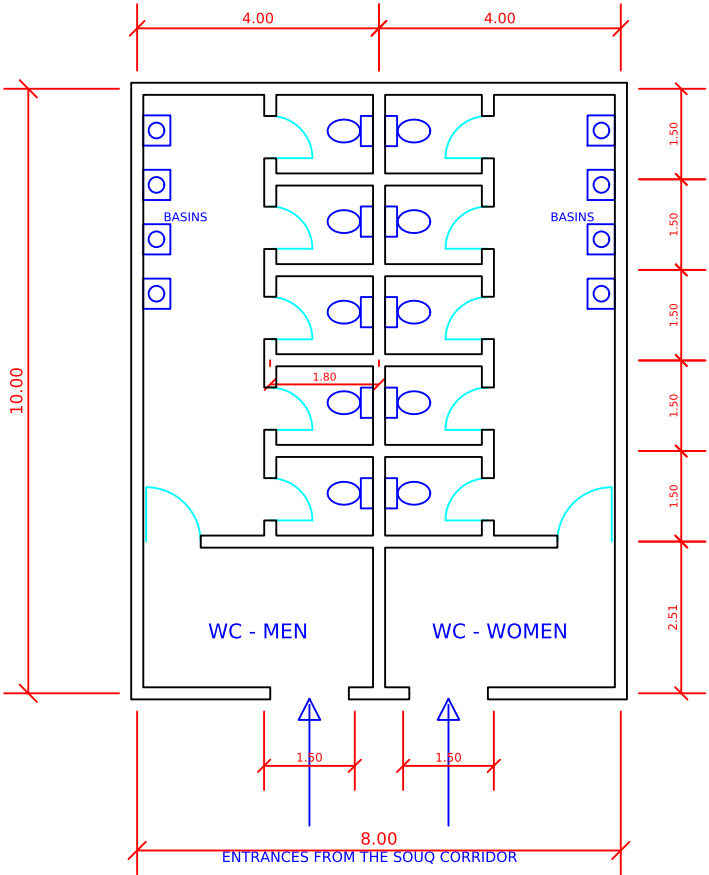

Cubicles ~1.30 x 1.60, doors open inward 0.70; basins on outer walls; 1.50 open entrances.


PUBLIC WC 2 (north-east) - men + women side by side

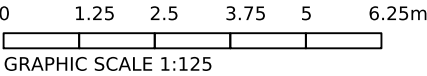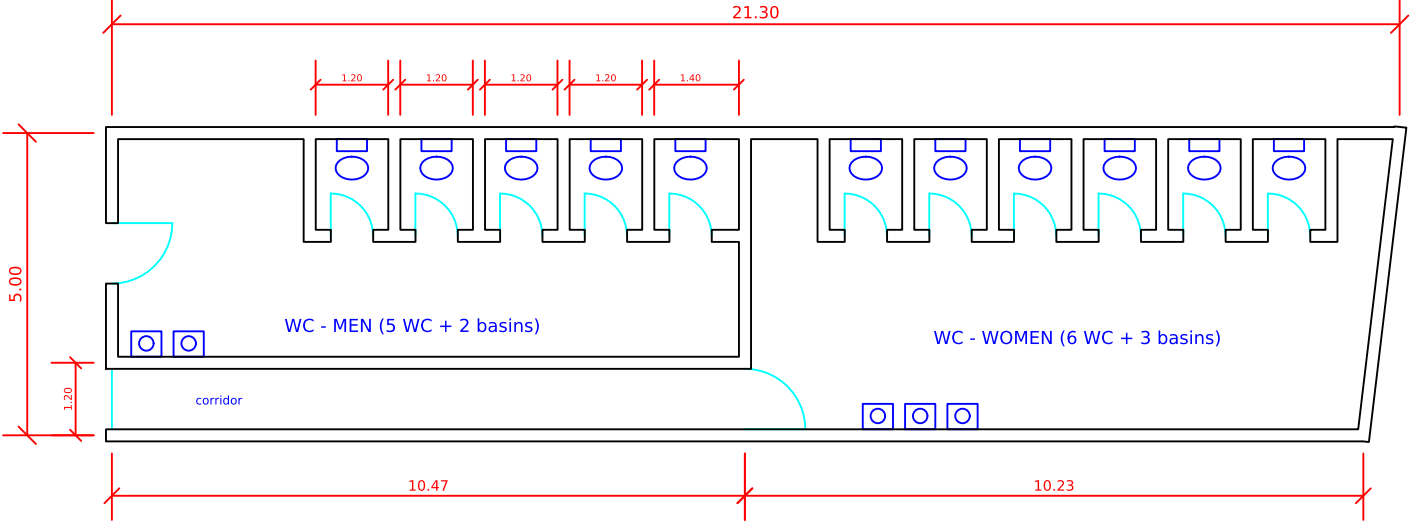

GENERAL NOTES

1. ALL DIMENSIONS ARE IN METRES UNLESS OTHERWISE NOTED. LEVELS IN METRES.
2. DO NOT SCALE FROM THIS DRAWING. USE FIGURED DIMENSIONS ONLY.
3. VERIFY ALL DIMENSIONS ON SITE BEFORE STARTING ANY WORK.
4. READ WITH ALL RELEVANT STRUCTURAL AND MEP DRAWINGS AND SPECIFICATIONS.
5. COPYRIGHT OF THIS DRAWING IS RESERVED BY THE OFFICE.

KEY PLAN

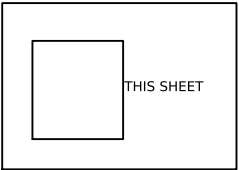

NORTH



REVISIONS

REV	DATE	DESCRIPTION	BY
00	30/09/2026	FIRST ISSUE	--

PROJECT
AL-YARMOUK COMMERCIAL SOUQ

LOCATION
MOSUL, IRAQ

CLIENT / OWNER
CLIENT NAME

PROJECT No.
PRJ-2026-002

DRAWING TITLE
PUBLIC TOILETS
PLANS - DIMENSIONS & FIXTURES

ROLE	NAME	SIGN.	DATE
DESIGNED	IBRAHIM MAHFOUDH		30/09/26
DRAWN	IBRAHIM MAHFOUDH		30/09/26
CHECKED	-		30/09/26
APPROVED	-		30/09/26

SCALE
1:125 @ A3

DATE
30/09/2026

PHASE
DESIGN DEVELOPMENT

STATUS
FOR REVIEW

DRAWING No.

A-402

SHEET

21
OF 21