
المخطط العام - المقترح ب: القلب الأخضر

MASTER PLAN - PROPOSAL B: THE GREEN HEART

مجمع الشلالات السكني · القطعة 157 مقاطعة 53 بابيوخت · فرصة هيئة استثمار نينوى 5/2026

UTM 38S · SCALE 1:2500 (A3) · 199,177 m2 · 2026-10-21

- فلل 400 م² (86)
- دور 200 م² (125)
- برجان 20 طابقاً (152 شقة)
- خدمات وبنى تحتية
- الحديقة المركزية
- حدائق وبستان وساحة رياضية
- طرق
- ماء

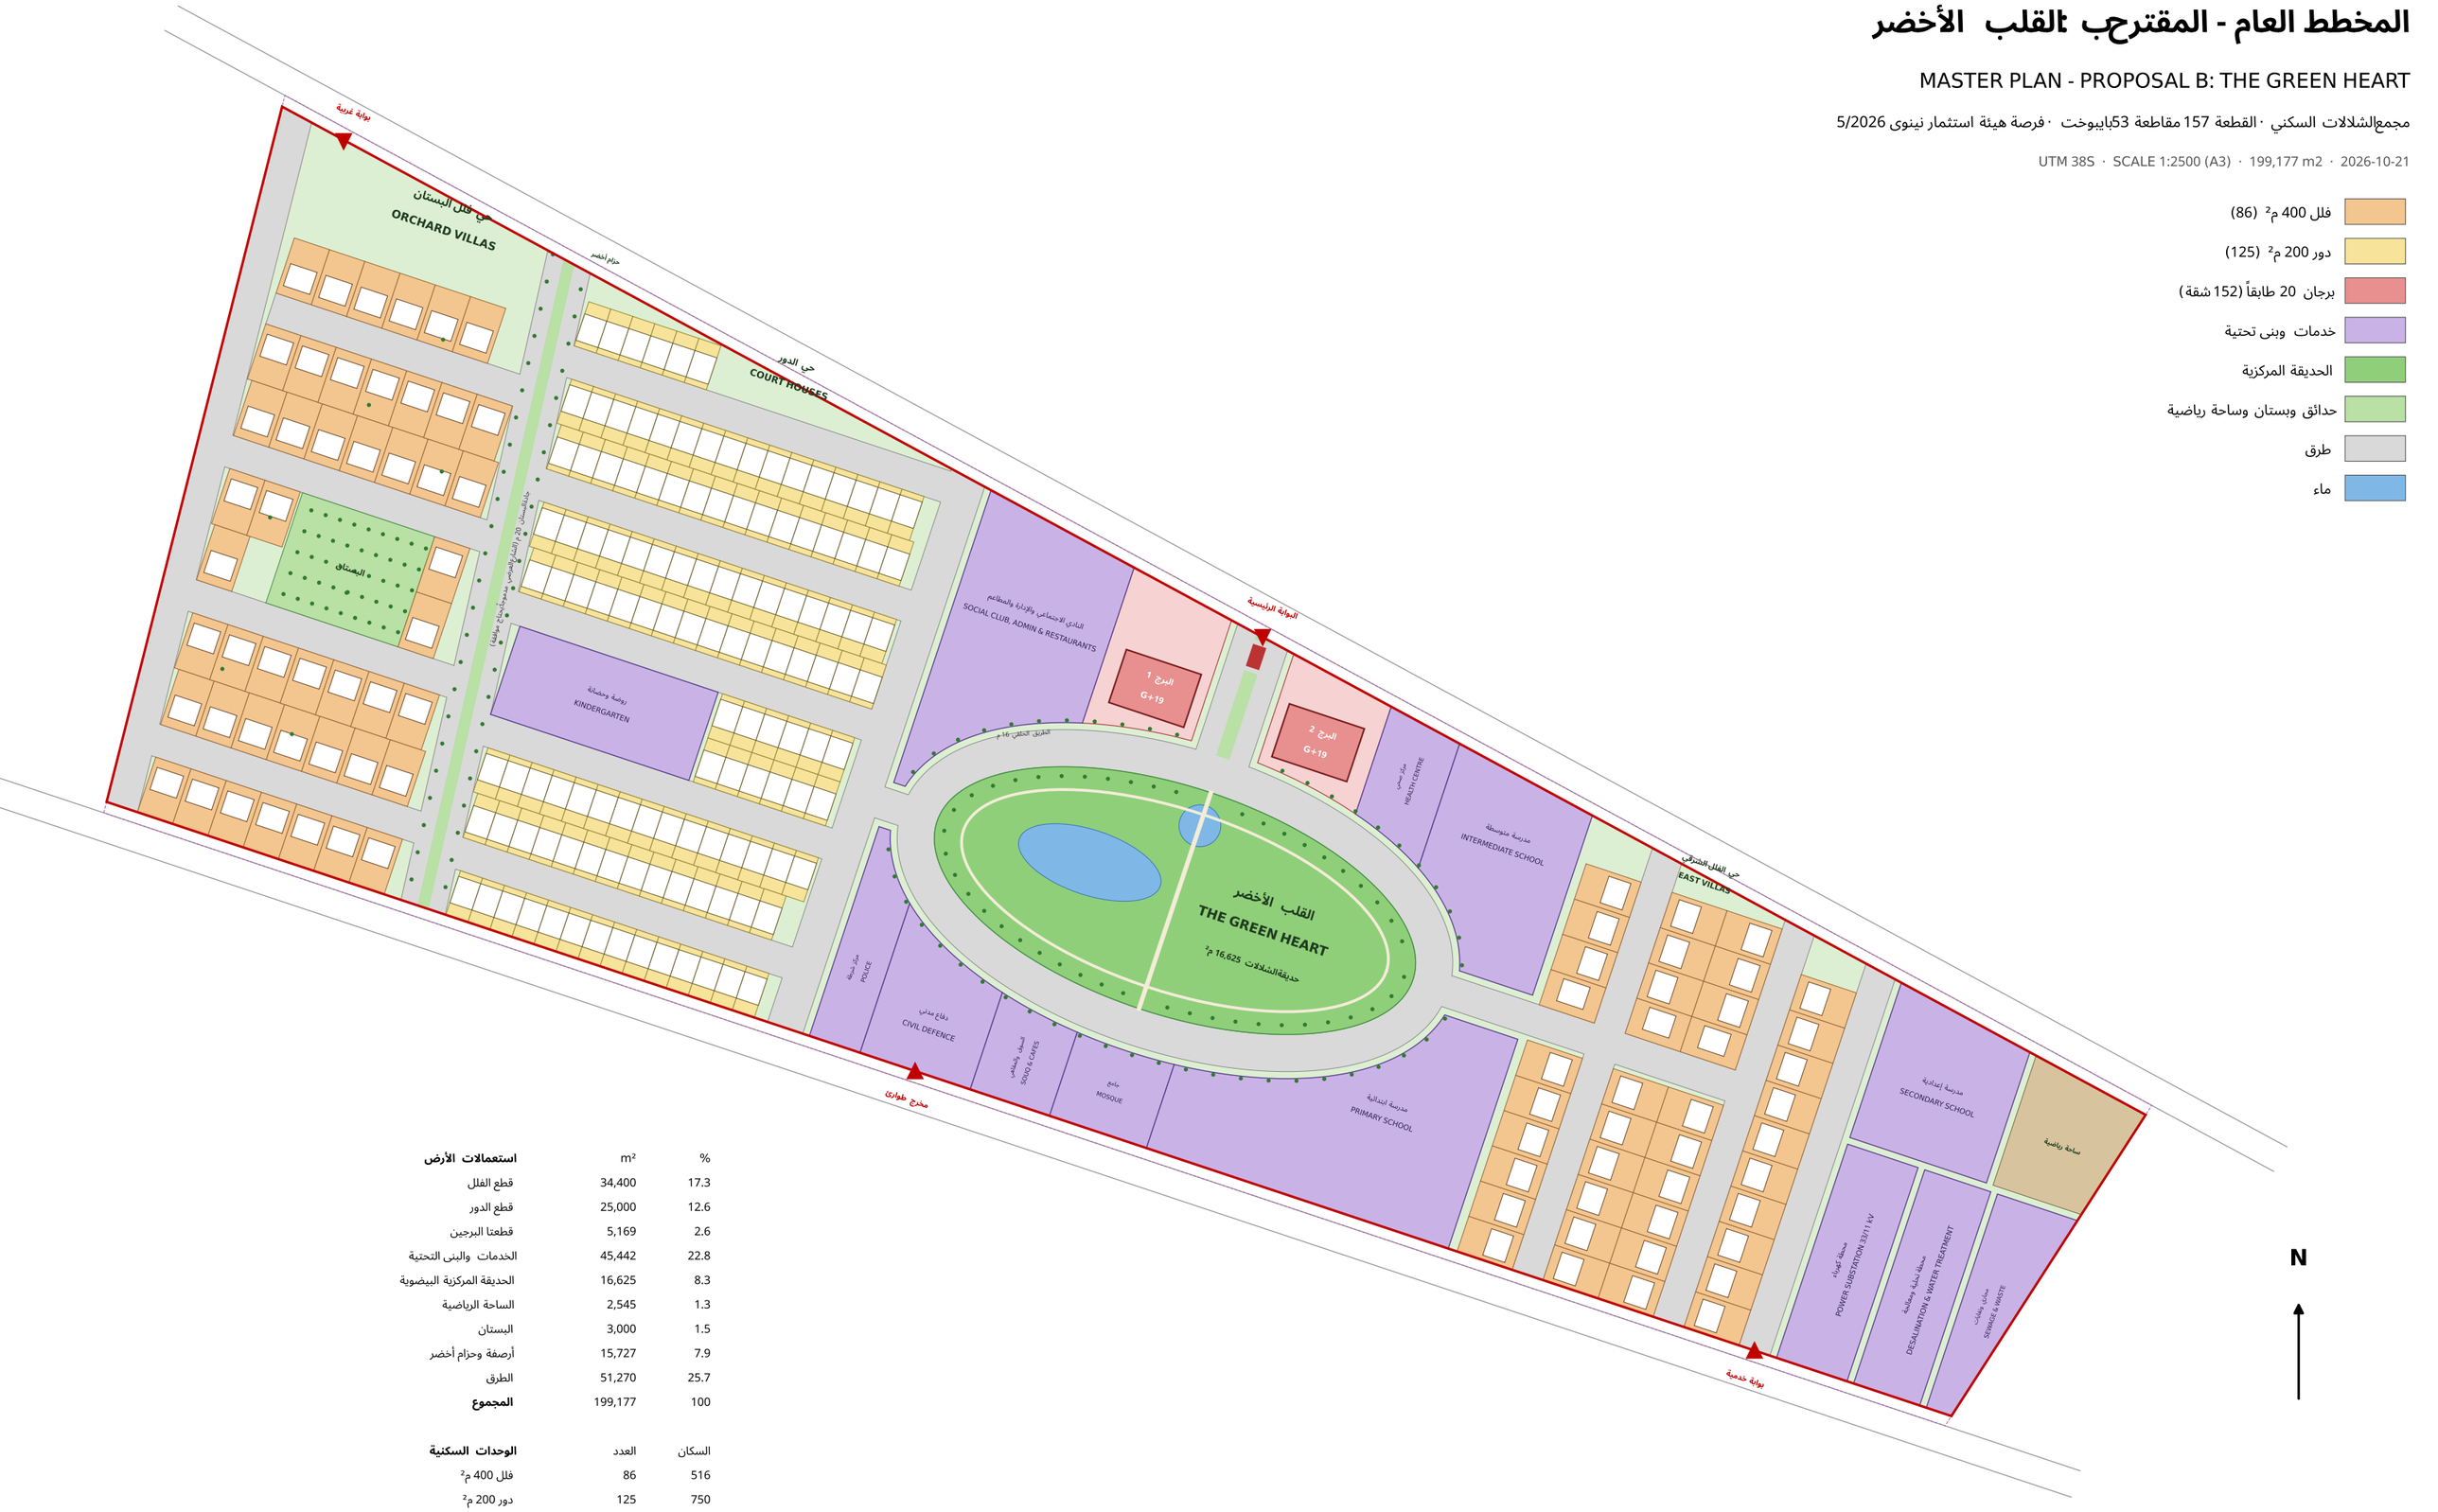

استعمالات الأرض	m²	%
قطع الفلل	34,400	17.3
قطع الدور	25,000	12.6
قطعتا البرجين	5,169	2.6
الخدمات والبنى التحتية	45,442	22.8
الحديقة المركزية البيضوية	16,625	8.3
الساحة الرياضية	2,545	1.3
البستان	3,000	1.5
أرصفة وحزام أخضر	15,727	7.9
الطرق	51,270	25.7
المجموع	199,177	100

الوحدات السكنية	العدد	السكان
فلل 400 م²	86	516
دور 200 م²	125	750
شقق 140 M2 م²	76	304
شقق 180 M3 م²	76	456
المجموع	363	2,026

الكثافة الإجمالية 102 شخص/هكتار

الخضرة العامة 10.9 م² للفرد